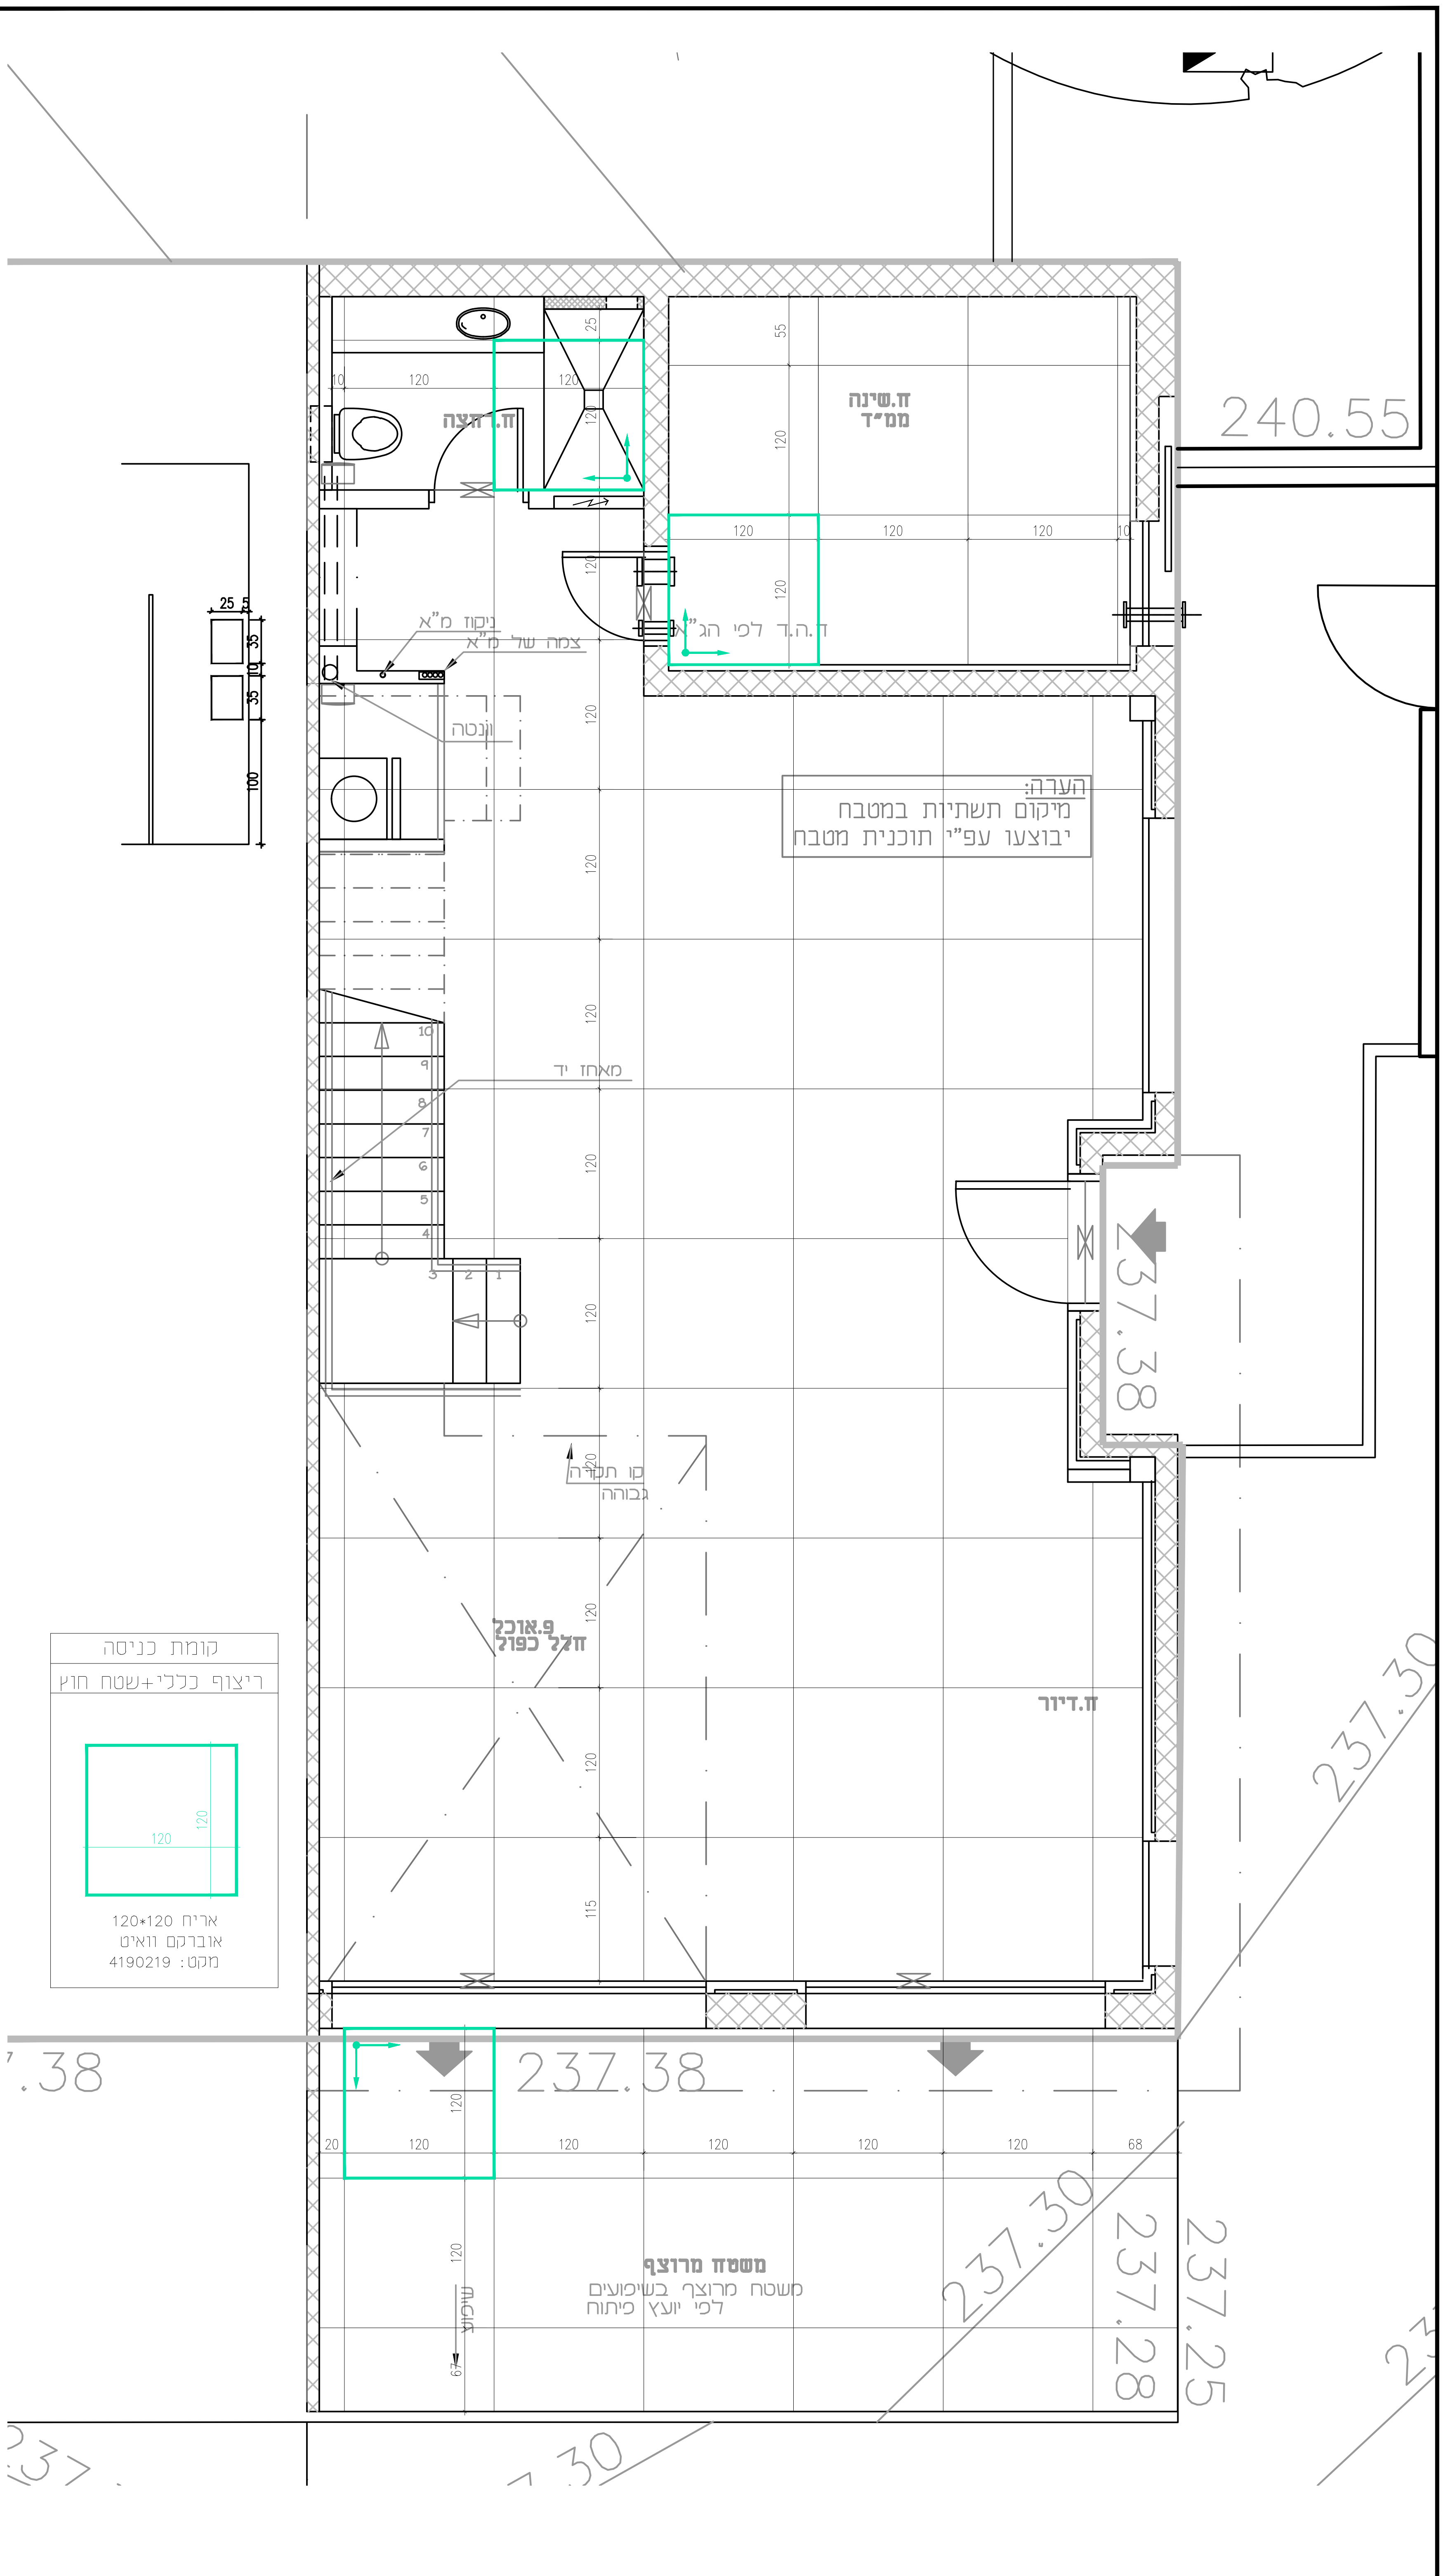

פרויקט:	תכנית:	גליון מס':	גודל גיליון:	הערות:
אלפי מנשה דירה 14	ריצוף-קרקע	10	--	1. על המבצע לבדוק את התאמת התכנית בשטח, לפני הבנייה, ולבקר את המידות. על כל טעות ו/או אי התאמה יש לעדכן משרד מתכנן. 2. אין לקבוע מידות ע"פ שרטוט. המידות המחייבות הן המידות שנמדדו בשטח לאחר ביצוע. 3. המידות בתכנית הן ברוטו-ללא חיפוי גמר. 4. יתכנו שינויים בהתאם להוראות הביצוע הסופי. 5. כל התכניות נשארות רכוש המתכנן: אין לעשות בהן שימוש ללא אישור בכתב המתכנן. 6. כל ההערות תקפות אלא אם צוין אחרת.
	○ לעיון ● לאישור ○ למכרז ○ לביצוע	תאריך: 20.8.2026	קנ"מ: 1:50	

RK
RUTH KOLSKY
תכנון - עיצוב - השראה

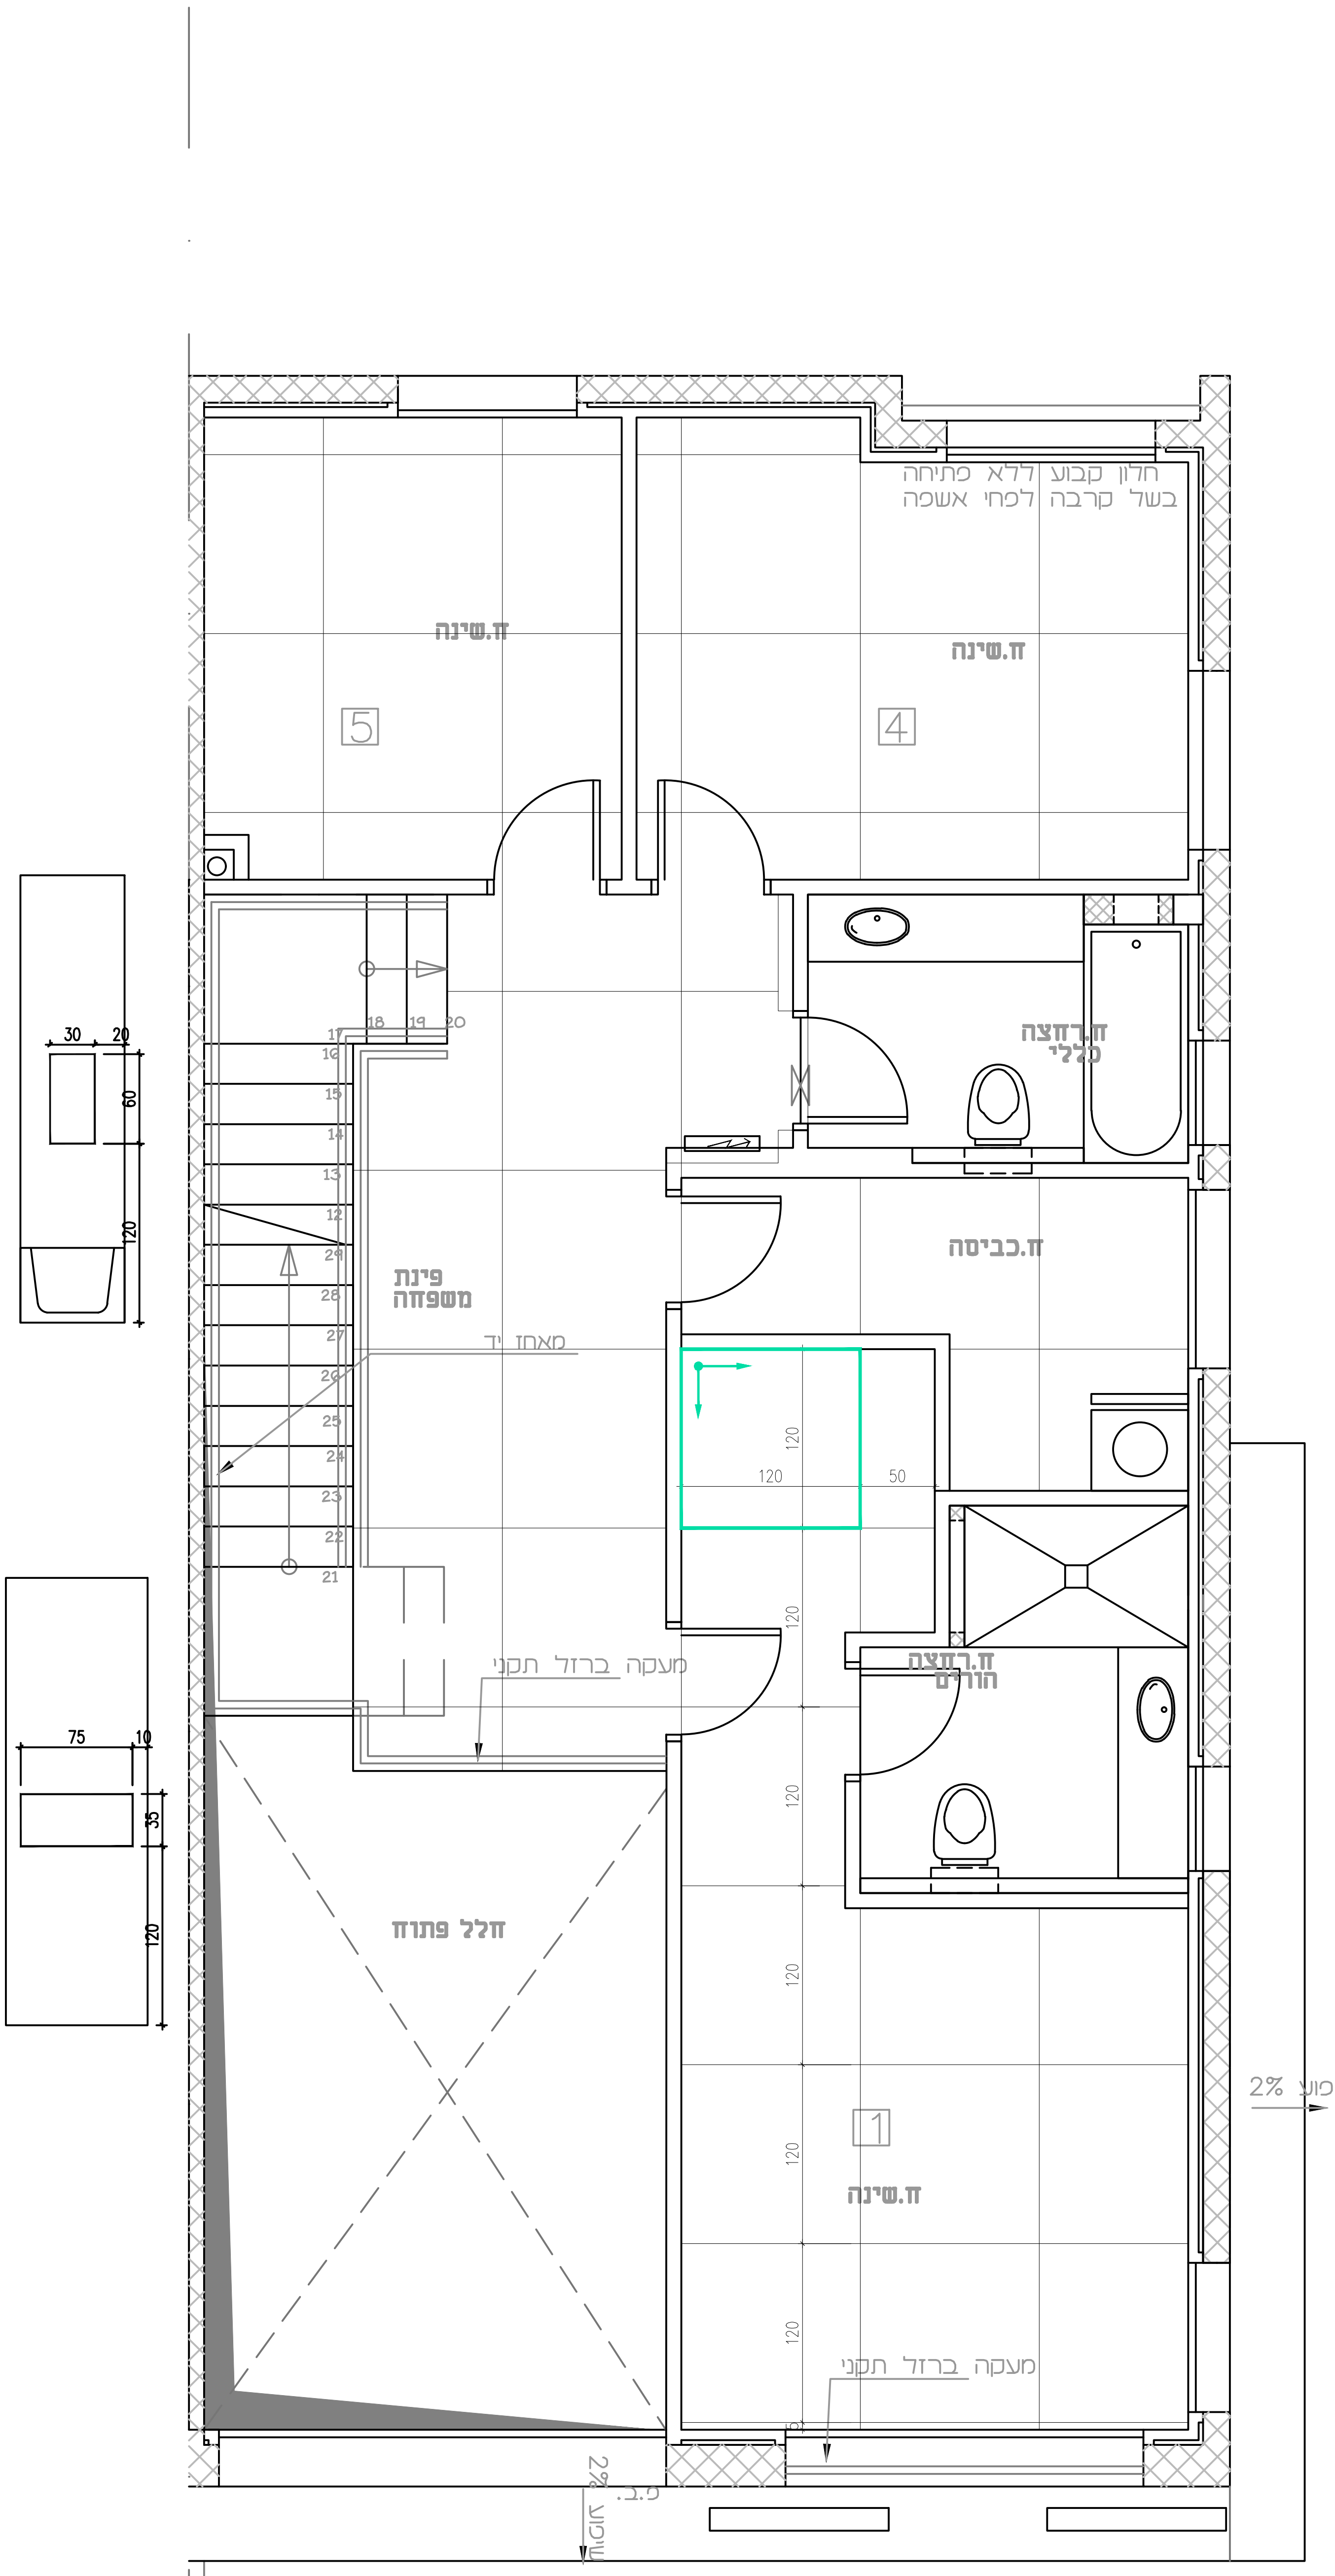

קומה א'

ריצוף

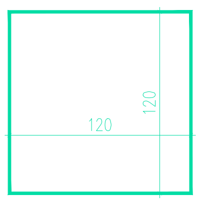

אריח 120*120
אוברקם וואיט
מקט: 4190219

פרויקט:
אלפי מנשה
דירה 14

תכנית:
ריצוף-קומה א'
○ לעיון ● לאישור
○ למכרז ○ לביצוע

גליון מס':
11

תאריך:
20.8.2026

גודל גיליון:
--

קנ"מ:
1:50

הערות:
1. על המבצע לבדוק את התאמת התכנית בשטח, לפני הבנייה, ולבקר את המידות. על כל טעות ו/או אי התאמה יש לעדכן משרד מתכנן.
2. אין לקבוע מידות ע"פ שרטוט. המידות המחייבות הן המידות שנמדדו בשטח לאחר ביצוע.
3. המידות בתכנית הן ברוטו-ללא חיפוי גמר.
4. יתכנו שינויים בהתאם להוראות הביצוע הסופי.
5. כל התכניות נשארות רכוש המתכנן: אין לעשות בהן שימוש ללא אישור בכתב המתכנן.
6. כל ההערות תקפות אלא אם צוין אחרת.

RK
RUTH KOLSKY
תכנון - עיצוב - השראה

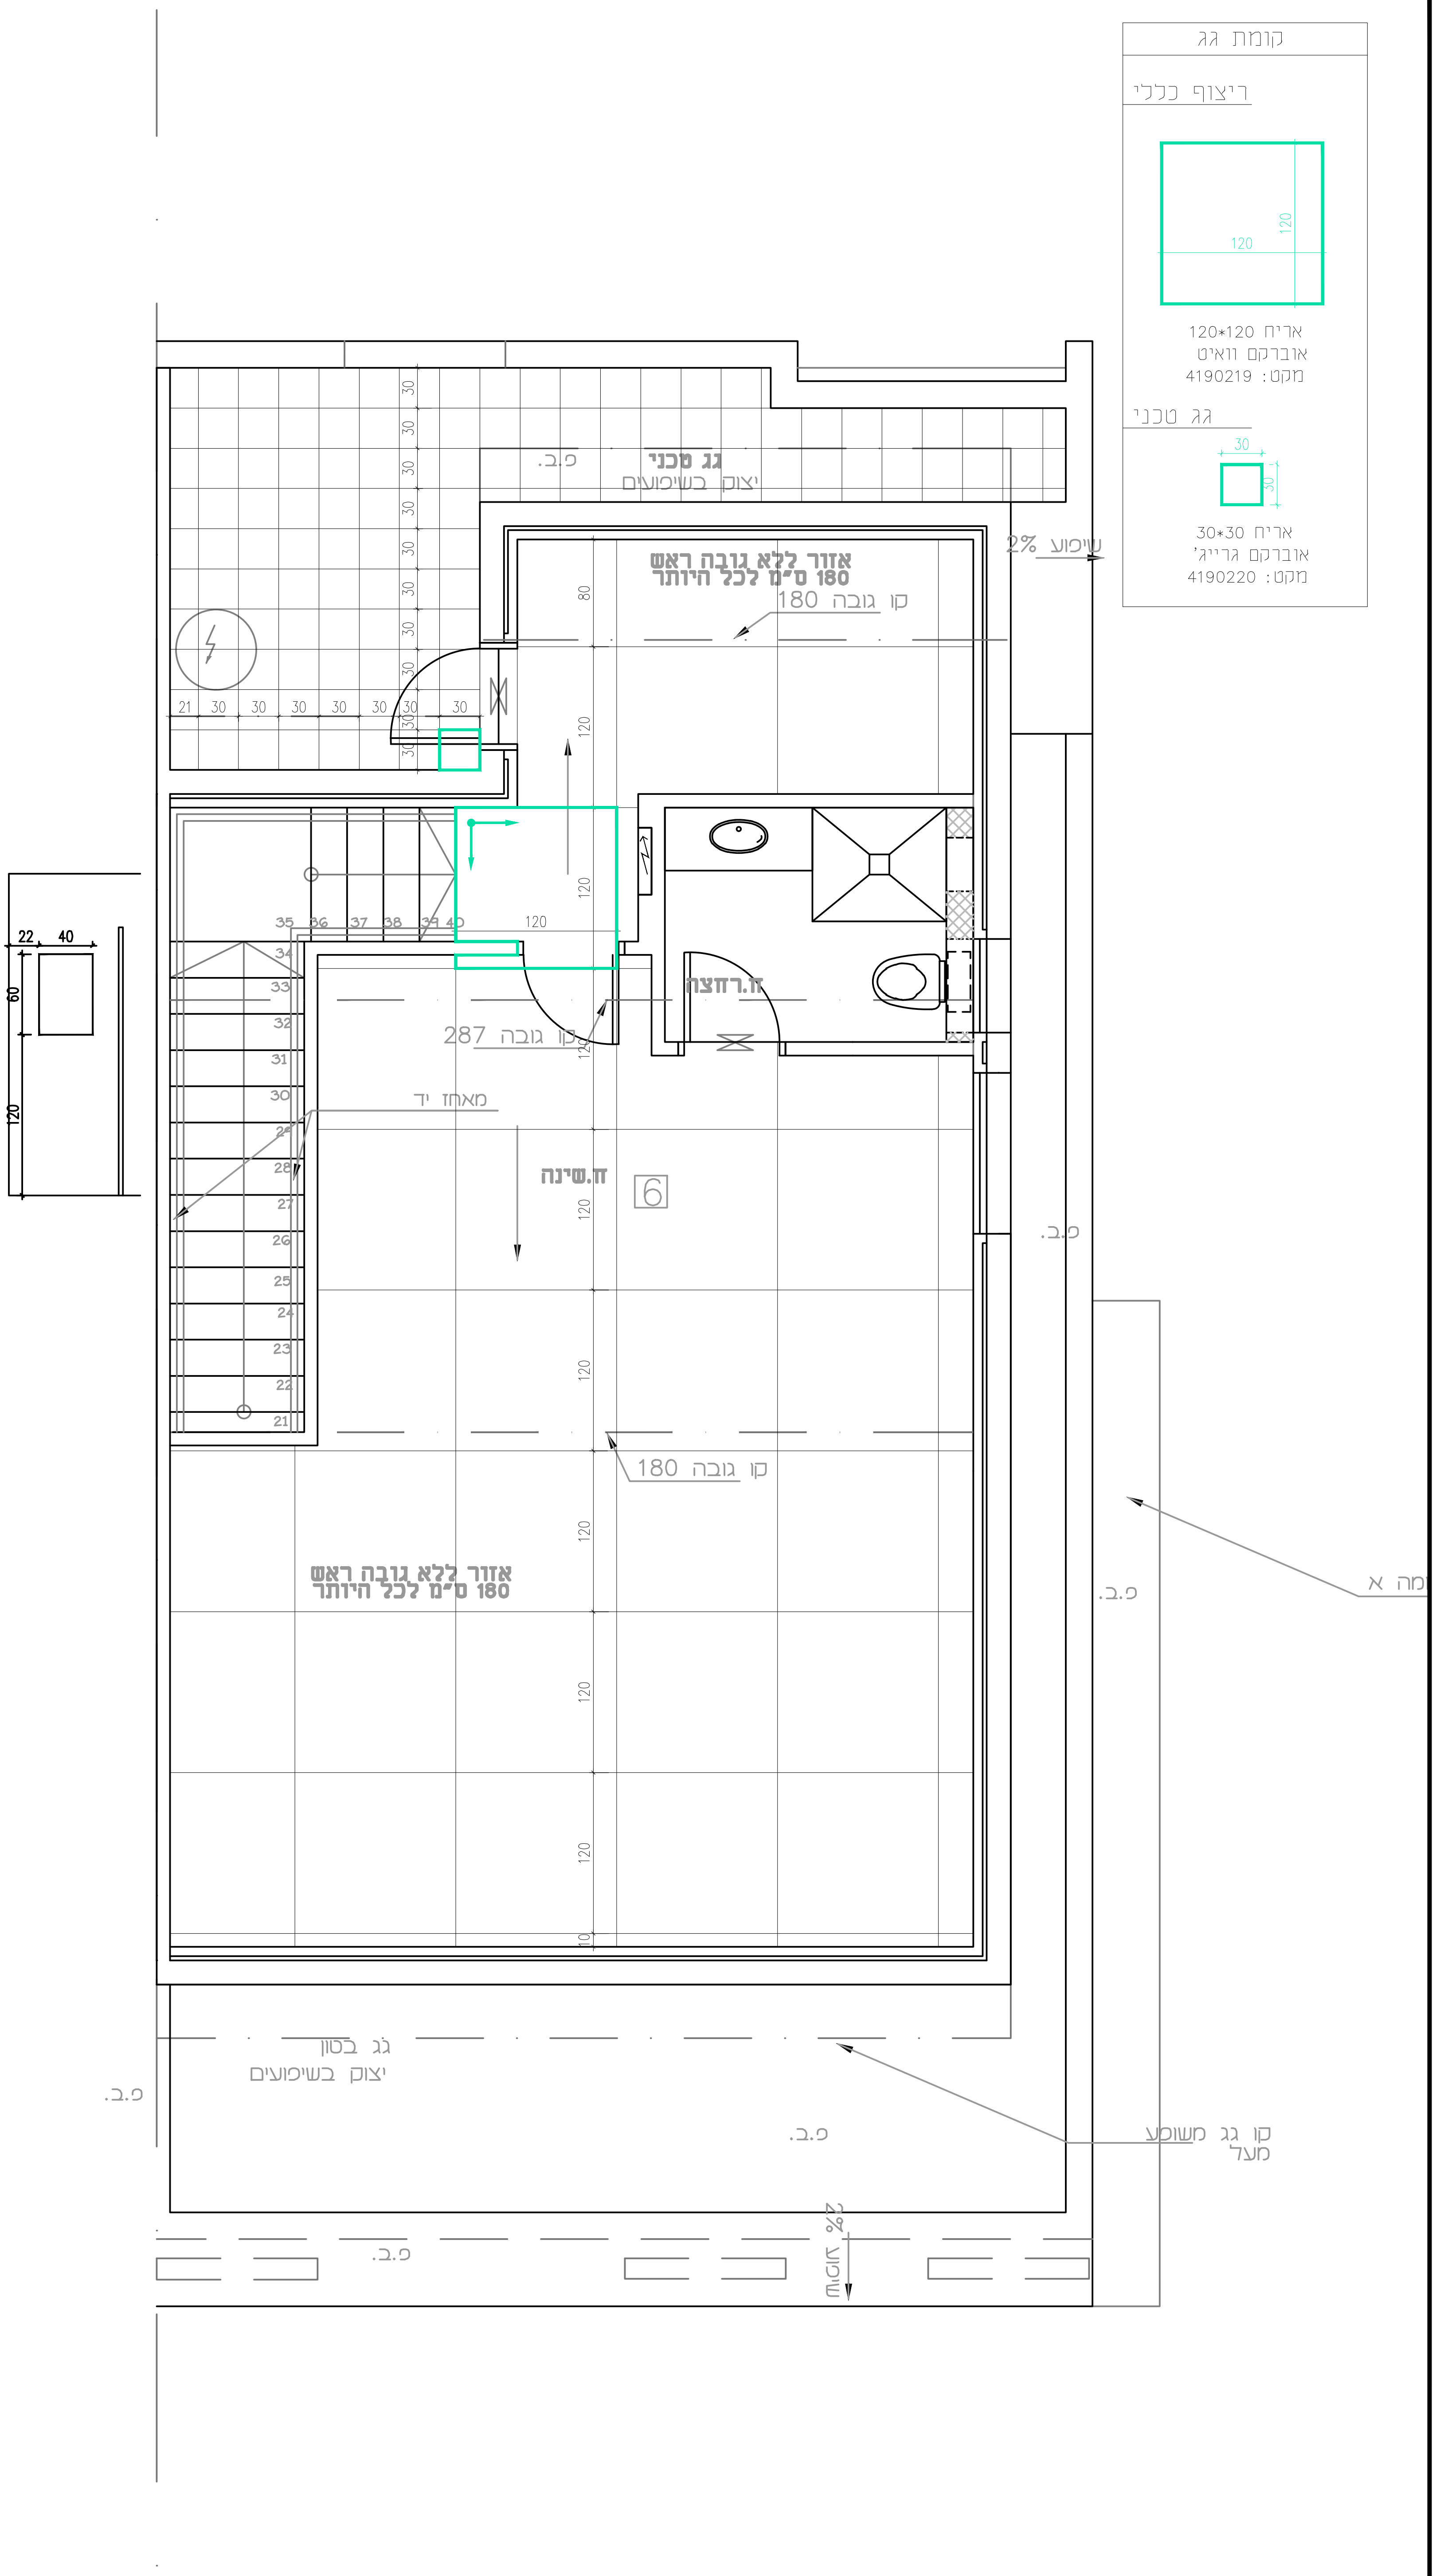

קומת גג

ריצוף כללי

אריח 120*120
אוברקם וואיט
מקט: 4190219

גג טכני

אריח 30*30
אוברקם גרייג'
מקט: 4190220

פרויקט: אלפי מנשה דירה 14	תכנית: ריצוף-גג	גליון מס': 12	גודל גיליון: --
	○ לעיון ● לאישור ○ למכרז ○ לביצוע	תאריך: 20.8.2026	קנ"מ: 1:50

הערות:
1. על המבצע לבדוק את התאמת התכנית בשטח, לפני הבנייה, ולבקר את המידות. על כל טעות ו/או אי התאמה יש לעדכן משרד מתכנן.
2. אין לקבוע מידות ע"פ שרטוט. המידות המחייבות הן המידות שנמדדו בשטח לאחר ביצוע.
3. המידות בתכנית הן ברוטו-ללא חיפוי גמר.
4. יתכנו שינויים בהתאם להוראות הביצוע הסופי.
5. כל התכניות נשארות רכוש המתכנן: אין לעשות בהן שימוש ללא אישור בכתב המתכנן.
6. כל ההערות תקפות אלא אם צוין אחרת.

מבט על

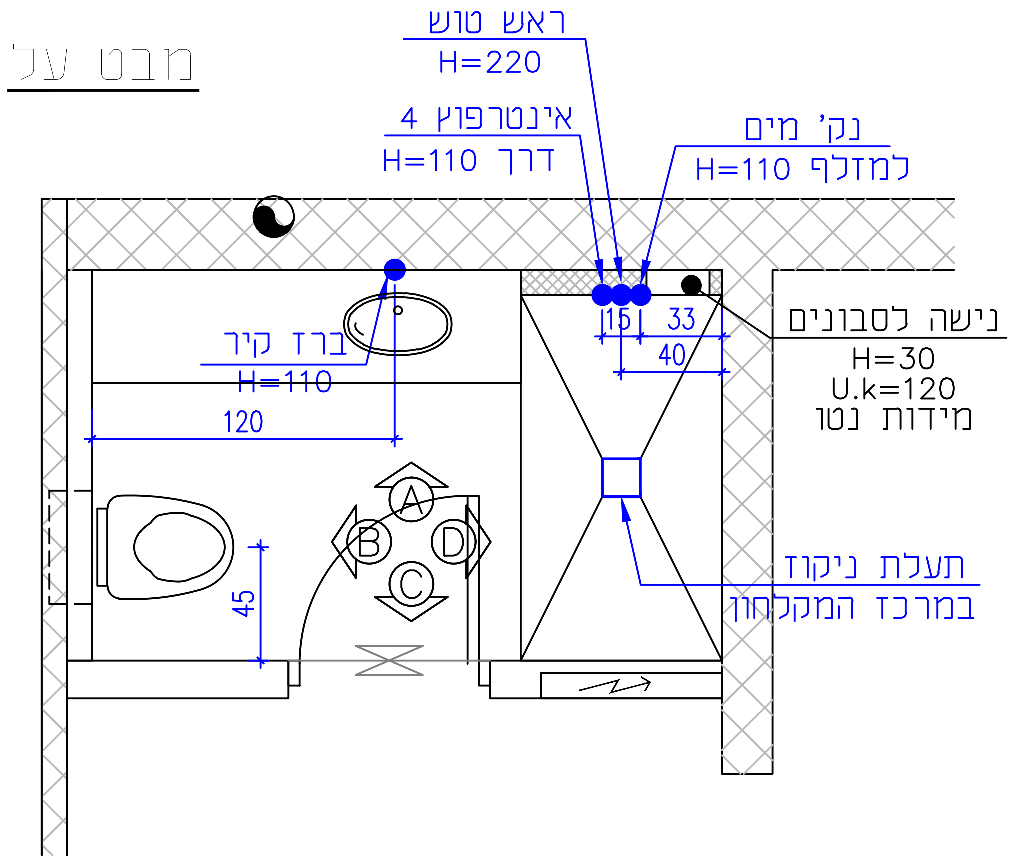

ריצוף

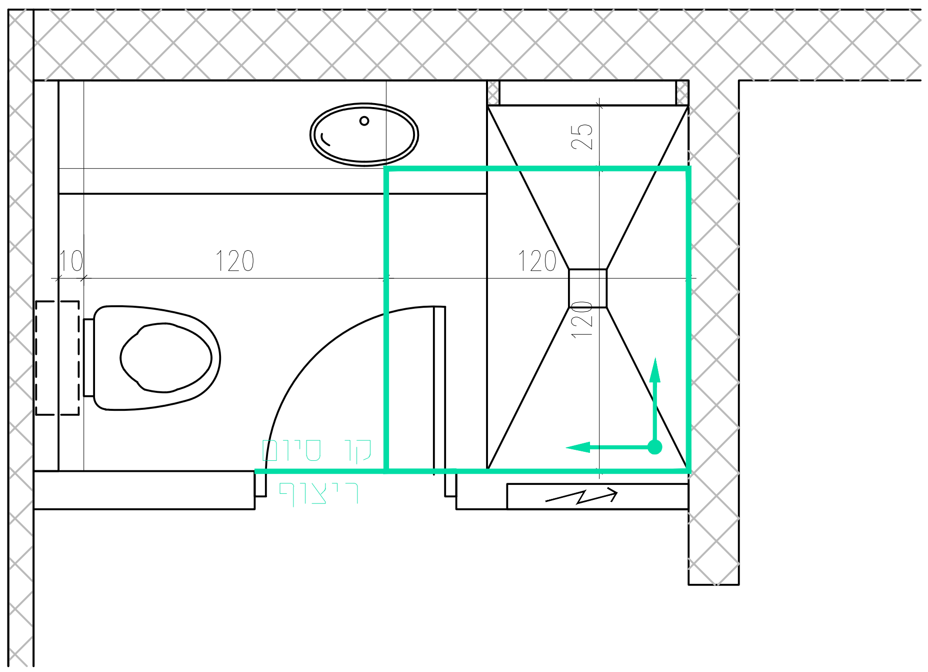

פריסה A

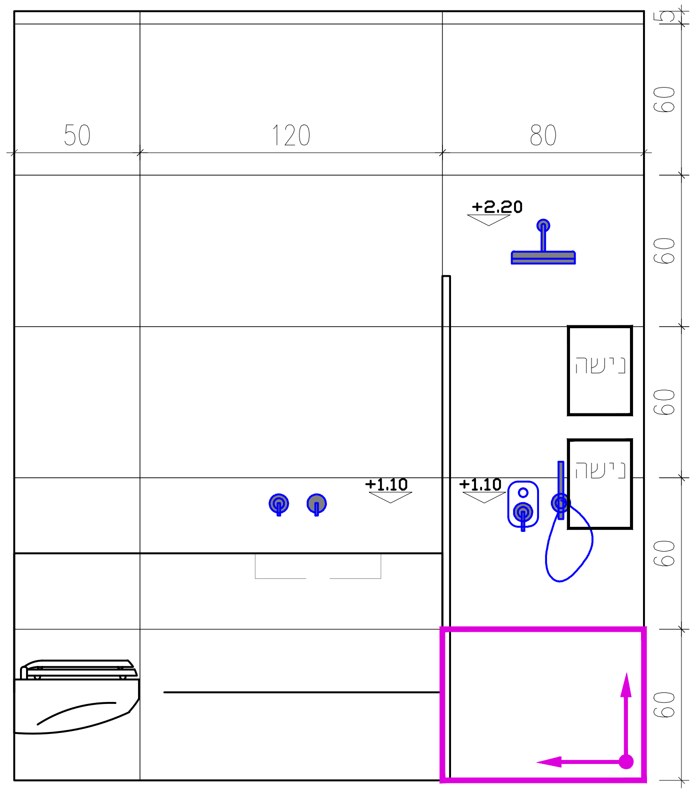

פריסה B

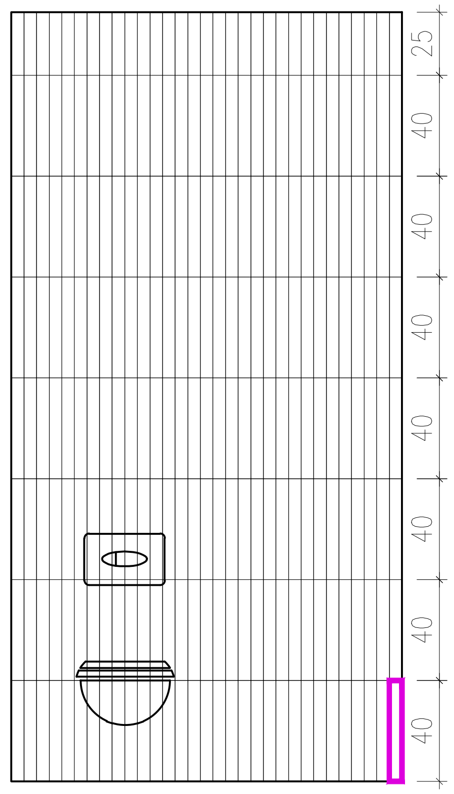

פריסה C

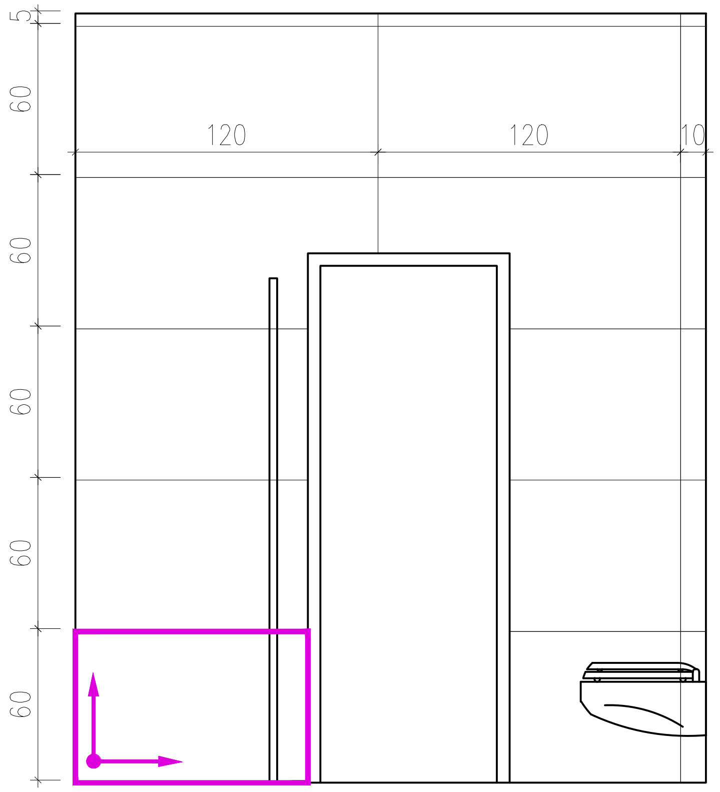

פריסה D

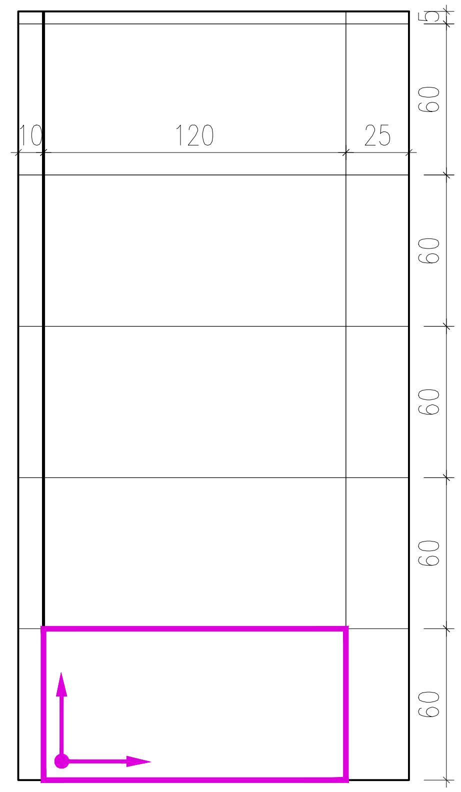

ח.רחצה אורחים-קרקע

ריצוף

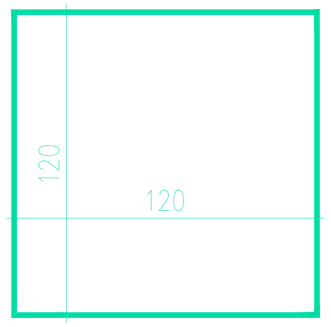

אריח 120*120
אוברקם וואיט
מקט: 4190219

חיפוי

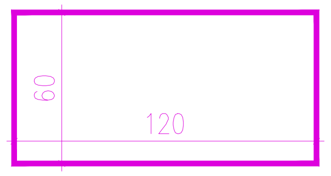

אריח 60*120
אוברקם וואיט
מקט: 4190218

דקור-בריקים

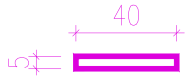

אריח 5*40
באלי איסלה אופ פרינס
מקט: 447136

פרויקט:	תכנית:	גליון מס':	גודל גיליון:	
אלפי מנשה דירה 14	פריסות ח.רחצה אורחים-קרקע	13	A3	🟩 – ריצוף
	○ לעיון ● לאישור ○ למכרז ○ לביצוע	תאריך: 20.8.2026	קנ"מ: 1:50	🟪 – חיפוי

הערות:
1. על המבצע לבדוק את התאמת התכנית בשטח, לפני הבנייה, ולבקר את המידות. על כל טעות ו/או אי התאמה יש לעדכן משרד מתכנן.
2. אין לקבוע מידות ע"פ שרטוט. המידות המחייבות הן המידות שנמדדו בשטח לאחר ביצוע.
3. המידות בתכנית הן ברוטו-ללא חיפוי גמר.
4. יתכנו שינויים בהתאם להוראות הביצוע הסופי.
5. כל התכניות נשארות רכוש המתכנן: אין לעשות בהן שימוש ללא אישור בכתב המתכנן.
6. כל ההערות תקפות אלא אם צוין אחרת.

מבט על

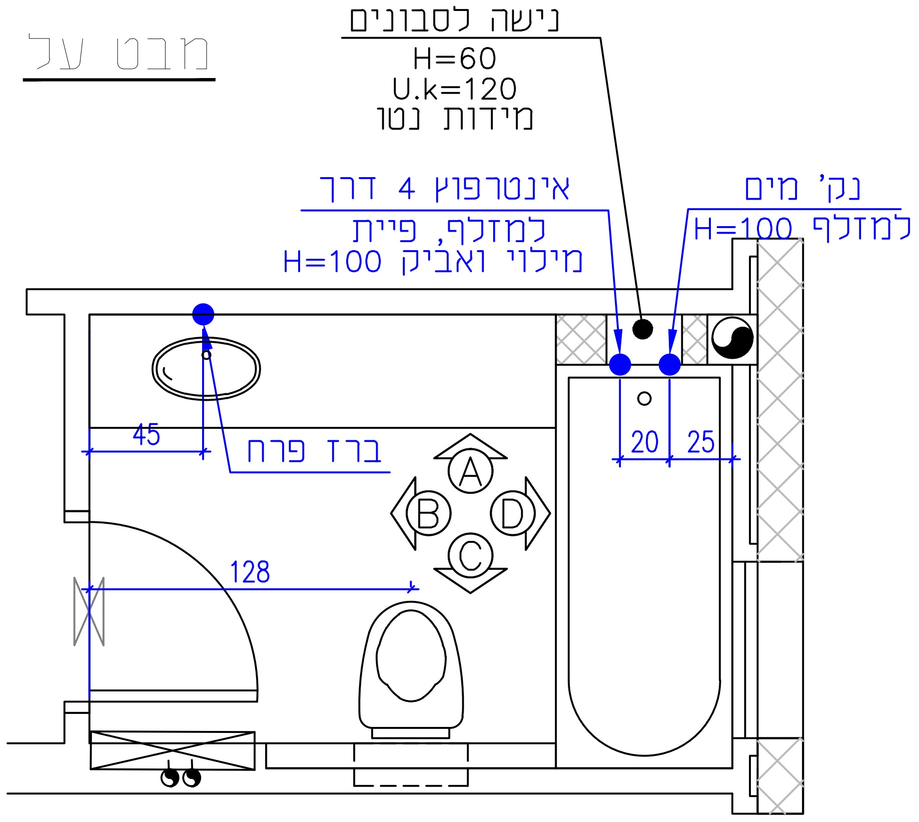

פריסה A

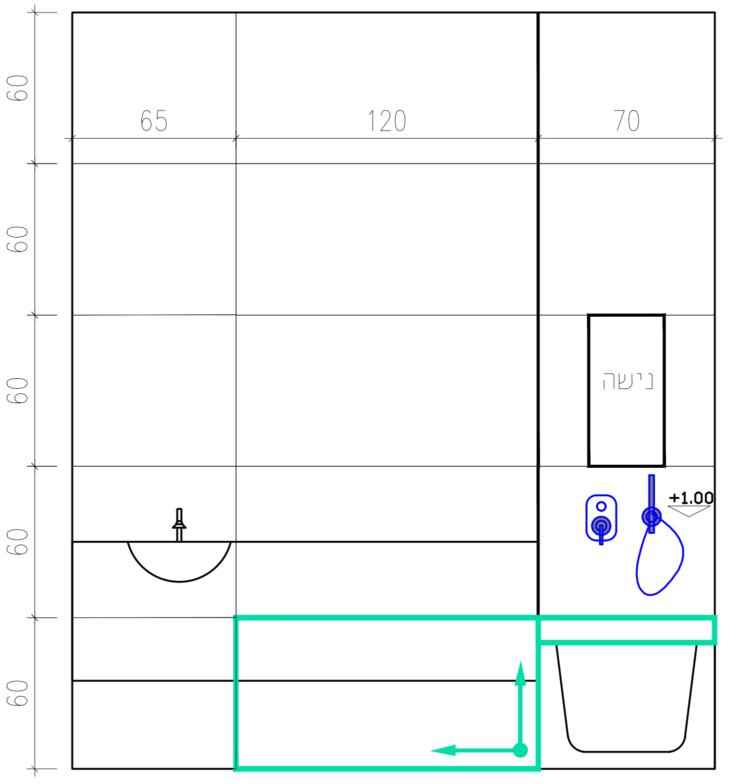

פריסה B

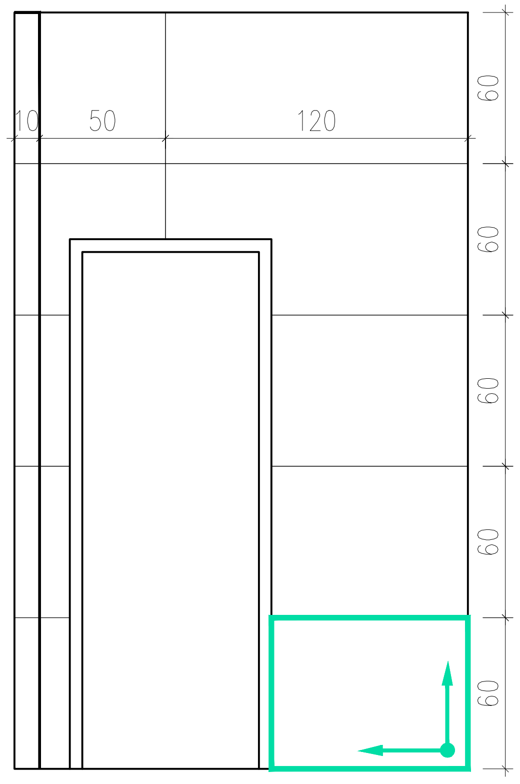

ח.רחצה כללי

ריצוף+חיפוי

אריח 60*120
דורטס גריי
מקט: 690204

ריצוף

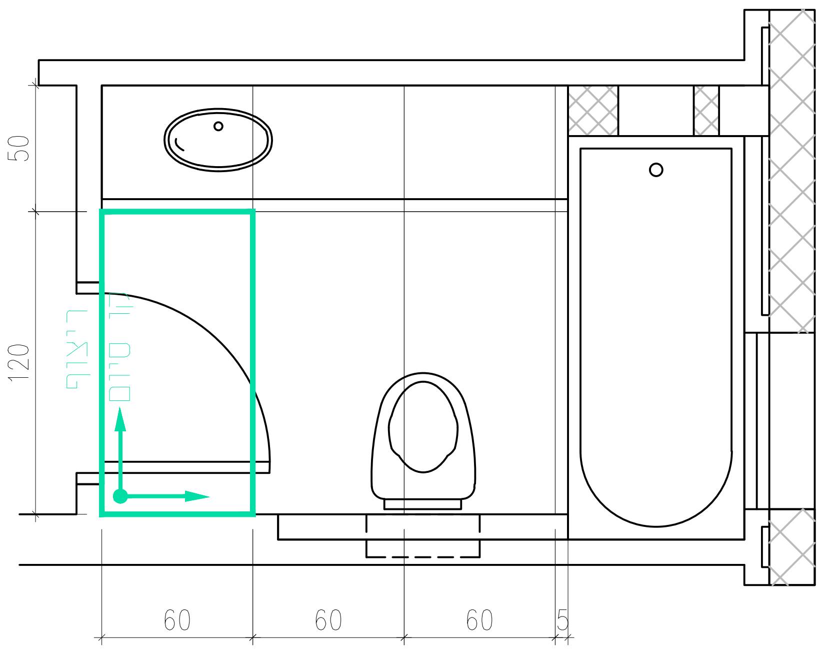

פריסה C

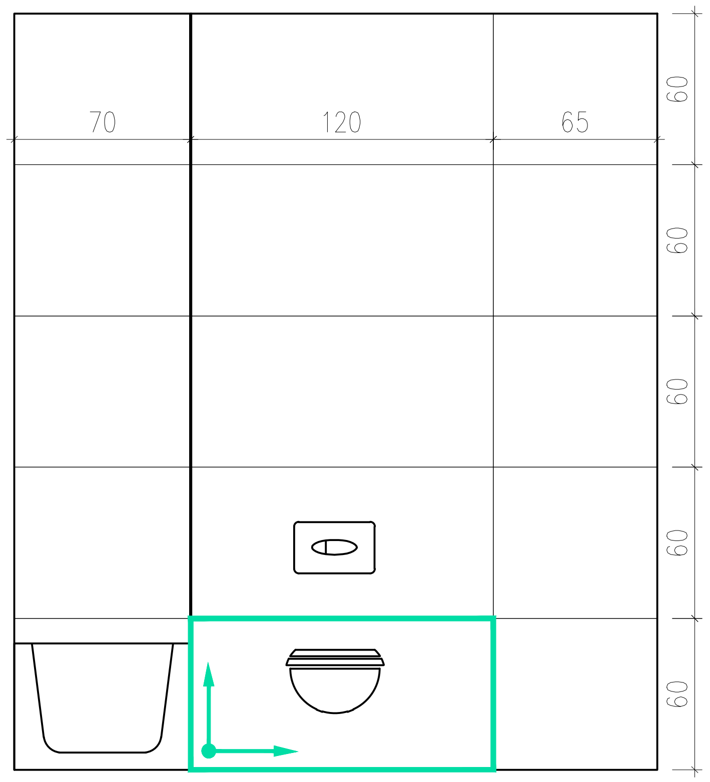

פריסה D

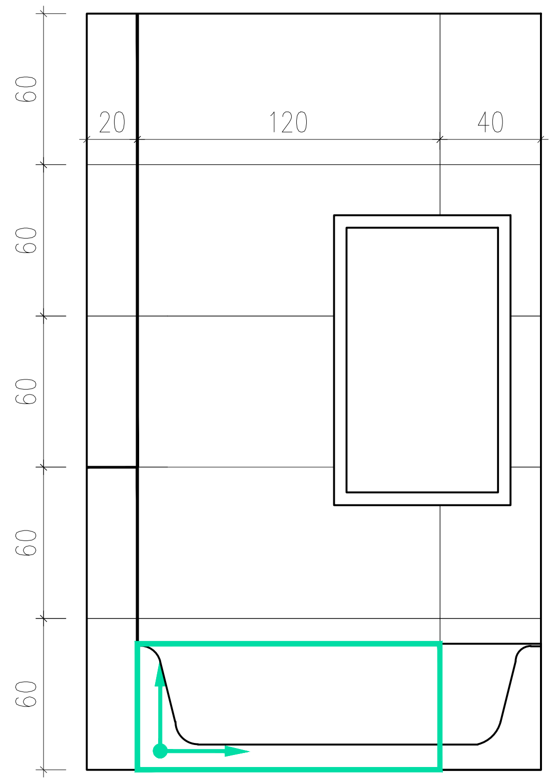

הערות:

1. על המבצע לבדוק את התאמת התכנית בשטח, לפני הבנייה, ולבקר את המידות. על כל טעות ו/או אי התאמה יש לעדכן משרד מתכנן.
2. אין לקבוע מידות ע"פ שרטוט. המידות המחייבות הן המידות שנמדדו בשטח לאחר ביצוע.
3. המידות בתכנית הן ברוטו-ללא חיפוי גמר.
4. יתכנו שינויים בהתאם להוראות הביצוע הסופי.
5. כל התכניות נשארות רכוש המתכנן: אין לעשות בהן שימוש ללא אישור בכתב המתכנן.
6. כל ההערות תקפות אלא אם צוין אחרת.

פרויקט:	תכנית:	גליון מס':	גודל גיליון:	
אלפי מנשה דירה 14	פריסות ח.רחצה כללי	14	A3	🟩 – ריצוף
	○ לעיון ● לאישור ○ למכרז ○ לביצוע	תאריך: 20.8.2026	קנ"מ: 1:50	🟪 – חיפוי

RK
RUTH KOLSKY

מבט על

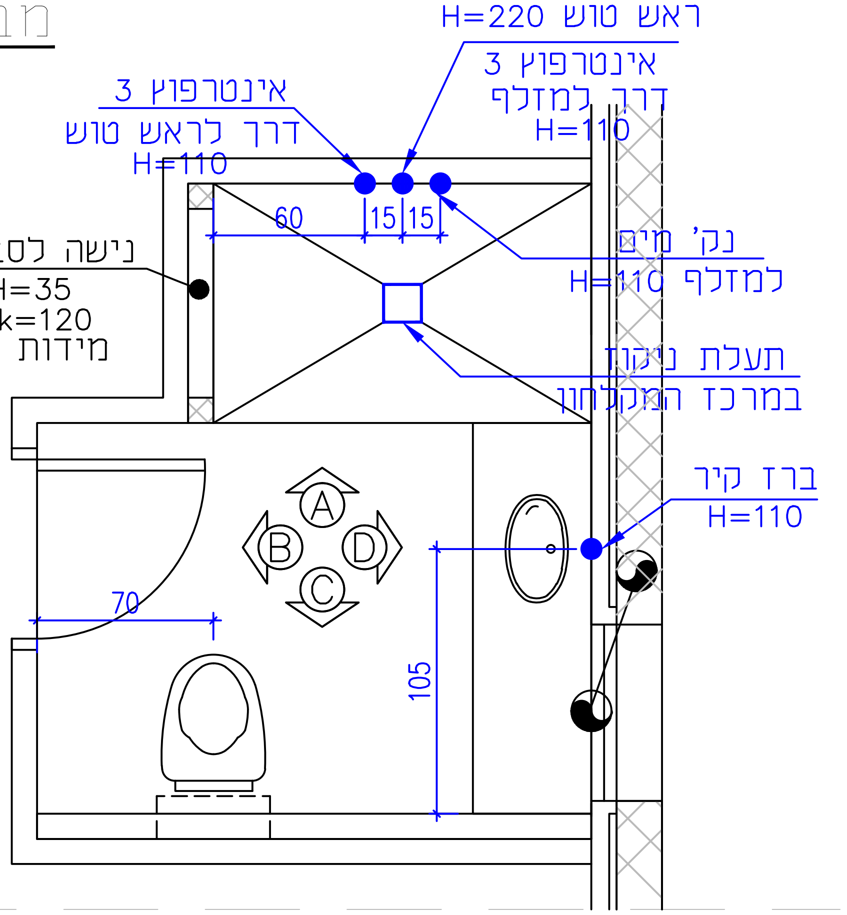

ריצוף

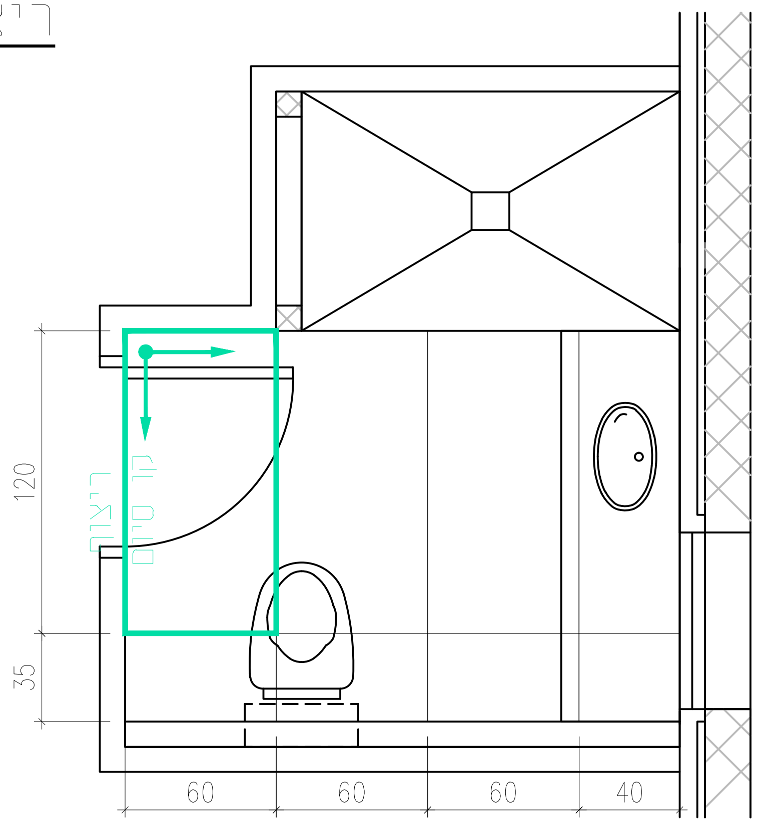

פריסה A

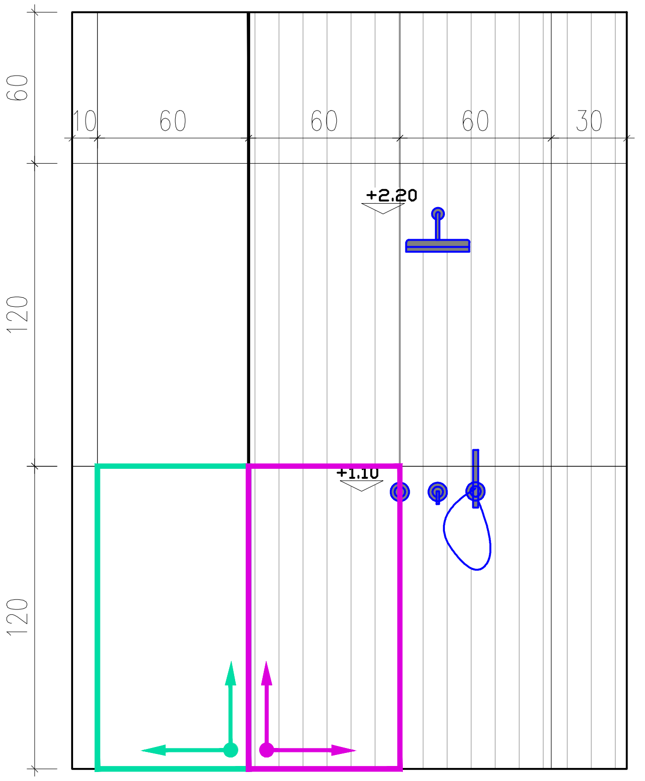

פריסה B

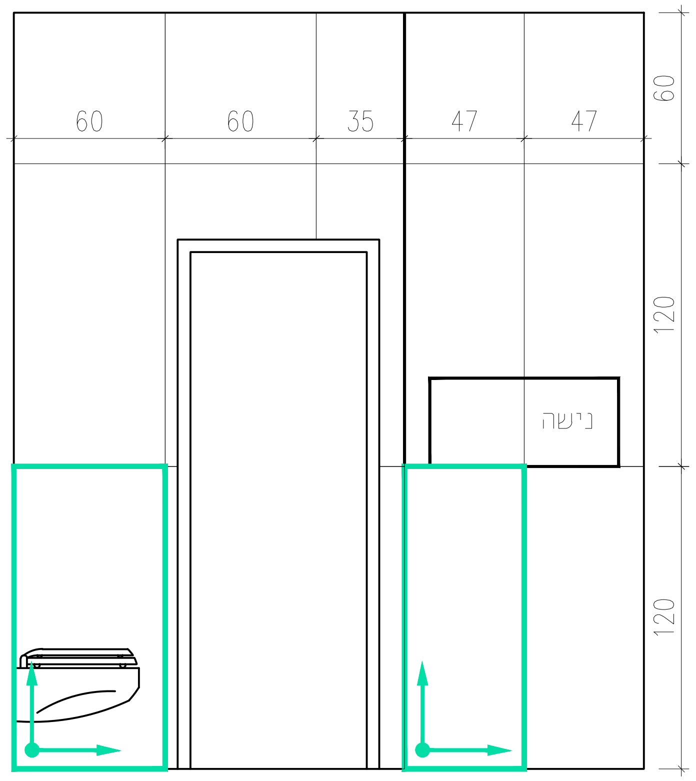

פריסה C

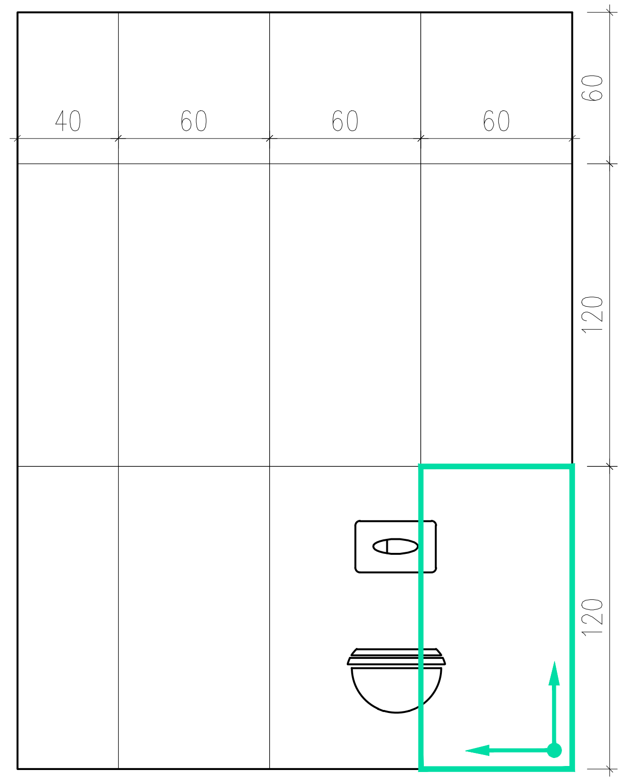

פריסה D

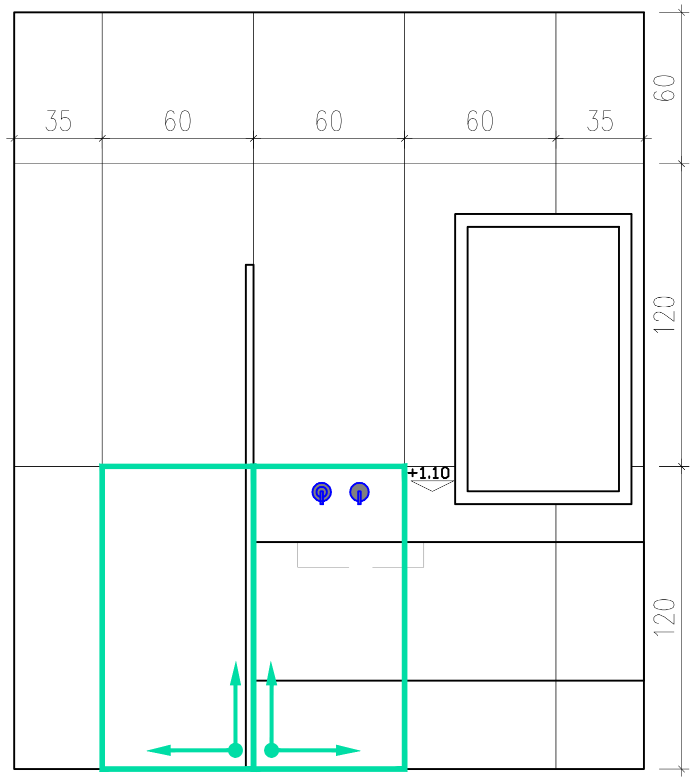

ח.רחצה הורים

ריצוף+חיפוי

אריח 60*120
דורסט גריס
מקט: 690204

דקור

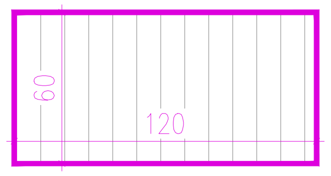

אריח 60*120
דקור רליב דורסט גריס
מקט: 690211

הערות:
1. על המבצע לבדוק את התאמת התכנית בשטח, לפני הבנייה, ולבקר את המידות. על כל טעות ו/או אי התאמה יש לעדכן משרד מתכנן.
2. אין לקבוע מידות ע"פ שרטוט. המידות המחייבות הן המידות שנמדדו בשטח לאחר ביצוע.
3. המידות בתכנית הן ברוטו-ללא חיפוי גמר.
4. יתכנו שינויים בהתאם להוראות הביצוע הסופי.
5. כל התכניות נשארות רכוש המתכנן: אין לעשות בהן שימוש ללא אישור בכתב המתכנן.
6. כל ההערות תקפות אלא אם צוין אחרת.

פרויקט: אלפי מנשה דירה 14	תכנית: פריסות ח.רחצה הורים	גליון מס': 15	גודל גיליון: A3	🟩 – ריצוף	
	○ לעיון ● לאישור ○ למכרז ○ לביצוע	תאריך: 20.8.2026	קנ"מ: 1:50	🟪 – חיפוי	

מבט על

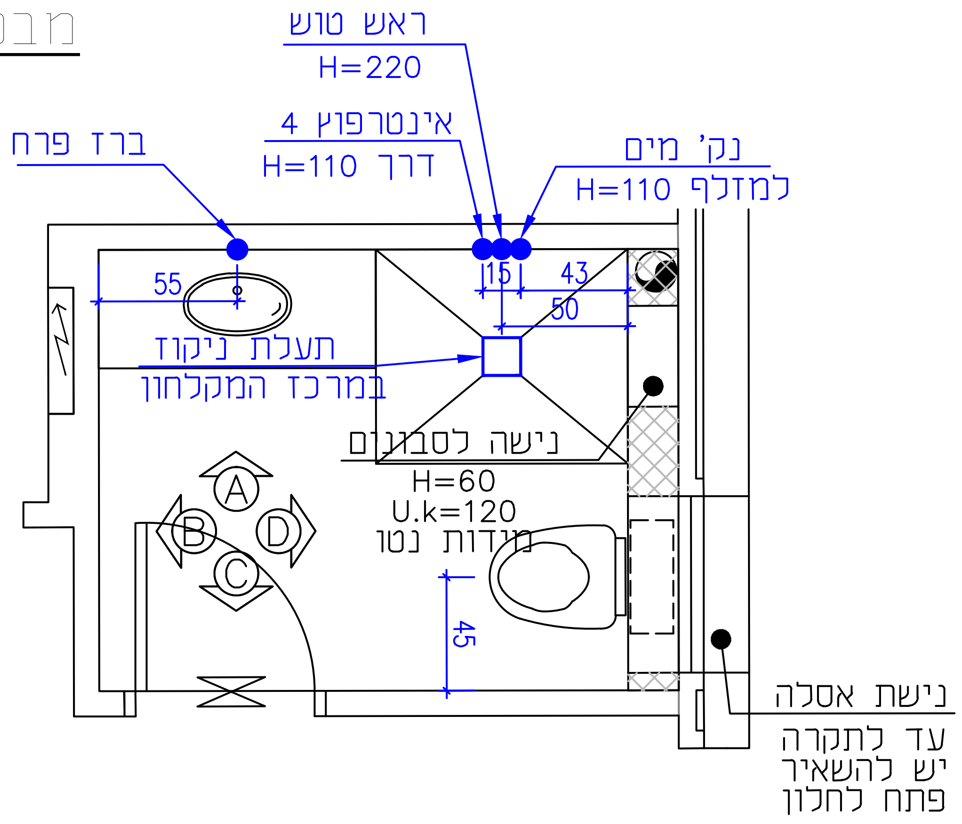

ריצוף

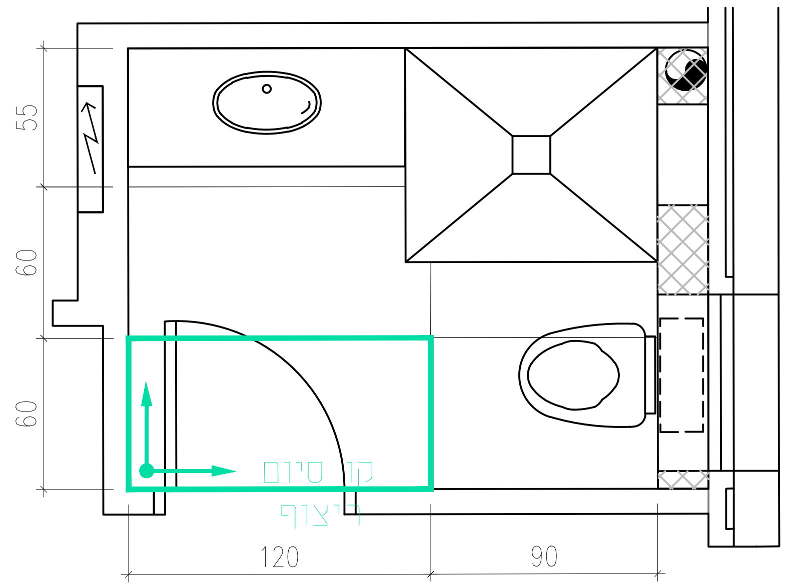

פריסה A

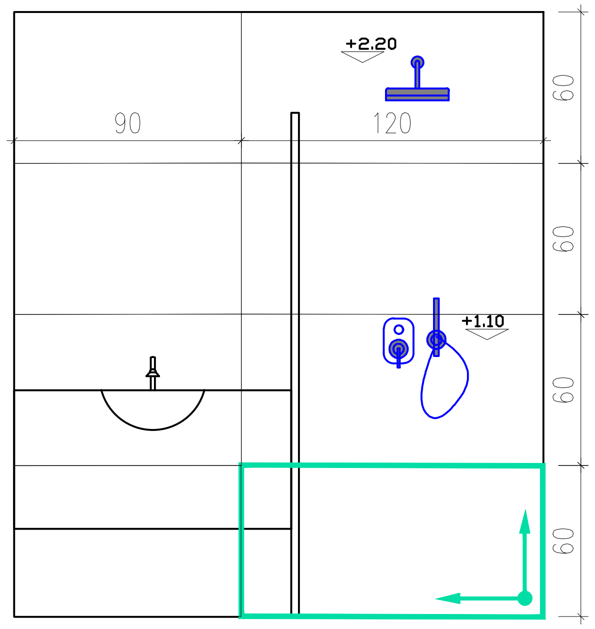

פריסה B

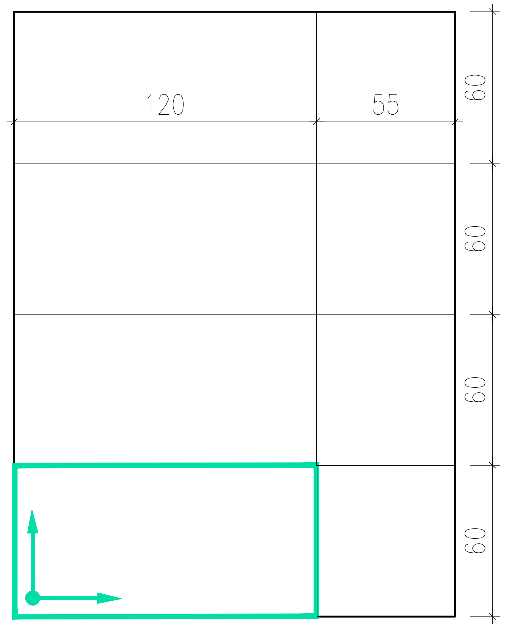

פריסה C

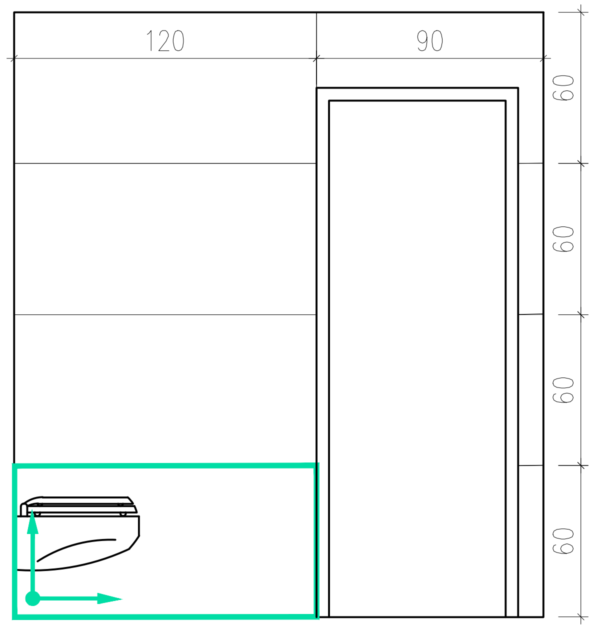

פריסה D

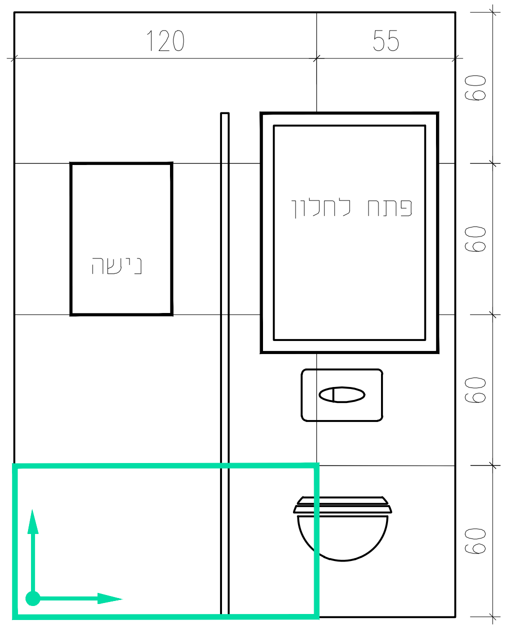

ח.רחצה אורחים-גג

ריצוף+חיפוי

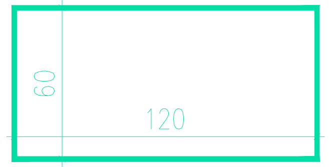

אריח 60*120
נין, ויסטה גריי מט
מקט: 199061

RK
RUTH KOLSKY

הערות:
1. על המבצע לבדוק את התאמת התכנית בשטח, לפני הבנייה, ולבקר את המידות. על כל טעות ו/או אי התאמה יש לעדכן משרד מתכנן.
2. אין לקבוע מידות ע"פ שרטוט. המידות המחייבות הן המידות שנמדדו בשטח לאחר ביצוע.
3. המידות בתכנית הן ברוטו-ללא חיפוי גמר.
4. יתכנו שינויים בהתאם להוראות הביצוע הסופי.
5. כל התכניות נשארות רכוש המתכנן: אין לעשות בהן שימוש ללא אישור בכתב המתכנן.
6. כל ההערות תקפות אלא אם צוין אחרת.

ריצוף – 🟩
חיפוי – 🟪

גודל גיליון: A3
קנ"מ: 1:50
גליון מס': 16
תאריך: 20.8.2026
תכנית: פריסות ח.רחצה אורחים-גג
○ לעיון ● לאישור
○ למכרז ○ לביצוע
פרויקט: אלפי מנשה
דירה 14