
* מידות סופיות ילקחו מהשטח ע"י הנגר
* גוף הארון–סנדוויץ'
* גמר חזיתות–פורניר
* גוונים יבחרו ע"י המעצבת מול הנגר

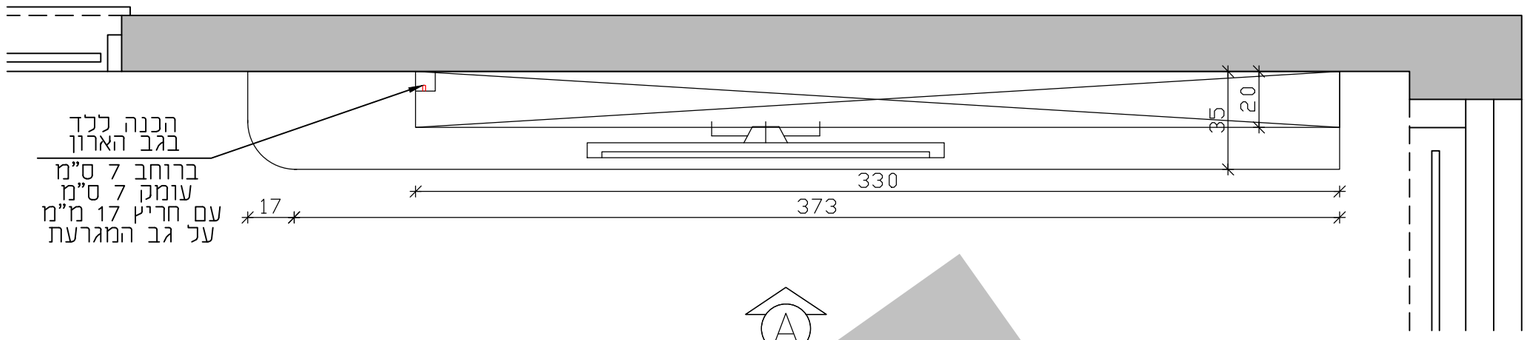


מבט על

A

הדמיה



מבט A

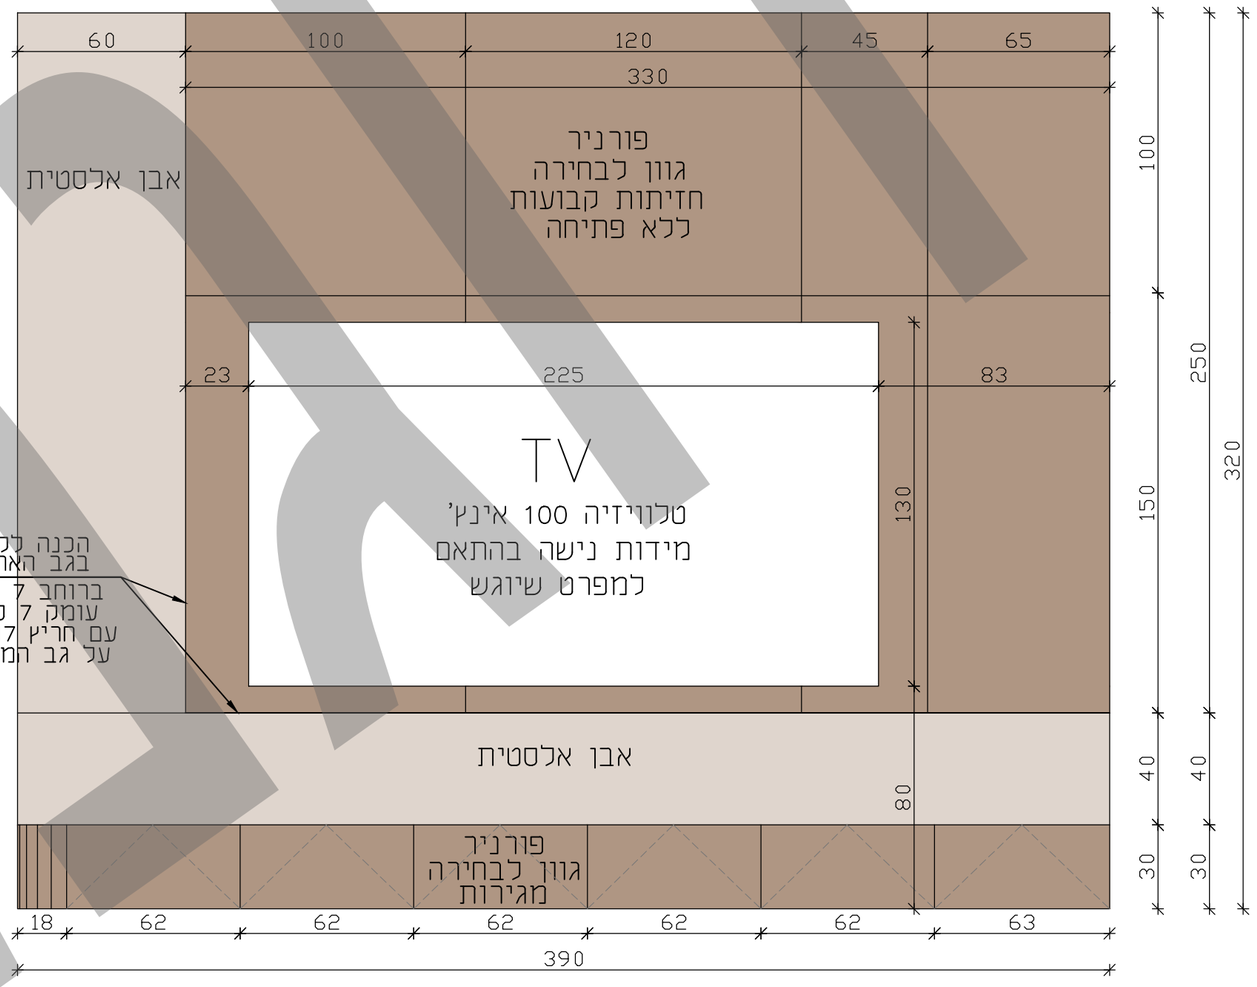

לקוח: טלי והרנן גומלסקי	כתובת: שקנאי 12 צורן	תכנית: נגרות TV
חתימת לקוח לאישור תכנית: _____	● לעיון ○ לאישור ○ למכרז ○ לביצוע	גיליון מס': 5 / גודל גיליון: --
		תאריך: 7.10.26 / קנ"מ: 1:20


הערות:

1. על המבצע לבדוק את התאמת התכנית בשטח, לפני הבנייה, ולבקר את המידות. על כל טעות ו/או אי התאמה יש לעדכן משרד מתכנן.
2. אין לקבוע מידות ע"פ שרטוט. המידות המחייבות הן המידות שנמדדו בשטח לאחר ביצוע.
3. המידות בתכנית הן ברוטו–ללא חיפוי גמר.
4. יתכנו שינויים בהתאם להוראות הביצוע הסופי.
5. כל התכניות נשארות רכוש המתכנן: אין לעשות בהן שימוש ללא אישור בכתב המתכנן.
6. כל ההערות תקפות אלא אם צוין אחרת.


RK
RUTH KOLSKY
תכנון - עיצוב - השראה

* מידות סופיות ילקחו מהשטח ע"י הנגר
* גוף הארון–סנדוויץ'
* גמר חזיתות–צבע בתנור
* גוונים יבחרו ע"י המעצבת מול הנגר
* ידיות חיצוניות
* מדפים פנימיים ניידים


מבט על

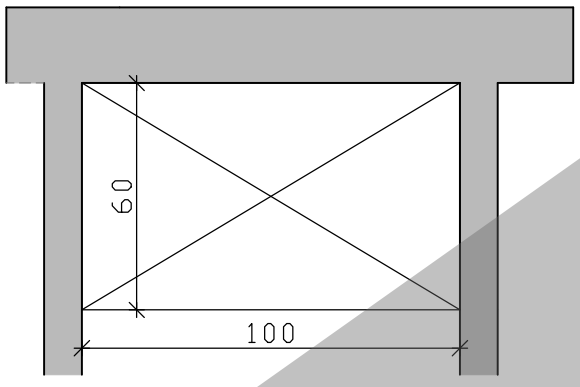

מבט A – חלוקה פנימית

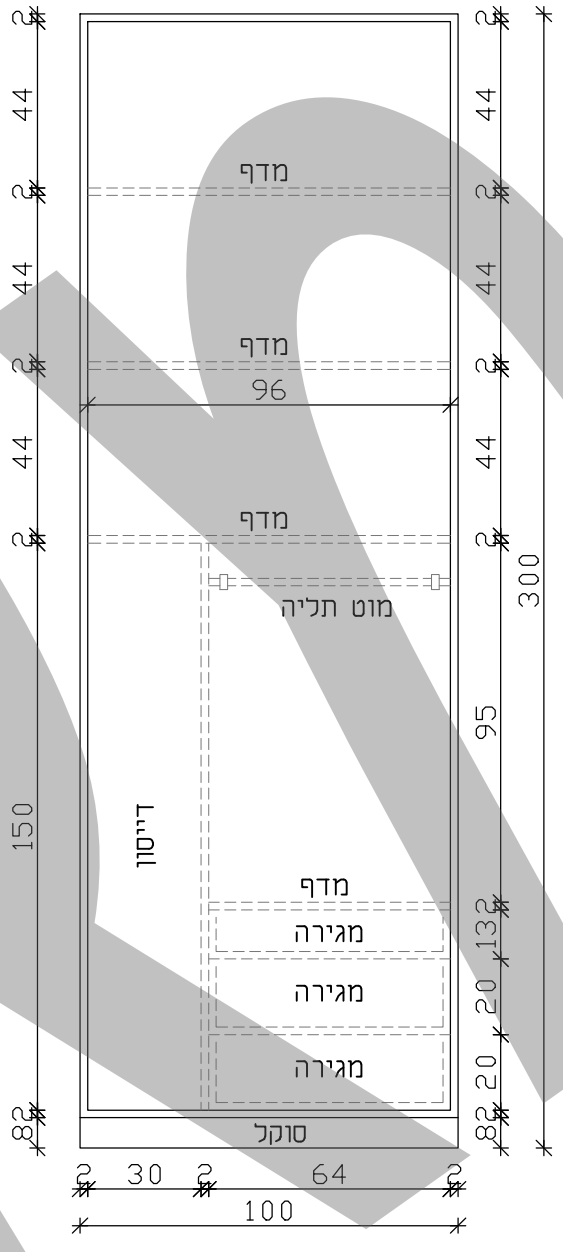

מבט A – חזית

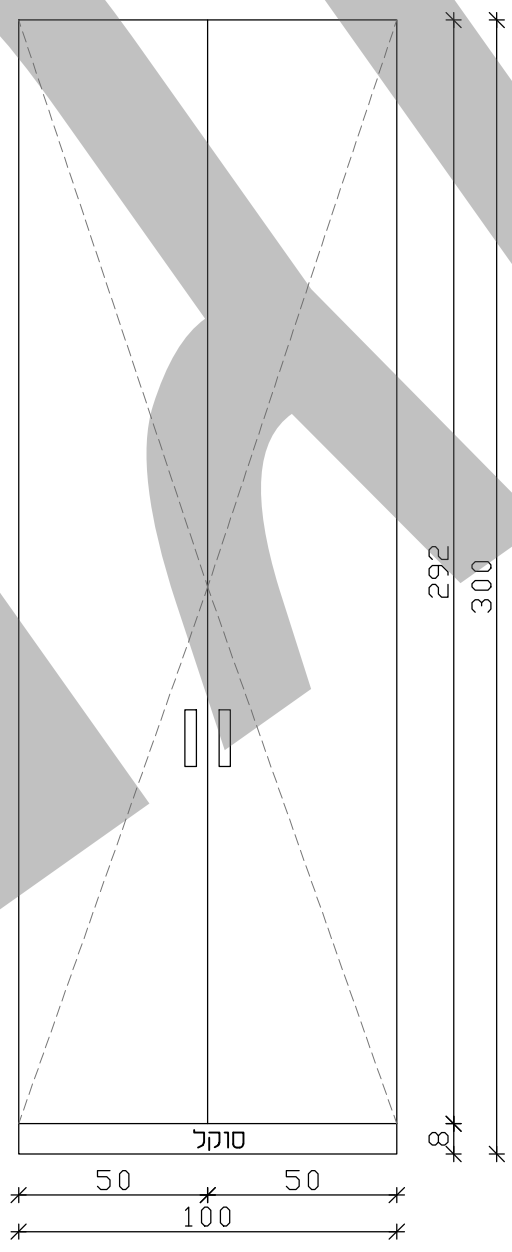


RK
RUTH KOLSKY
תכנון - עיצוב - השראה

לקוח: טלי והרנן גומלסקי	כתובת: שקנאי 12 צורן	תכנית: נגרות דיסון
חתימת לקוח לאישור תכנית: _____	● לעיון ○ לאישור ○ למכרז ○ לביצוע	גיליון מס': 18 / גודל גיליון: A3 / תאריך: 7.10.26 / קנ"מ: 1:20

* מידות סופיות ילקחו מהשטח ע"י הנגר
* גוף הארון–סנדוויץ'
* גמר חזיתות–צבע בתנור
* מידוף–פורניר
* גוונים יבחרו ע"י המעצבת מול הנגר
* ללא סגירה בצדדים– חזית עולה על המסגרת
* פתיחת טאצ'




הדמיה

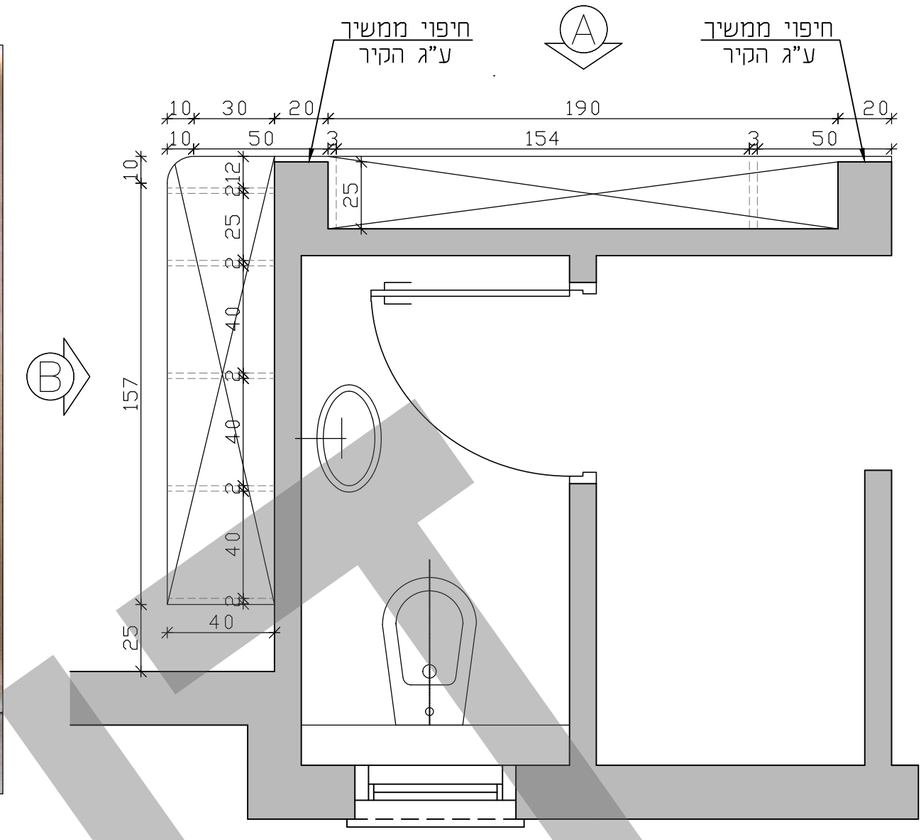


מבט על


מבט A

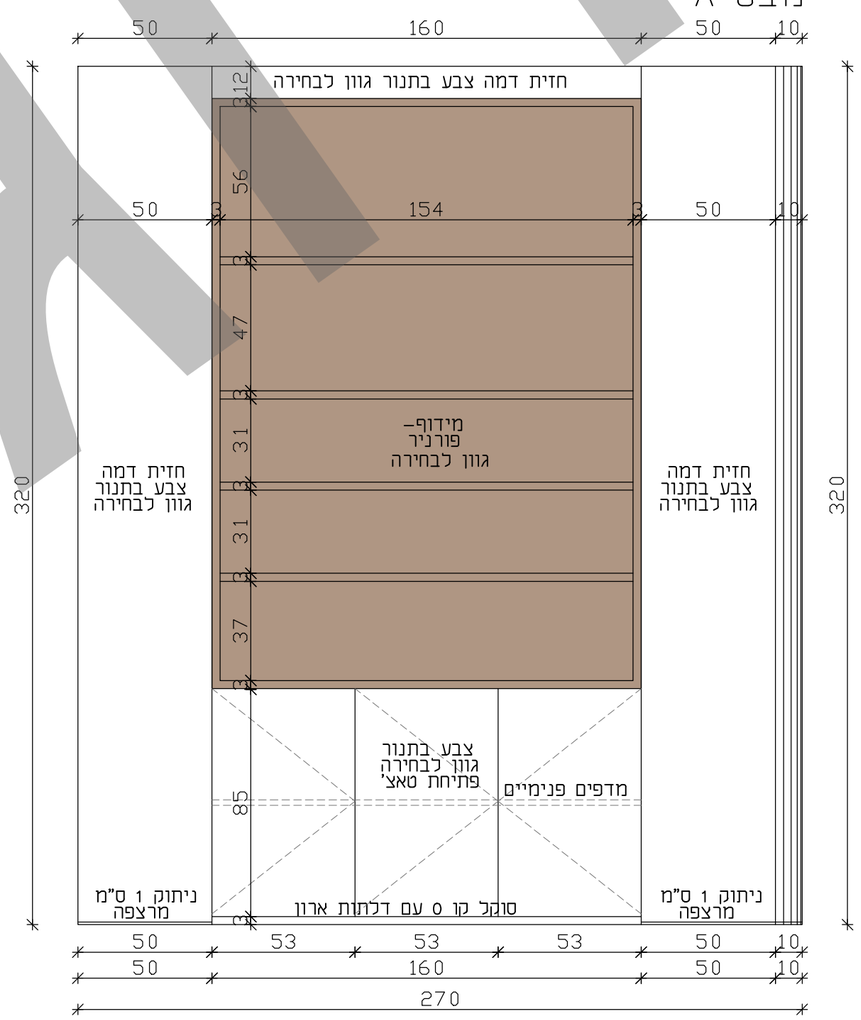

מבט B – חזית

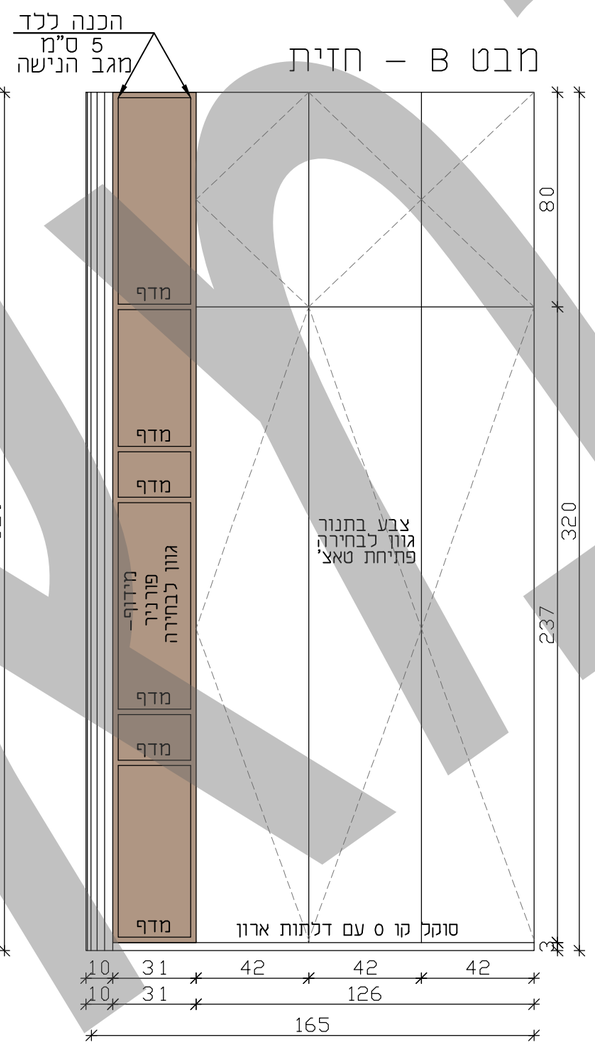

מבט B – חלוקה פנימית

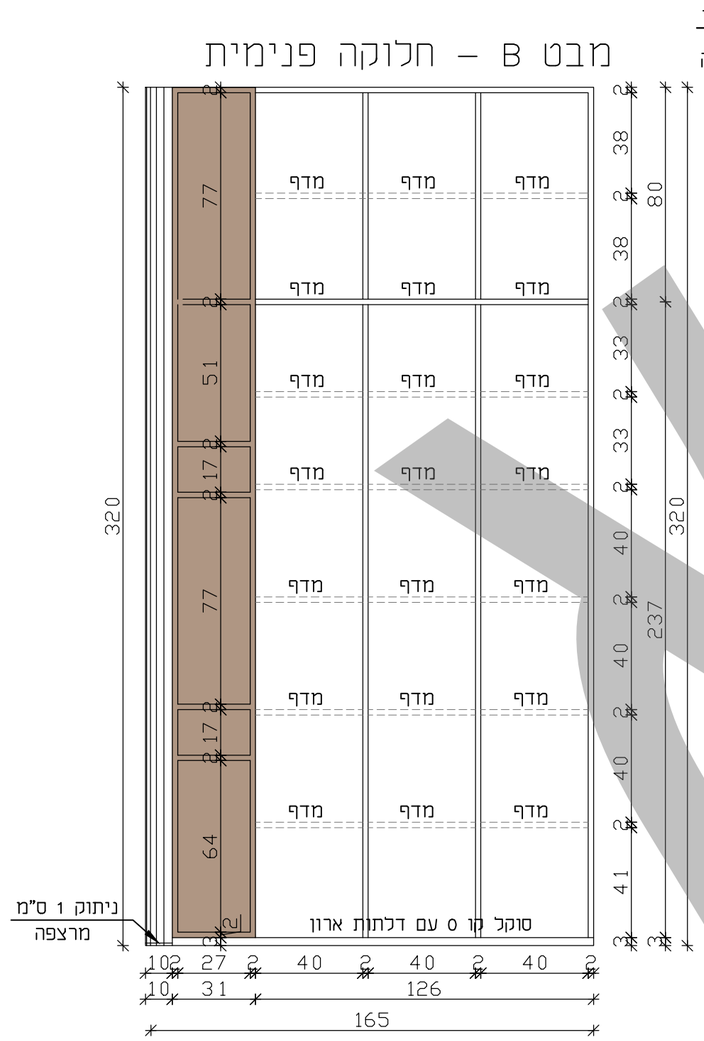


הערות:

1. על המבצע לבדוק את התאמת התכנית בשטח, לפני הבנייה, ולבקר את המידות. על כל טעות ו/או אי התאמה יש לעדכן משרד מתכנן.
2. אין לקבוע מידות ע"פ שרטוט. המידות המחייבות הן המידות שנמדדו בשטח לאחר ביצוע.
3. המידות בתכנית הן ברוטו–ללא חיפוי גמר.
4. יתכנו שינויים בהתאם להוראות הביצוע הסופי.
5. כל התכניות נשארות רכוש המתכנן: אין לעשות בהן שימוש ללא אישור בכתב המתכנן.
6. כל ההערות תקפות אלא אם צוין אחרת.

RK
RUTH KOLSKY
תכנון - עיצוב - השראה


לקוח: טלי והרנן גומלסקי	כתובת: שקנאי 12 צורן	תכנית: נגרות פ.אוכל ומטבח
חתימת לקוח לאישור תכנית: _____	● לעיון ○ לאישור ○ למכרז ○ לביצוע	גיליון מס': 5 / גודל גיליון: -- / תאריך: 7.10.26 / קנ"מ: 1:20

* מידות סופיות ילקחו מהשטח ע"י הנגר
* גוף הארון–סנדוויץ'
* גמר חזיתות–צבע בתנור
* מידוף ושולחן עבודה–פורניר
* גוונים יבחרו ע"י המעצבת מול הנגר
* ידיות אינטגרליות/פתיחת טאצ'

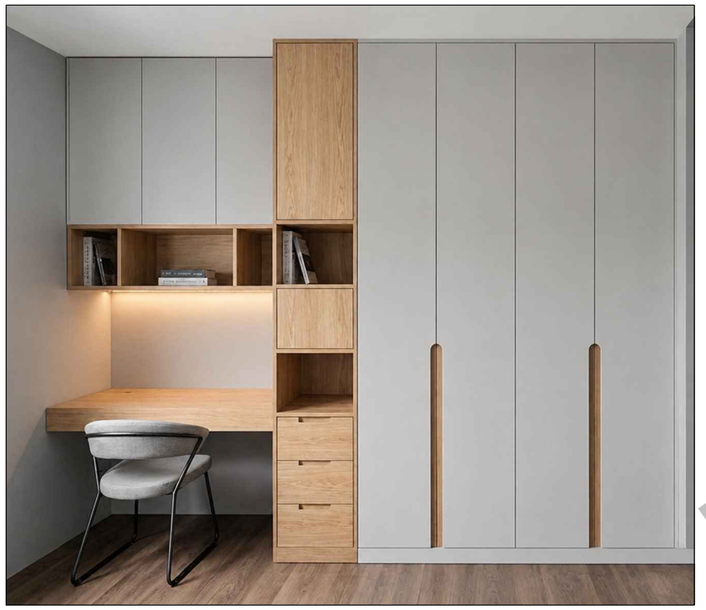


הדמיה


מבט על

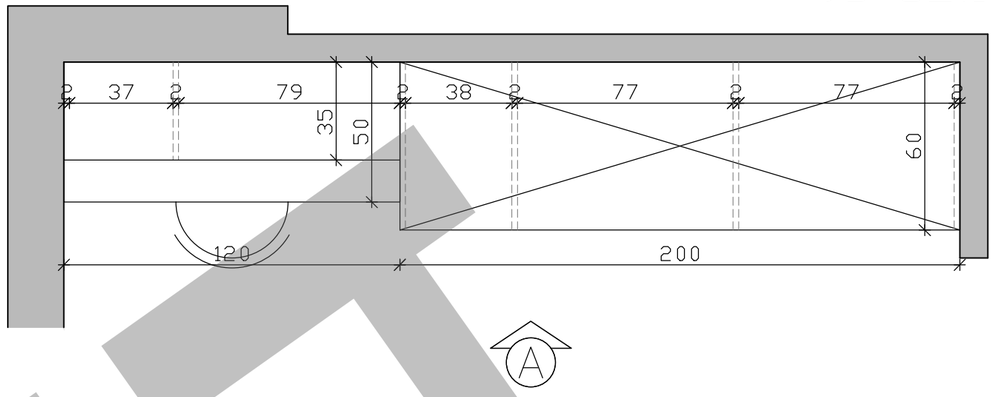

מבט A – חזית

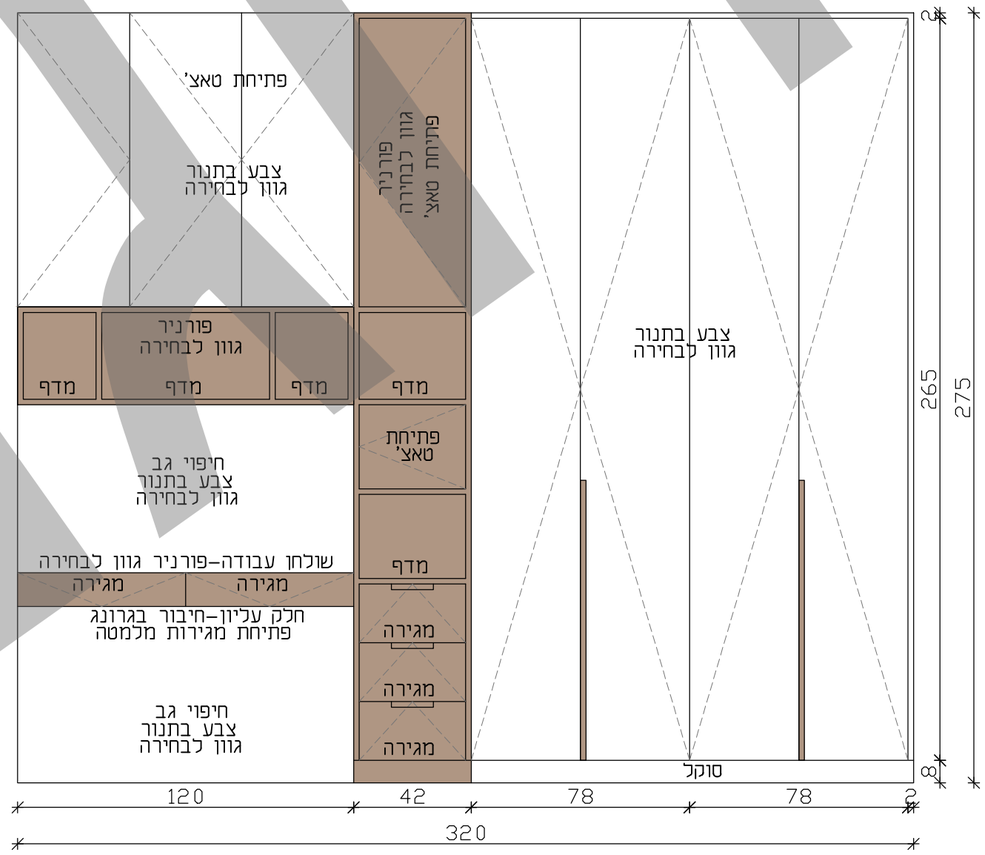

מבט A – חלוקה פנימית

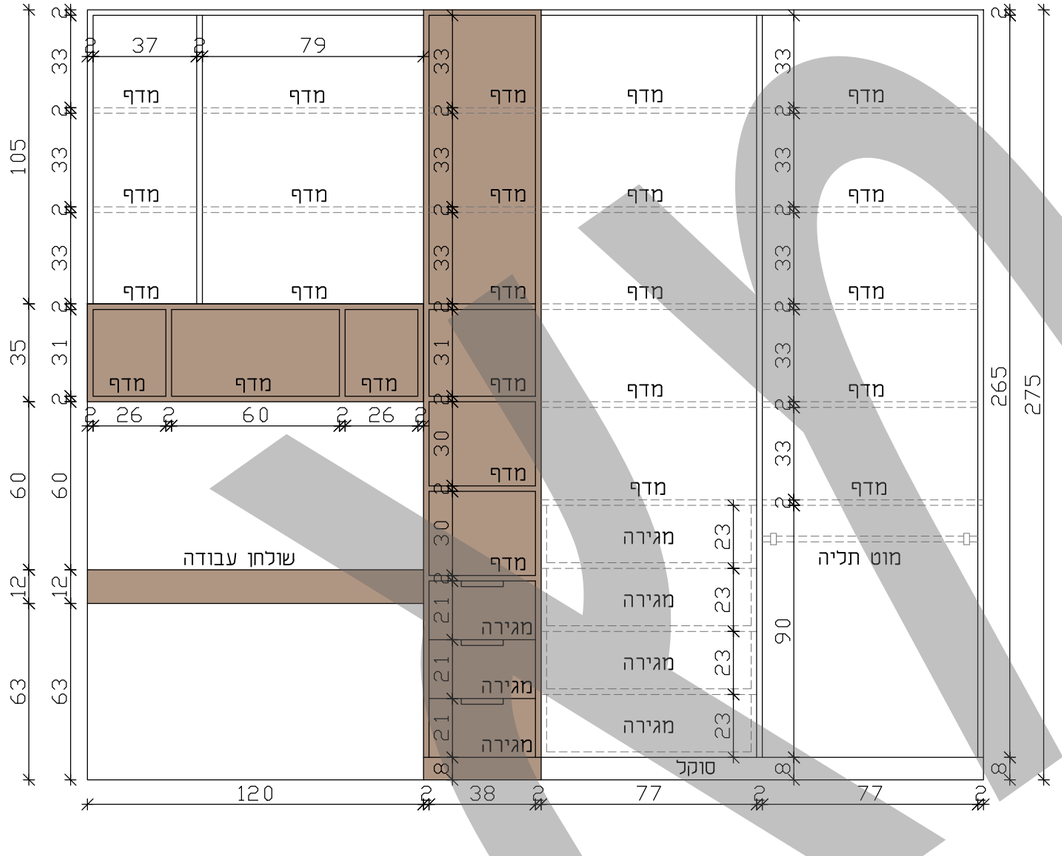


הערות:


1. על המבצע לבדוק את התאמת התכנית בשטח, לפני הבנייה, ולבקר את המידות. על כל טעות ו/או אי התאמה יש לעדכן משרד מתכנן.
2. אין לקבוע מידות ע"פ שרטוט. המידות המחייבות הן המידות שנמדדו בשטח לאחר ביצוע.
3. המידות בתכנית הן ברוטו–ללא חיפוי גמר.
4. יתכנו שינויים בהתאם להוראות הביצוע הסופי.
5. כל התכניות נשארות רכוש המתכנן: אין לעשות בהן שימוש ללא אישור בכתב המתכנן.
6. כל ההערות תקפות אלא אם צוין אחרת.


RK
RUTH KOLSKY
תכנון - עיצוב - השראה

לקוח: טלי והרנן גומלסקי	כתובת: שקנאי 12 צורן	תכנית: נגרות חדר איתן
חתימת לקוח לאישור תכנית: _____	● לעיון ○ לאישור ○ למכרז ○ לביצוע	גיליון מס': 5 / גודל גיליון: -- / תאריך: 7.10.26 / קנ"מ: 1:20

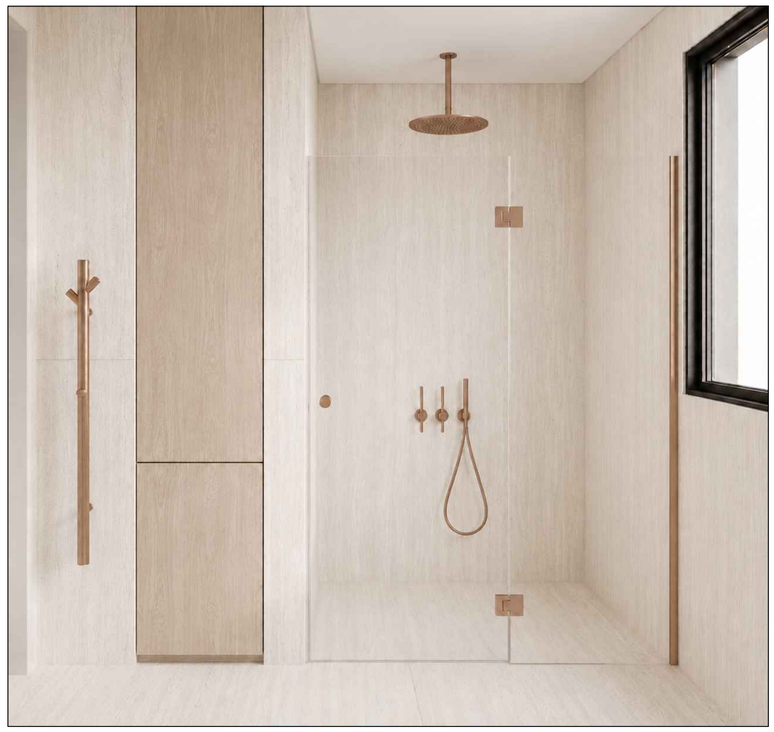



הדמיה

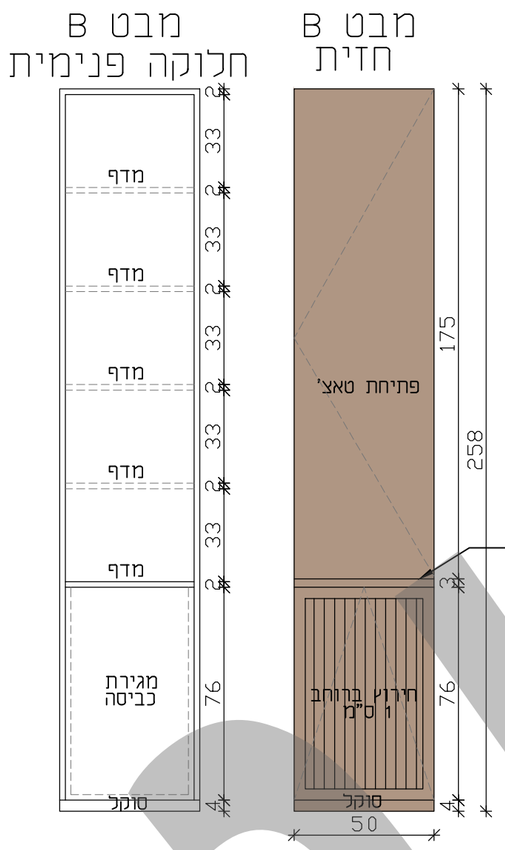

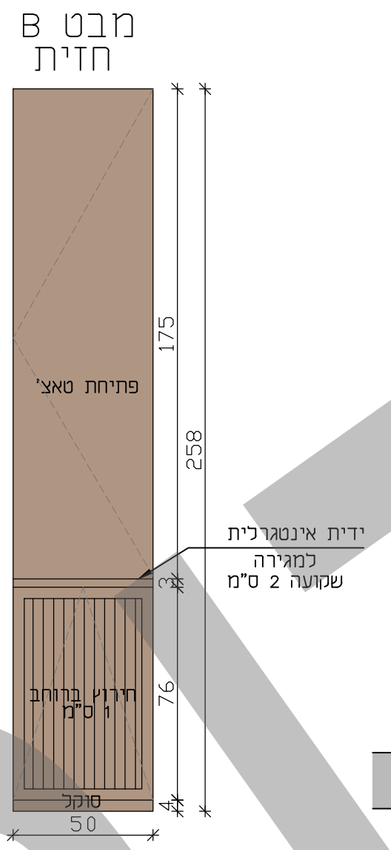

ידית אינטגרלית
למגירה
שקועה 2 ס"מ

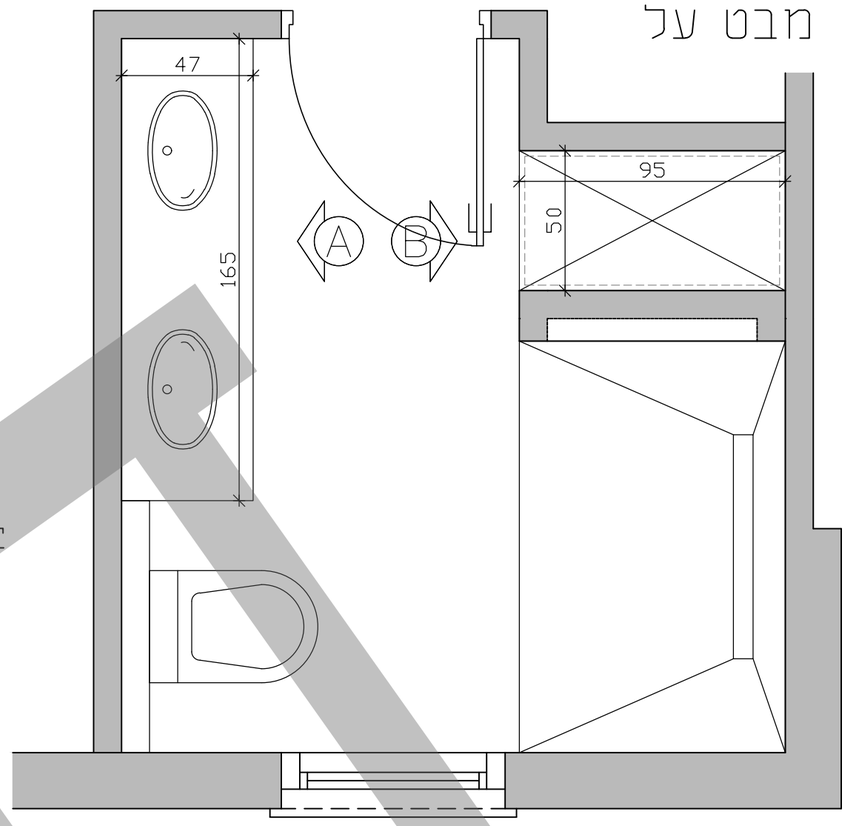


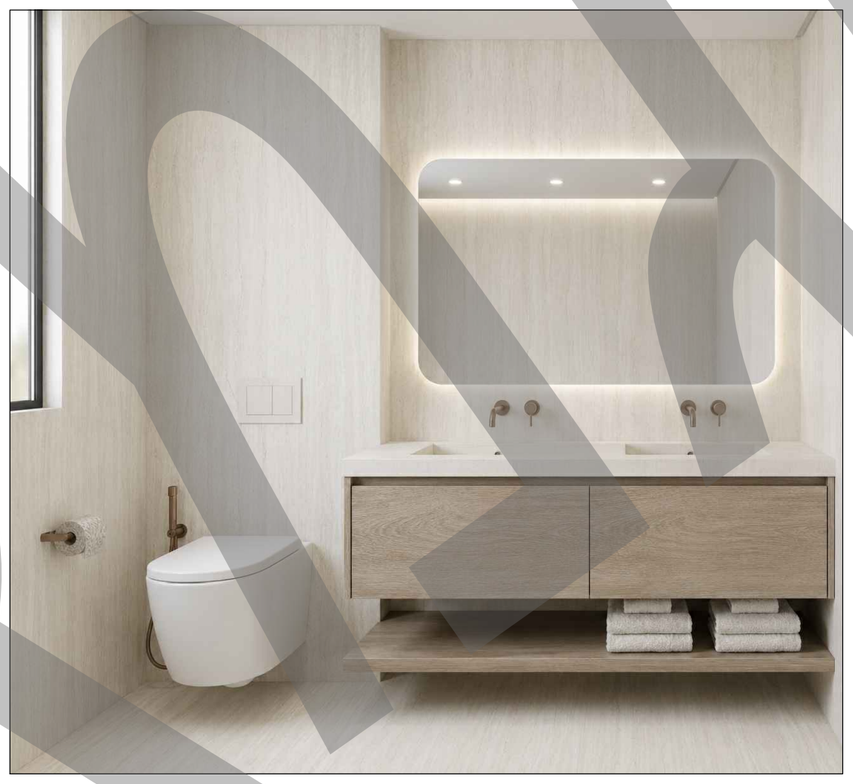

הדמיה

- מידות סופיות ילקחו מהשטח ע"י הנגר
- גוף הארון–סנדוויץ'
- גמר חזיתות–פורניר
- כיור בנוי מאריח פורצלן
- גוונים יבחרו ע"י המעצבת מול הנגר
- ידיות אינטגרליות/פתיחת טאצ'
- מדפים פנימיים ניידים

מבט A

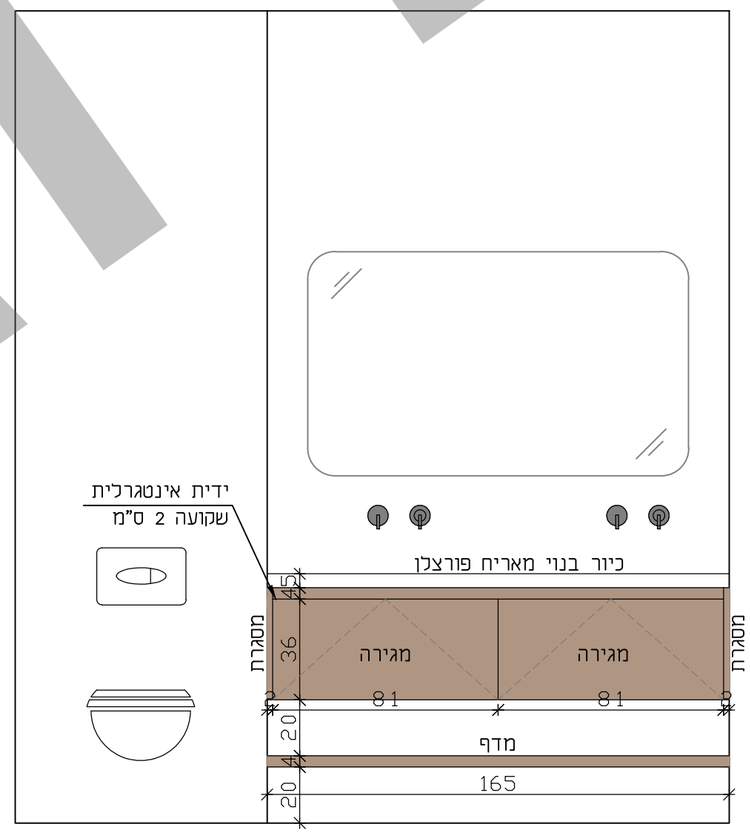

הערות:


1. על המבצע לבדוק את התאמת התכנית בשטח, לפני הבנייה, ולבקר את המידות. על כל טעות ו/או אי התאמה יש לעדכן משרד מתכנן.
2. אין לקבוע מידות ע"פ שרטוט. המידות המחייבות הן המידות שנמדדו בשטח לאחר ביצוע.
3. המידות בתכנית הן ברוטו–ללא חיפוי גמר.
4. יתכנו שינויים בהתאם להוראות הביצוע הסופי.
5. כל התכניות נשארות רכוש המתכנן: אין לעשות בהן שימוש ללא אישור בכתב המתכנן.
6. כל ההערות תקפות אלא אם צוין אחרת.

לקוח: טלי והרנן גומלסקי	כתובת: שקנאי 12 צורן	תכנית: נגרות ארונות רחצה–הורים
חתימת לקוח לאישור תכנית: _____	● לעיון ○ לאישור ○ למכרז ○ לביצוע	גיליון מס': 5 / גודל גיליון: --
		תאריך: 7.10.26 / קנ"מ: 1:20

RK
RUTH KOLSKY
תכנון - עיצוב - השראה

* מידות סופיות ילקחו מהשטח ע"י הנגר
* גוף הארון–סנדוויץ'
* גמר חזיתות–פורניר מחורץ ברוחב 0.5 ס"מ
* כיור בנוי מאריח פורצלן
* גוונים יבחרו ע"י המעצבת מול הנגר
* ידית אינטגרלית


מבט על

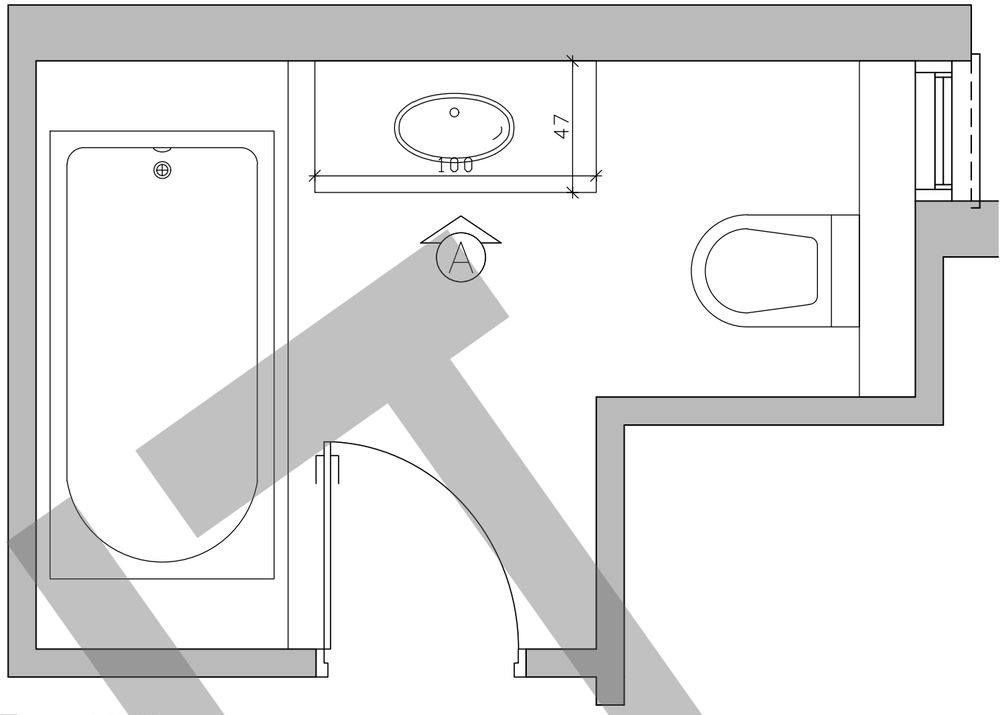

הדמיה



מבט A

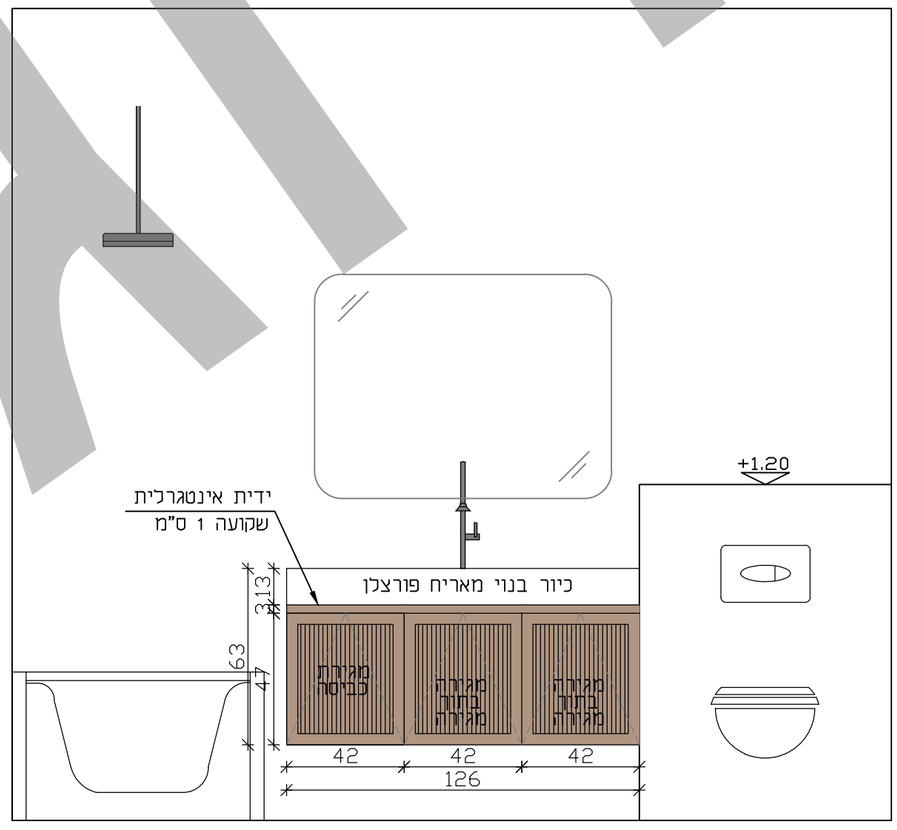


לקוח: טלי והרנן גומלסקי	כתובת: שקנאי 12 צורן	תכנית: נגרות ארון רחצה–ילדים
חתימת לקוח לאישור תכנית: _____	● לעיון ○ לאישור ○ למכרז ○ לביצוע	גיליון מס': 5 / גודל גיליון: -- / תאריך: 7.10.26 / קנ"מ: 1:20

הערות:

1. על המבצע לבדוק את התאמת התכנית בשטח, לפני הבנייה, ולבקר את המידות. על כל טעות ו/או אי התאמה יש לעדכן משרד מתכנן.
2. אין לקבוע מידות ע"פ שרטוט. המידות המחייבות הן המידות שנמדדו בשטח לאחר ביצוע.
3. המידות בתכנית הן ברוטו–ללא חיפוי גמר.
4. יתכנו שינויים בהתאם להוראות הביצוע הסופי.
5. כל התכניות נשארות רכוש המתכנן: אין לעשות בהן שימוש ללא אישור בכתב המתכנן.
6. כל ההערות תקפות אלא אם צוין אחרת.


RK
RUTH KOLSKY
תכנון - עיצוב - השראה


מבט על

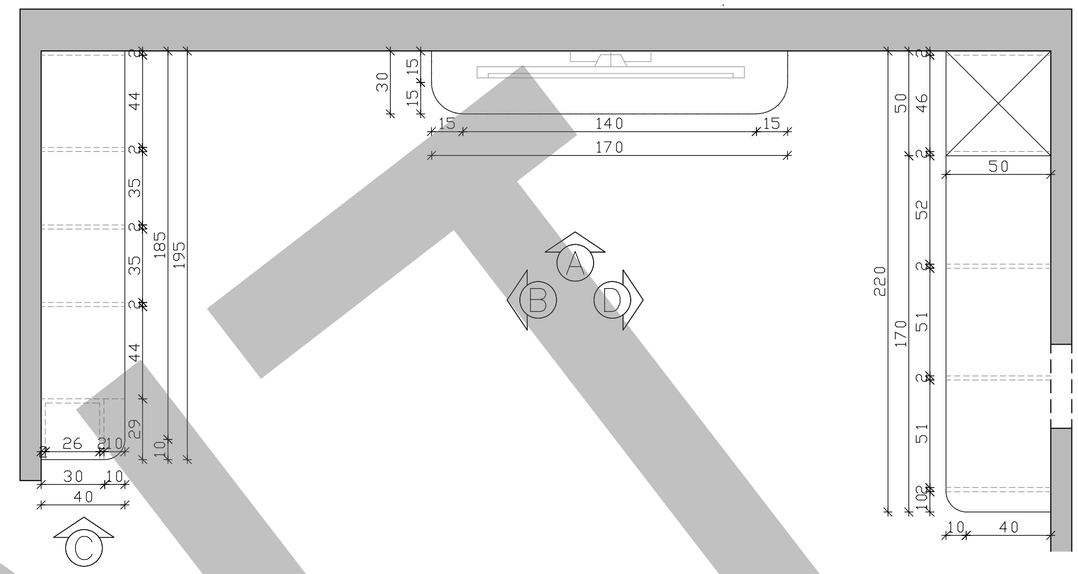


* מידות סופיות ילקחו מהשטח ע"י הנגר
* גוף הארון–סנדוויץ'
* גמר חזיתות–צבע בתנור/פורניר
* גוונים יבחרו ע"י המעצבת מול הנגר
* ידיות אינטגרליות
* מדפים ניידים

הדמיות

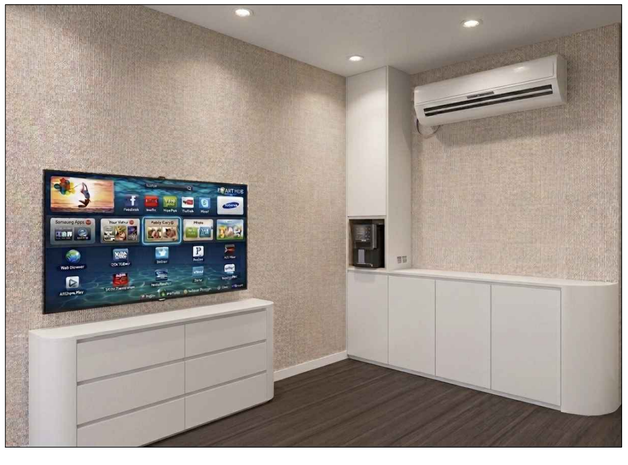


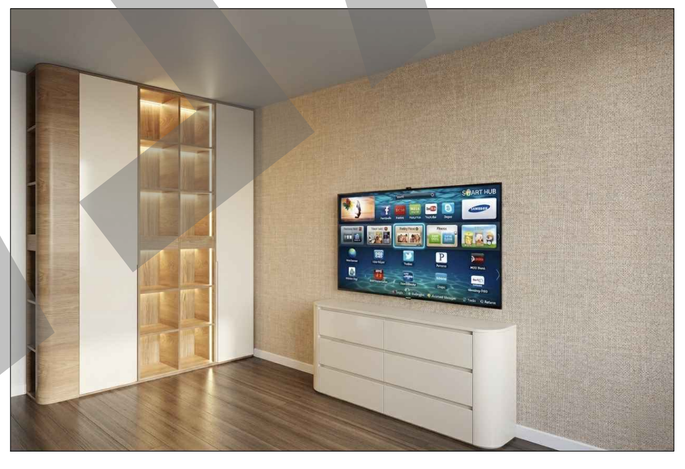


מבט A

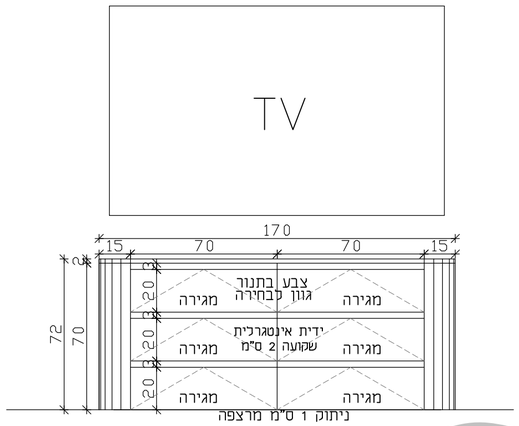


מבט B

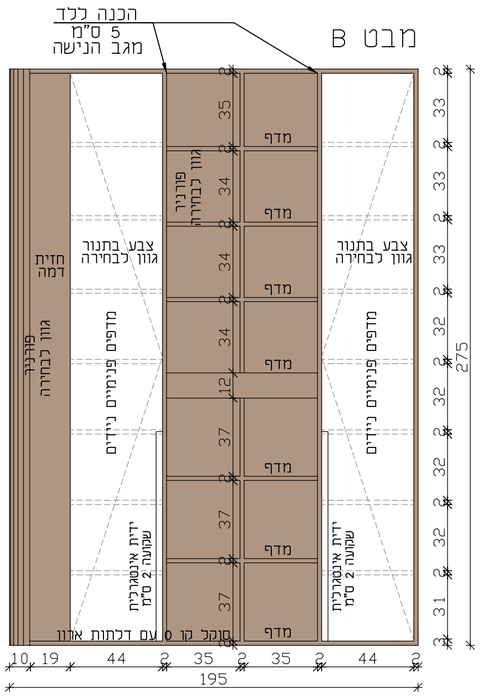


מבט C

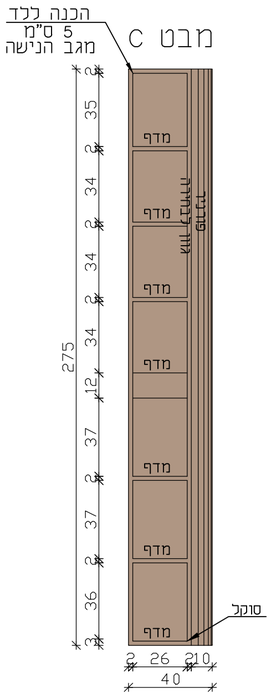

מבט D – חלוקה פנימית

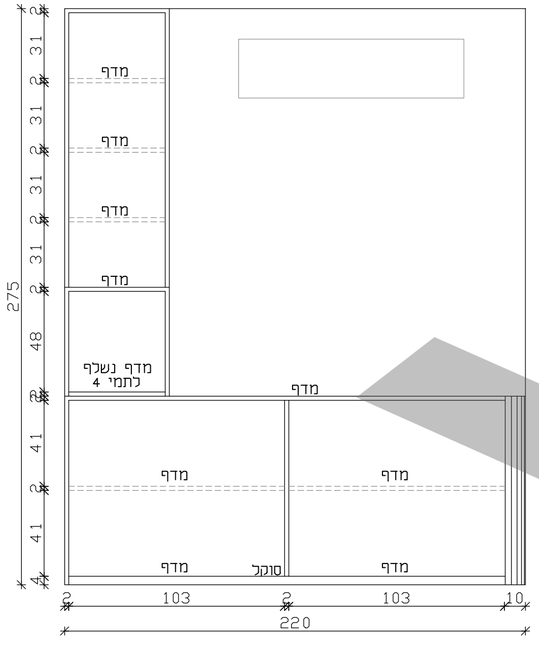

מבט D – חזית

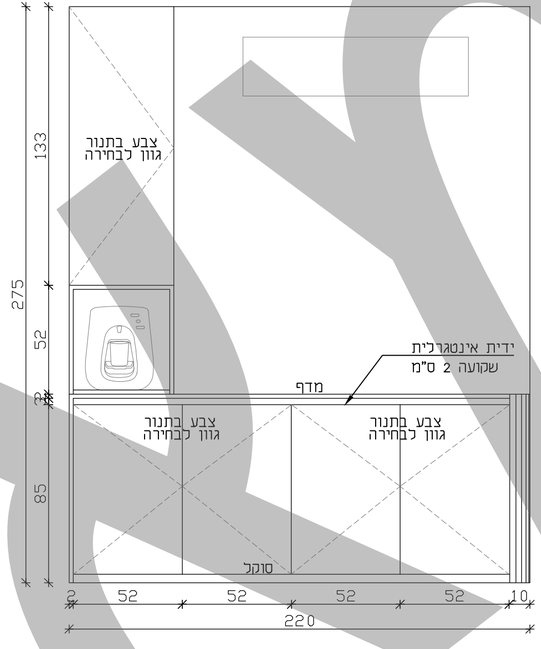


לקוח: טלי והרנן גומלסקי	כתובת: שקנאי 12 צורן	תכנית: נגרות פ.משפחה
חתימת לקוח לאישור תכנית: _____	● לעיון ○ לאישור ○ למכרז ○ לביצוע	גיליון מס: 5 / גודל גיליון: -- / תאריך: 7.10.26 / קנ"מ: 1:20


הערות:

1. על המבצע לבדוק את התאמת התכנית בשטח, לפני הבנייה, ולבקר את המידות. על כל טעות ו/או אי התאמה יש לעדכן משרד מתכנן.
2. אין לקבוע מידות ע"פ שרטוט. המידות המחייבות הן המידות שנמדדו בשטח לאחר ביצוע.
3. המידות בתכנית הן ברוטו–כלא חיפוי גמר.
4. יתכנו שינויים בהתאם להוראות הביצוע הסופי.
5. כל התכניות נשארות רכוש המתכנן: אין לעשות בהן שימוש ללא אישור בכתב המתכנן.
6. כל ההערות תקפות אלא אם צוין אחרת.


RK
RUTH KOLSKY
תכנון - עיצוב - השראה

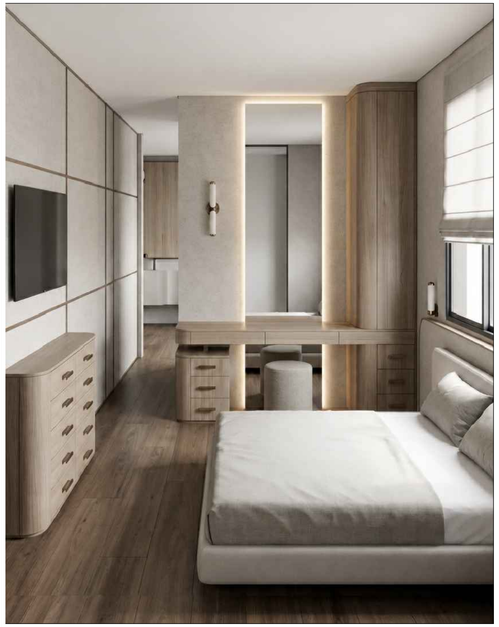

מבט C

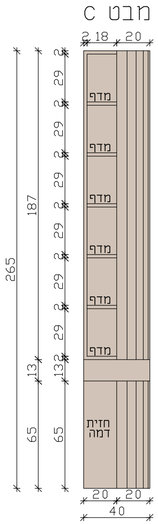


מבט B

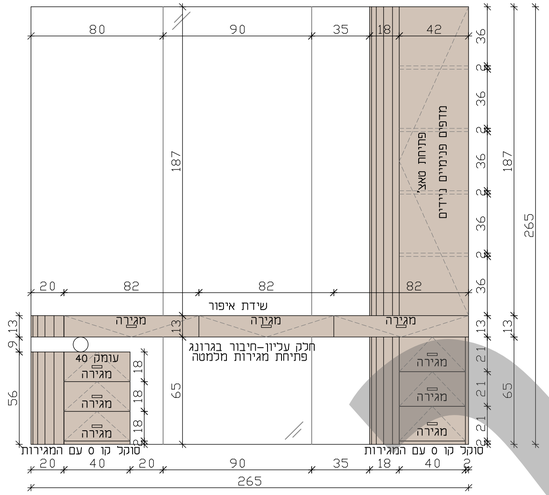


ידית




מבט A

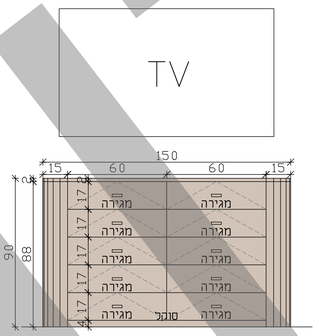


מבט על

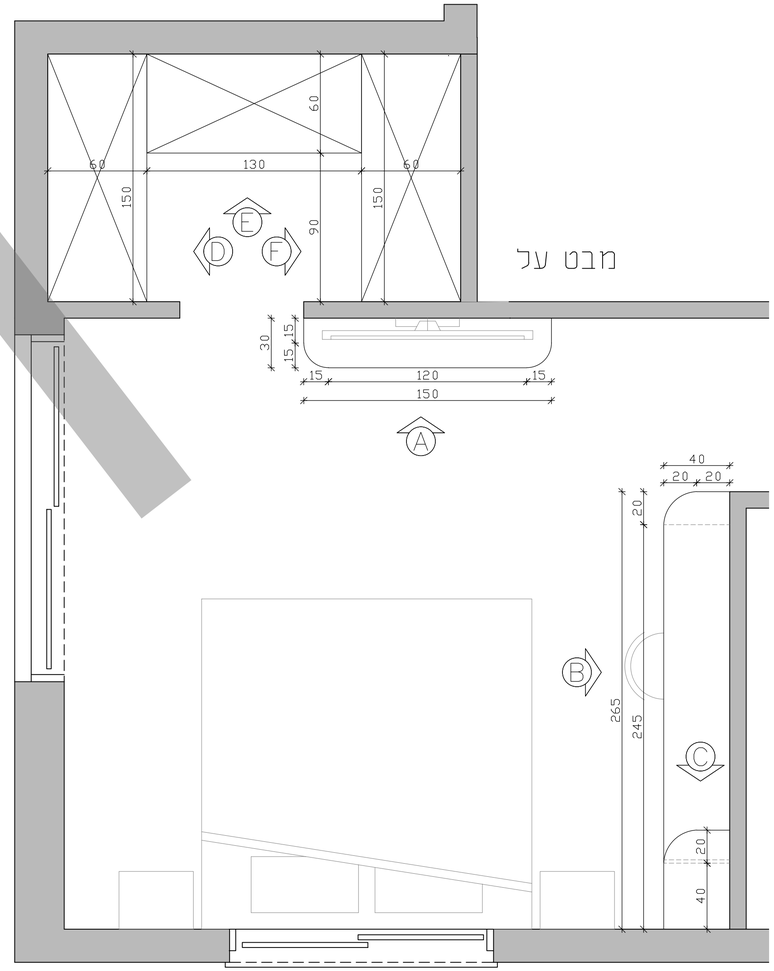


הדמיות

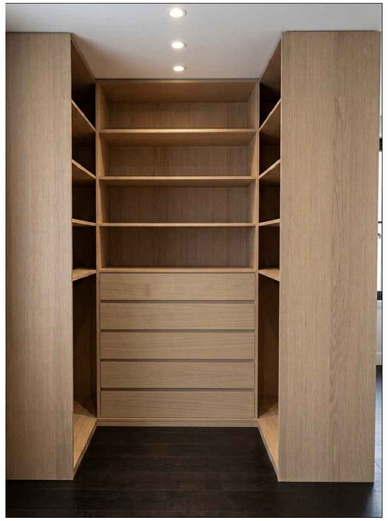


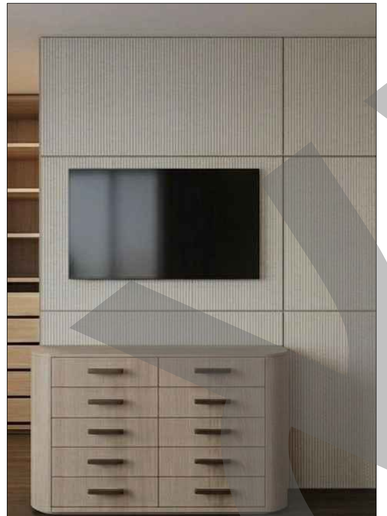

מבט D+F

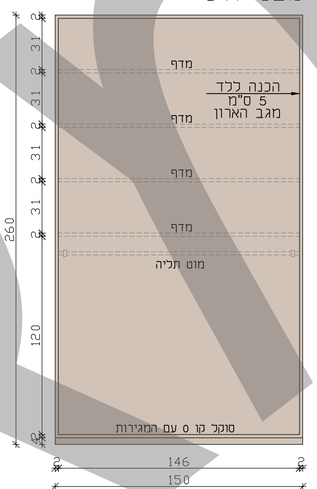

מבט E

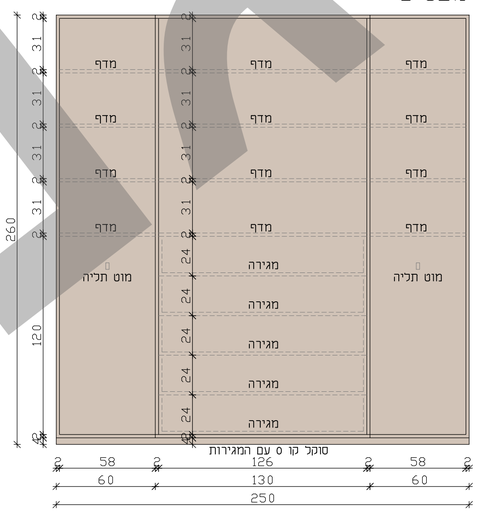

- מידות סופיות ילקחו מהשטח ע"י הנגר
- גוף הארון–סנדוויץ'
- גמר חזיתות–פורניר מולבן
- גוונים יבחרו ע"י המעצבת מול הנגר
- ידיות חיצוניות/פתיחת טאצ
- מדפים ניידים

הערות:


1. על המבצע לבדוק את התאמת התכנית בשטח, לפני הבנייה, ולבקר את המידות. על כל טעות ו/או אי התאמה יש לעדכן משרד מתכנן.
2. אין לקבוע מידות ע"פ שרטוט. המידות המחייבות הן המידות שנמדדו בשטח לאחר ביצוע.
3. המידות בתכנית הן ברוטו–ללא חיפוי גמר.
4. יתכנו שינויים בהתאם להוראות הביצוע הסופי.
5. כל התכניות נשארות רכוש המתכנן: אין לעשות בהן שימוש ללא אישור בכתב המתכנן.
6. כל ההערות תקפות אלא אם צוין אחרת.

RK
RUTH KOLSKY
תכנון - עיצוב - השראה


לקוח: טלי והרנן גומלסקי	כתובת: שקנאי 12 צורן	תכנית: נגרות מאסטר הורים
חתימת לקוח לאישור תכנית: _____	● לעיון ○ לאישור ○ למכרז ○ לביצוע	גיליון מס: 5 / גודל גיליון: --
		תאריך: 7.10.26 / קנ"מ: 1:20

ארון רחצה מרתף


מבט על

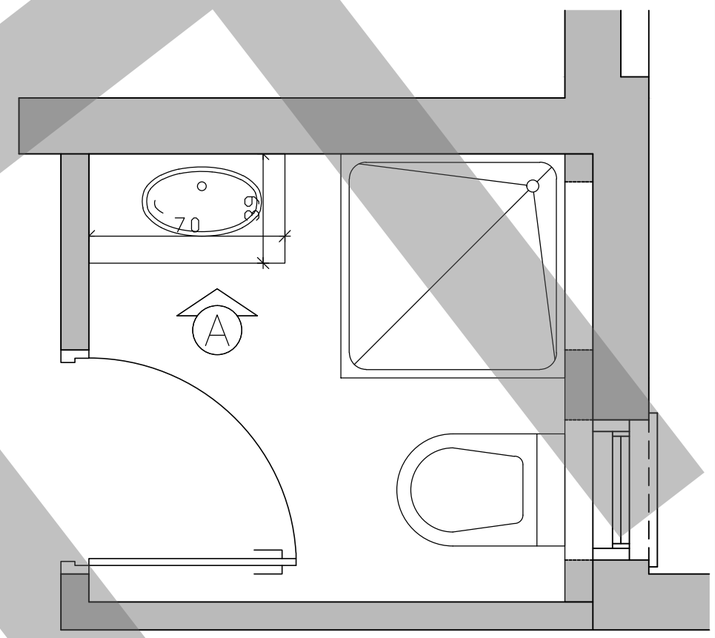

מבט A

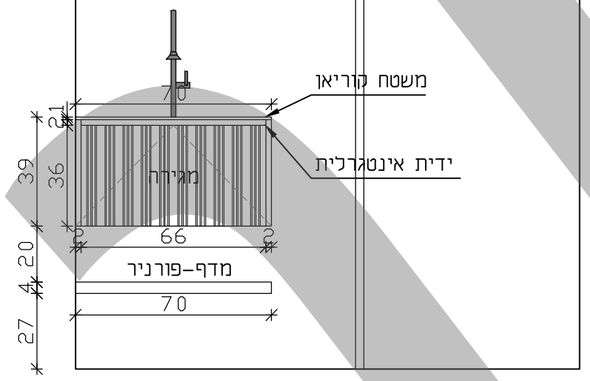


פרט חירוץ

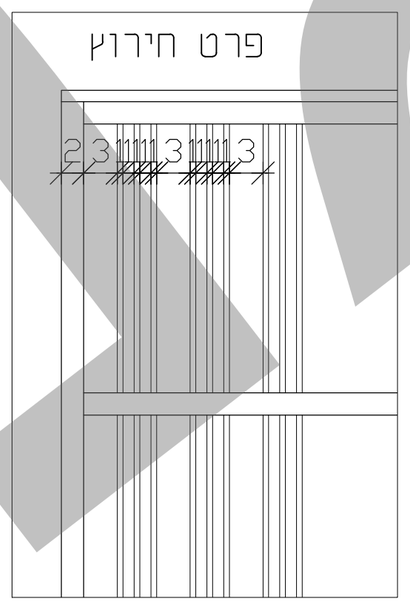


* מידות סופיות ילקחו מהשטח ע"י הנגר
* גוף הארון-סנדוויץ'
* גמר חזיתות-פורניר מחורץ ברוחב ועומק 0.5 ס"מ
  מרווח בין חריצים 1 ס"מ
  מרווח בין מקבץ חריצים 3 ס"צ
* גוונים יבחרו ע"י המעצבת מול הנגר
* ידית אינטגרלית

ארון רחצה יח"ד

מבט על

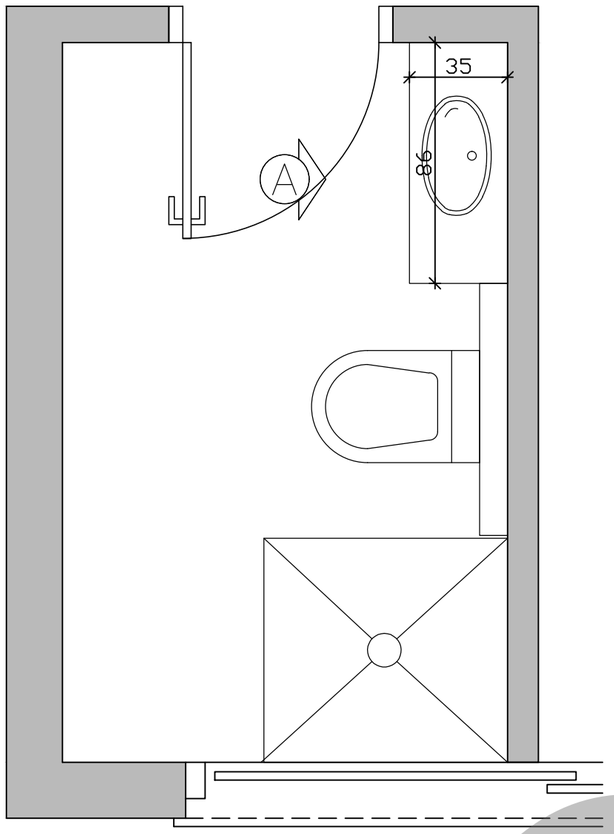

מבט A

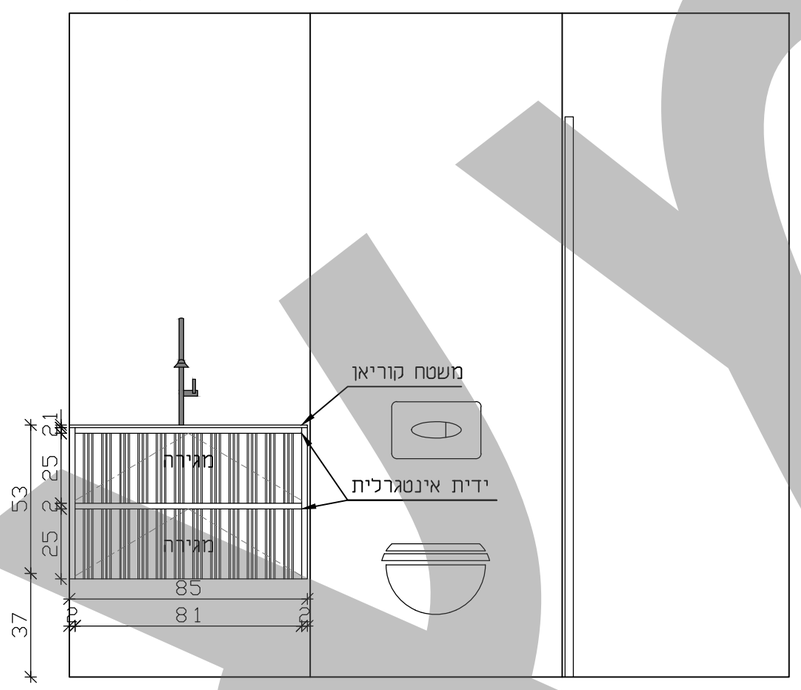

הערות:

1. על המבצע לבדוק את התאמת התכנית בשטח, לפני הבנייה, ולבקר את המידות. על כל טעות ו/או אי התאמה יש לעדכן משרד מתכנן.
2. אין לקבוע מידות ע"פ שרטוט. המידות המחייבות הן המידות שנמדדו בשטח לאחר ביצוע.
3. המידות בתכנית הן ברוטו-ללא חיפוי גמר.
4. יתכנו שינויים בהתאם להוראות הביצוע הסופי.
5. כל התכניות נשארות רכוש המתכנן: אין לעשות בהן שימוש ללא אישור בכתב המתכנן.
6. כל ההערות תקפות אלא אם צוין אחרת.

לקוח: טלי והרנן גומלסקי	כתובת: שקנאי 12 צורן	תכנית: נגרות ארונות רחצה קומת מרתף
חתימת לקוח לאישור תכנית: _____	● לעיון ○ לאישור ○ למכרז ○ לביצוע	גיליון מס': 5 / גודל גיליון: -- / תאריך: 7.10.26 / קנ"מ: 1:20

RK
RUTH KOLSKY
תכנון - עיצוב - השראה