


רח' יהודה הנשיא

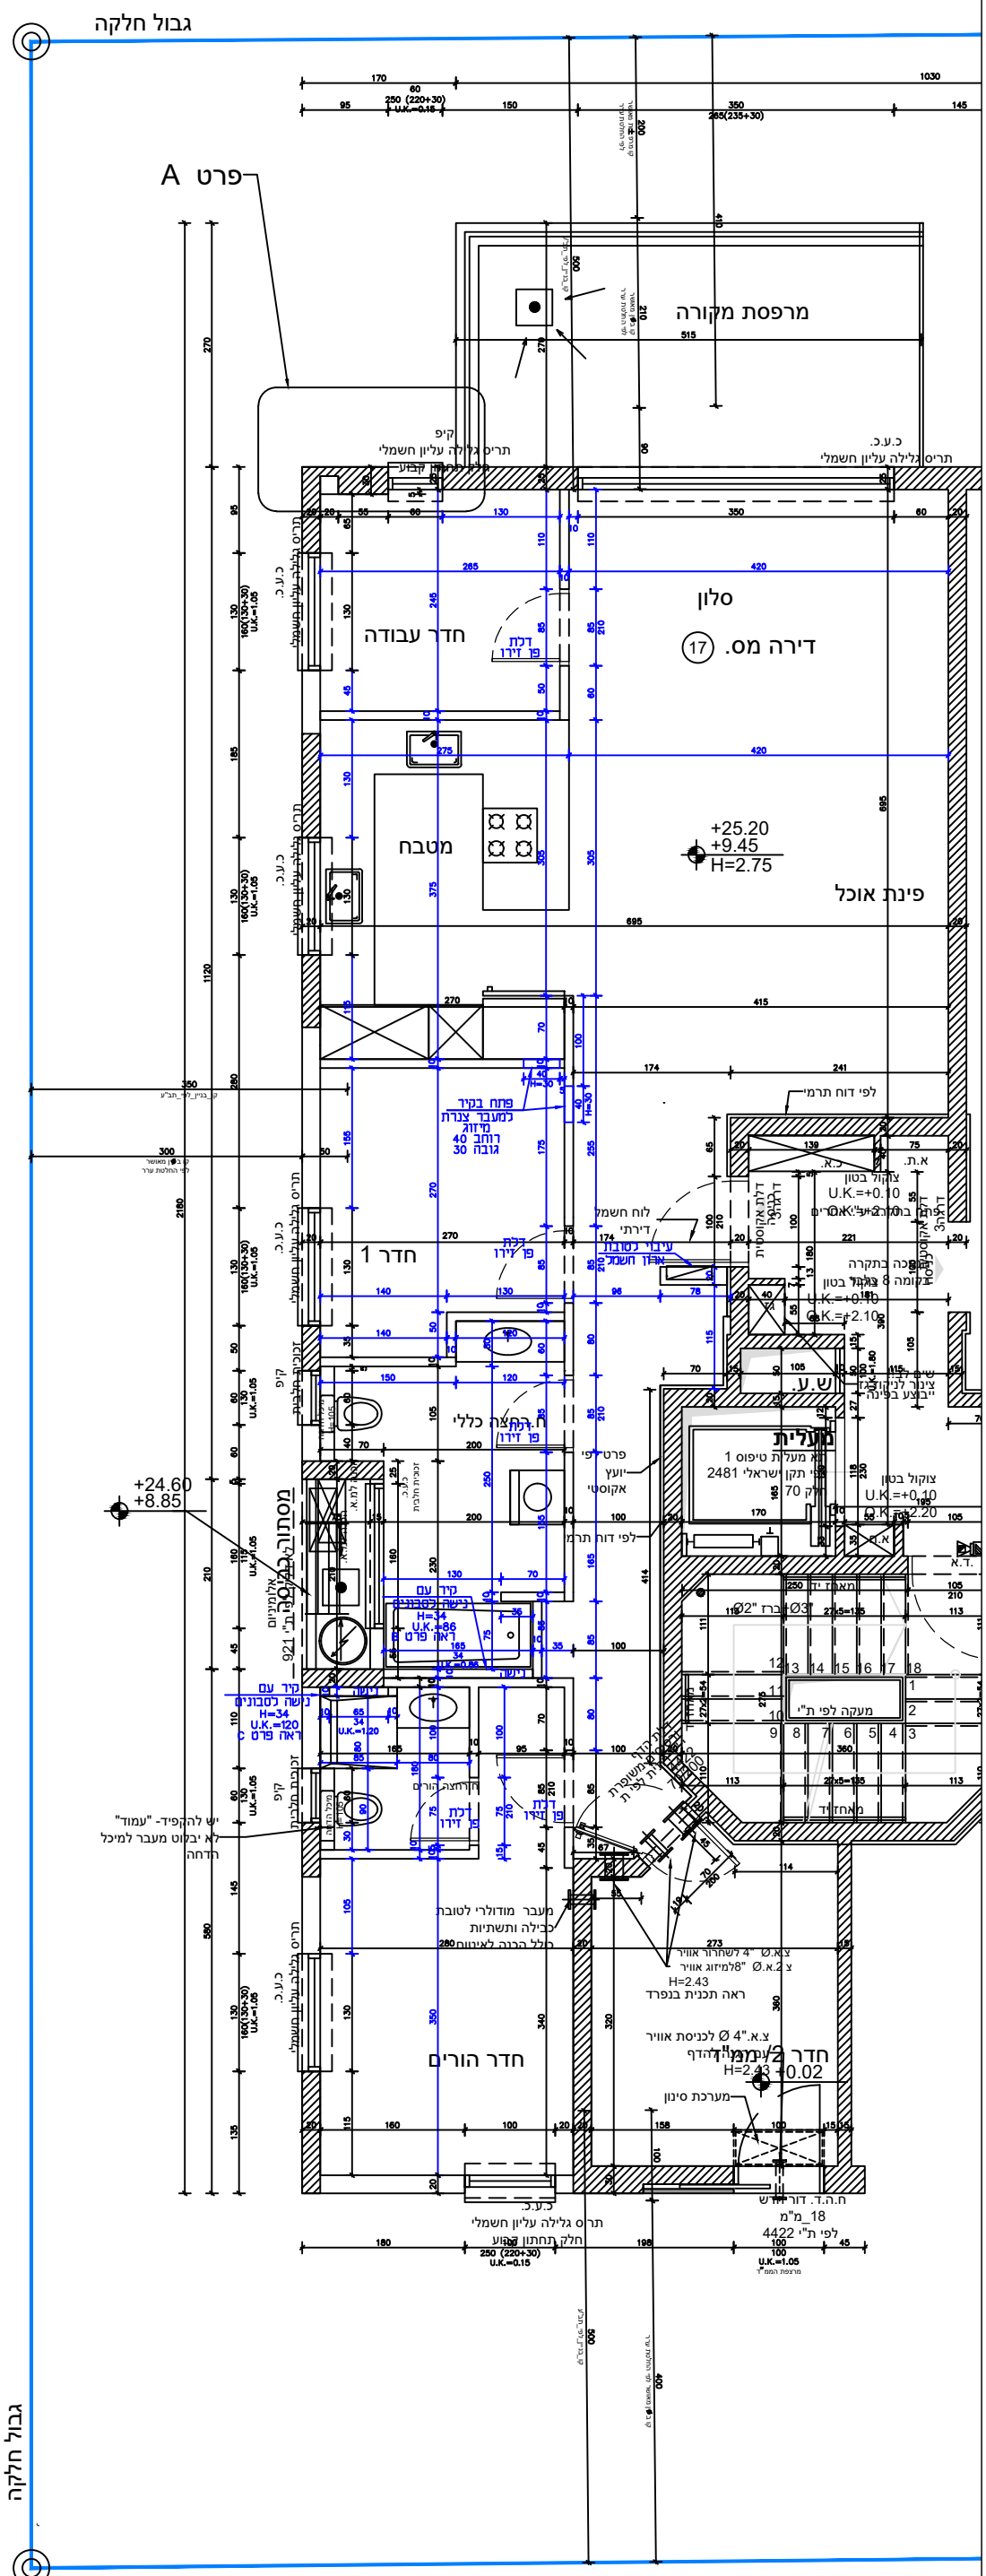

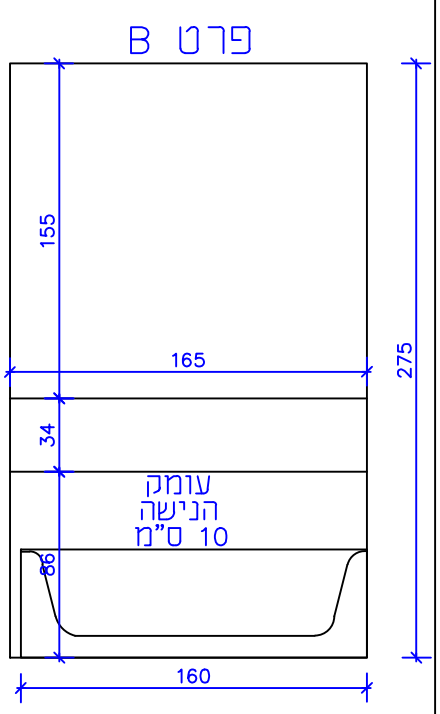

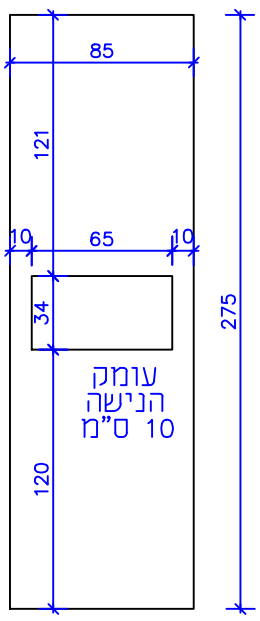

לקוח:
מרדכי וחגית פוגל

תכנית:
בינוי

כתובת:
יהודה הנשיא 12 דירה 17

גיליון מס':	גודל גיליון:	תאריך:	קנ"מ:
1	A3	4.5.26	1:75

חתימת לקוח לאישור תכנית:

_____

● לעיון ○ לאישור
○ למכרז ○ לביצוע

הערות:
1. על המבצע לבדוק את התאמת התכנית בשטח, לפני הבניה, ולבקר את המידות. על כל טעות ו/או אי התאמה יש לעדכן משרד מתכנן.
2. אין לקבוע מידות ע"פ שרטוט. המידות המחייבות הן המידות שנמדדו בשטח לאחר ביצוע.
3. המידות בתכנית הן ברוטו –ללא חיפוי גמר.
4. יתכנו שינויים בהתאם להוראות הביצוע הסופי.
5. כל התכניות נשארות רכוש המתכנן: אין לעשות בהן שימוש ללא אישור בכתב המתכנן.
6. כל ההערות תקפות אלא אם צוין אחרת.

RK
RUTH KOLSKY
תכנון - עיצוב - השראה

לקוח:
מרדכי וחגית פוגל


תכנית:
אינסטלציה


כתובת:
יהודה הנשיא 12 דירה 17

גיליון מס':	גודל גיליון:	תאריך:	קנ"מ:
2	A3	4.5.26	1:75

חתימת לקוח לאישור תכנית:

● לעיון ○ לאישור
○ למכרז ○ לביצוע

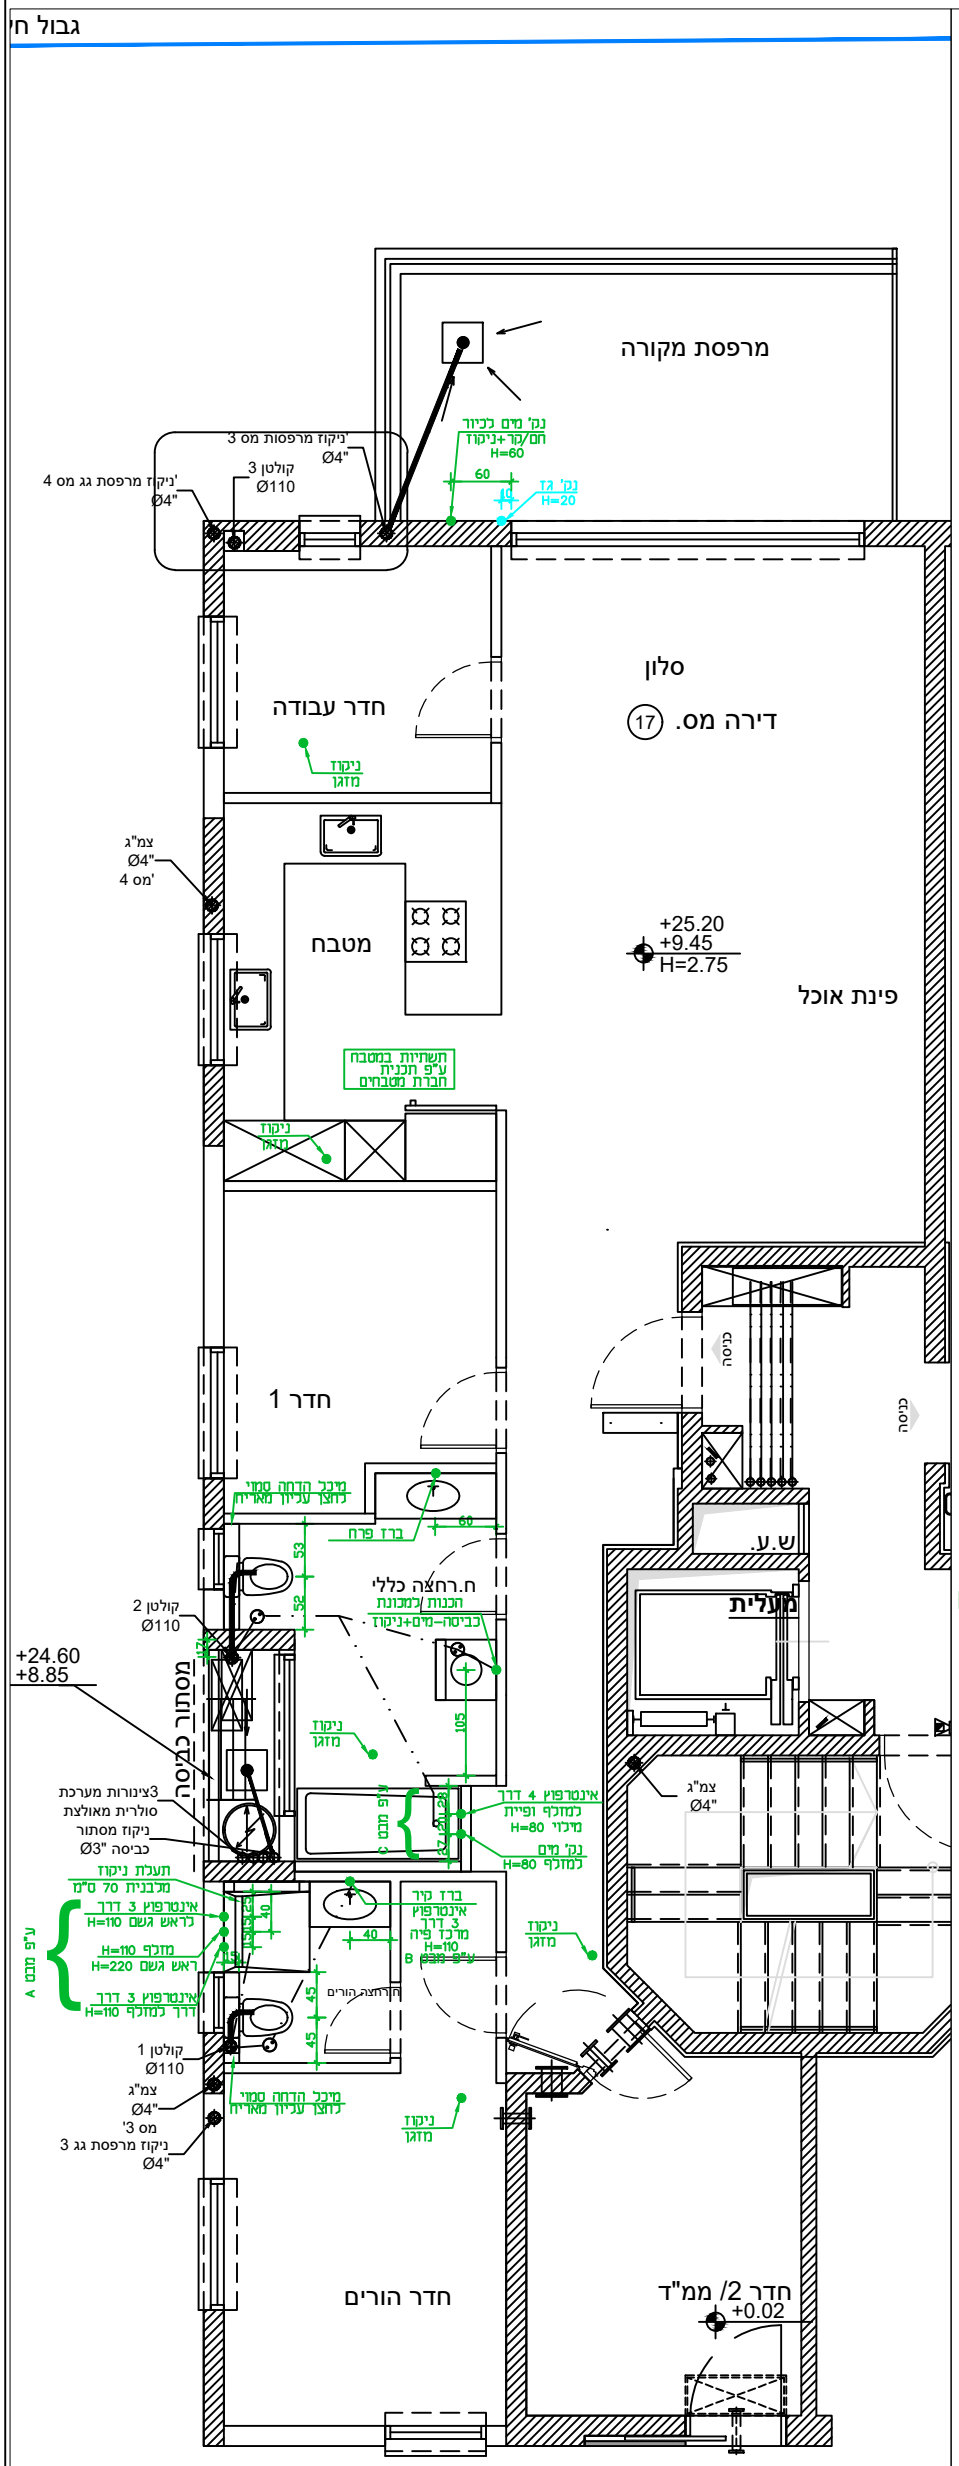

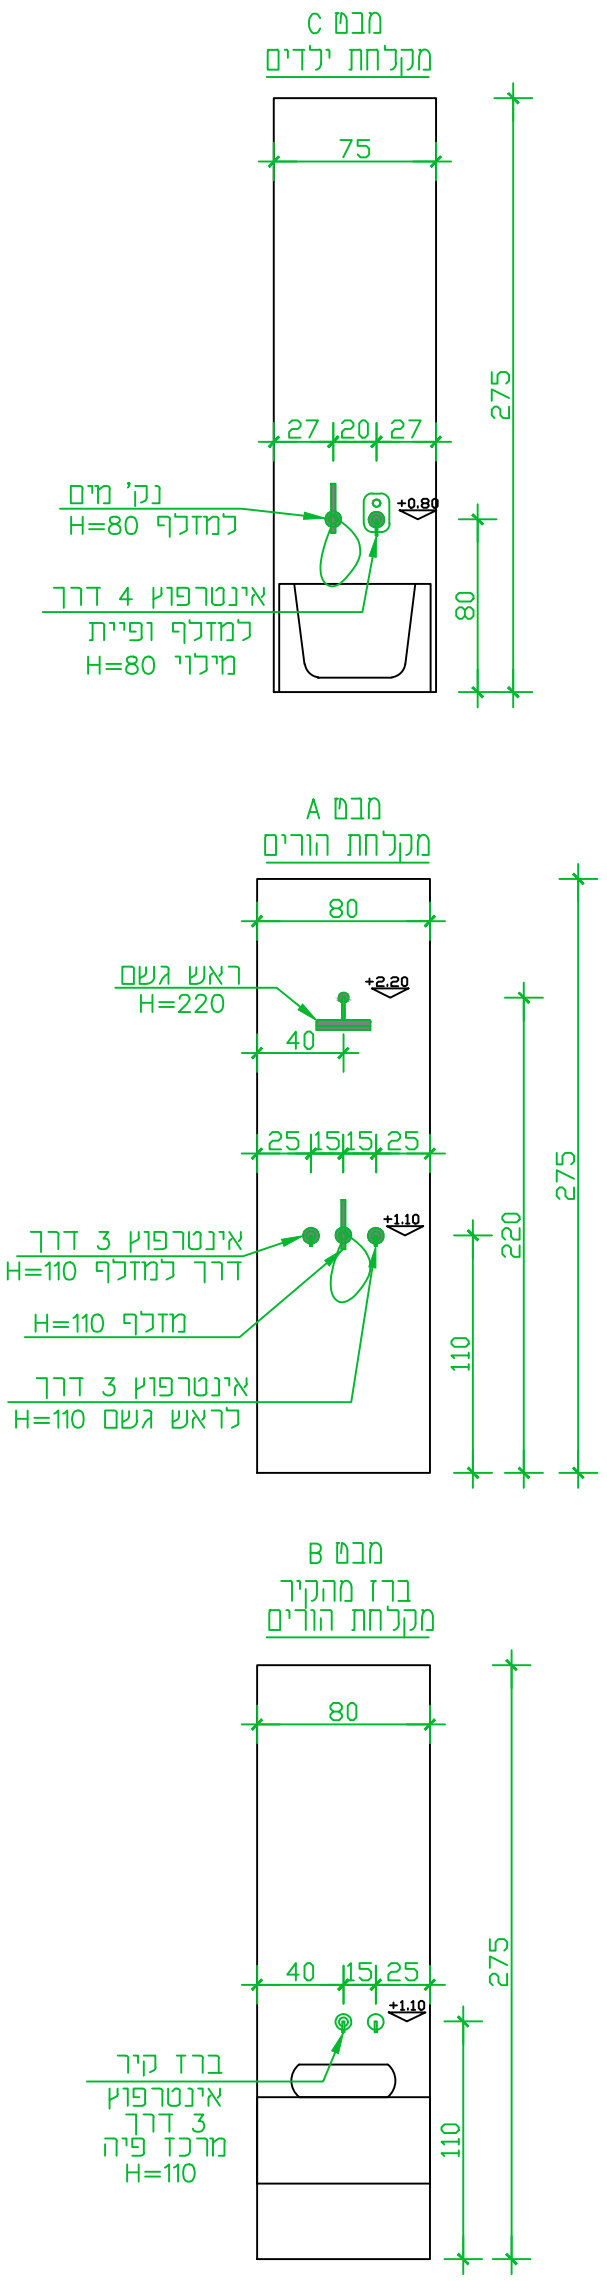

הערות:
1. על המבצע לבדוק את התאמת התכנית בשטח, לפני הבניה, ולבקר את המידות. על כל טעות ו/או אי התאמה יש לעדכן משרד מתכנן.
2. אין לקבוע מידות ע"פ שרטוט. המידות המחייבות הן המידות שנמדדו בשטח לאחר ביצוע.
3. המידות בתכנית הן ברוטו –ללא חיפוי גמר.
4. יתכנו שינויים בהתאם להוראות הביצוע הסופי.
5. כל התכניות נשארות רכוש המתכנן: אין לעשות בהן שימוש ללא אישור בכתב המתכנן.
6. כל ההערות תקפות אלא אם צוין אחרת.

RK
RUTH KOLSKY
תכנון - עיצוב - השראה

לקוח:
מרדכי וחגית פוגל

תכנית:
חשמל

כתובת:
יהודה הנשיא 12 דירה 17

גיליון מס':	גודל גיליון:	תאריך:	קנ"מ:
3	A3	4.5.26	1:75


חתימת לקוח לאישור תכנית:

_____

● לעיון ○ לאישור
○ למכרז ○ לביצוע

רח' יהודה הנשיא

גבול

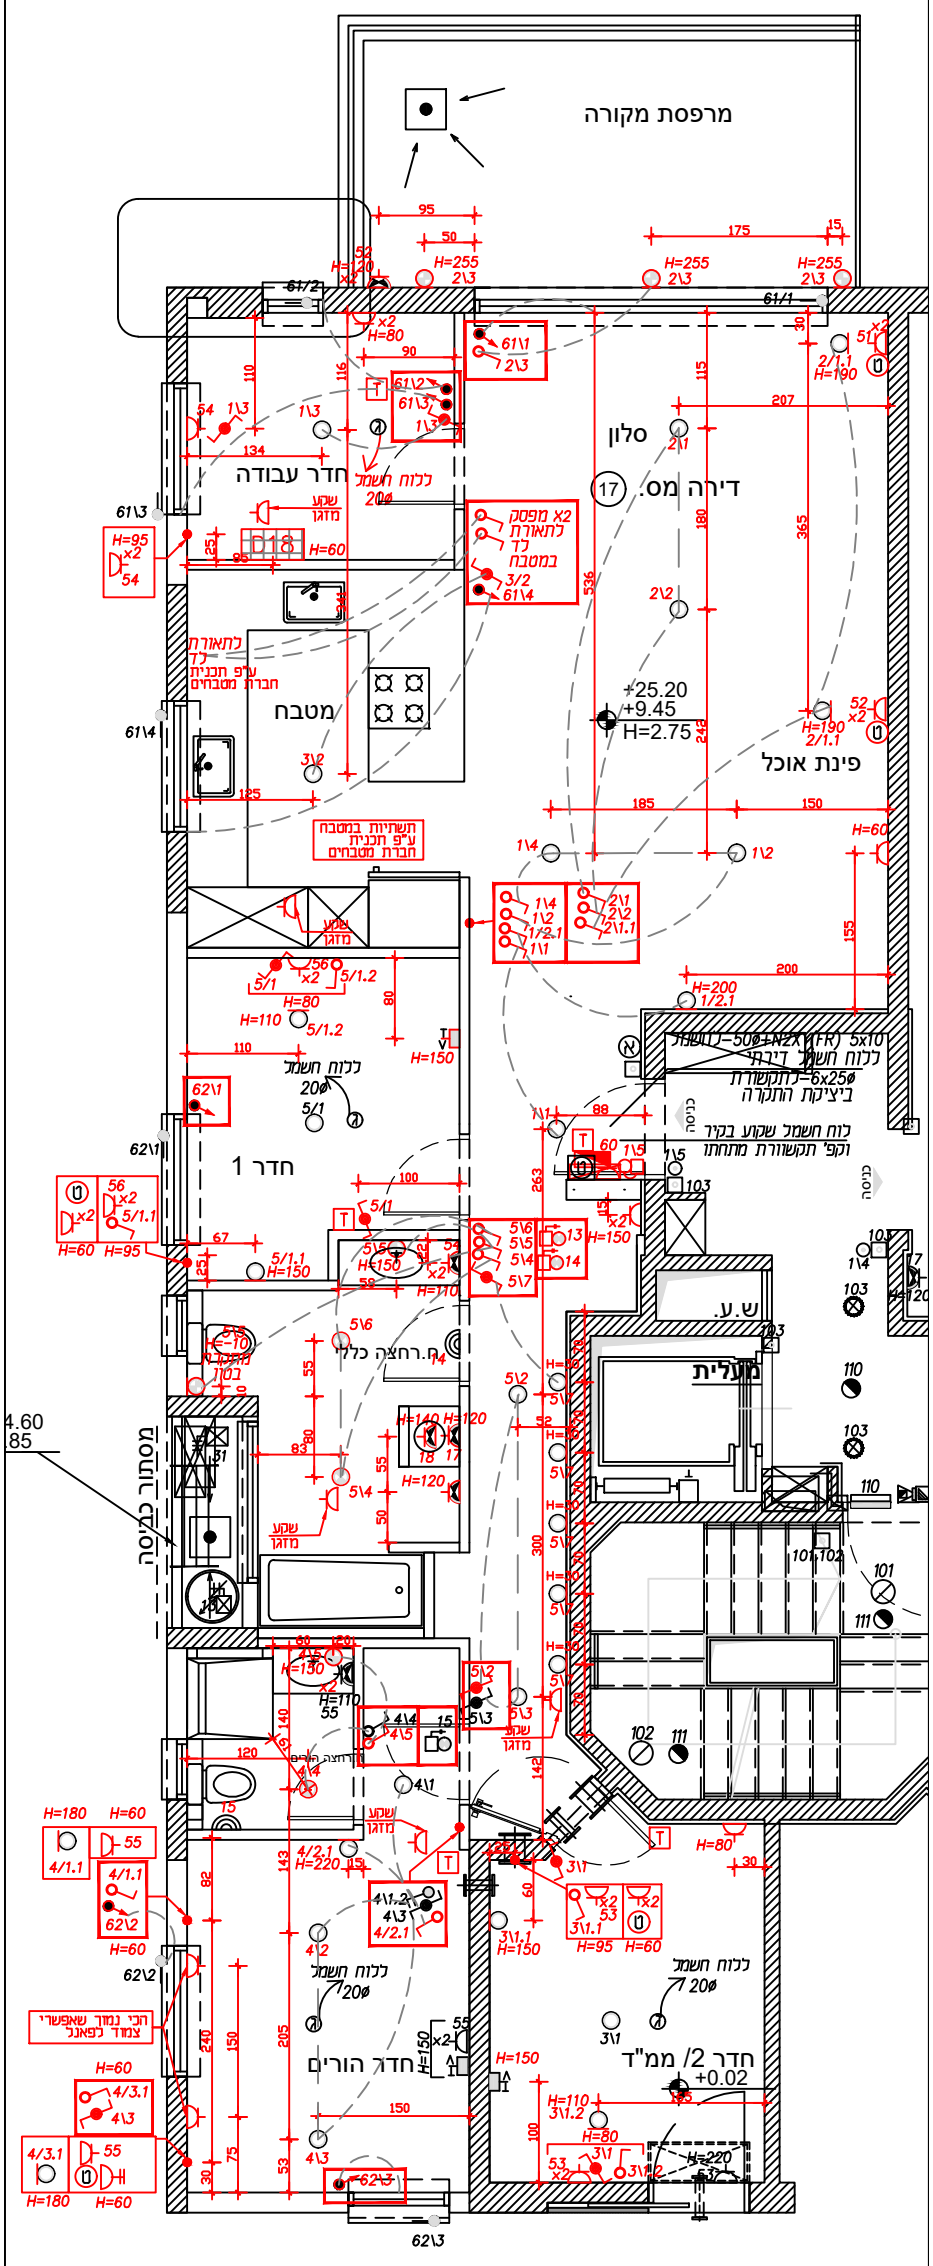

הערות:
1. על המבצע לבדוק את התאמת התכנית בשטח, לפני הבניה, ולבקר את המידות. על כל טעות ו/או אי התאמה יש לעדכן משרד מתכנן.
2. אין לקבוע מידות ע"פ שרטוט. המידות המחייבות הן המידות שנמדדו בשטח לאחר ביצוע.
3. המידות בתכנית הן ברוטו –ללא חיפוי גמר.
4. יתכנו שינויים בהתאם להוראות הביצוע הסופי.
5. כל התכניות נשארות רכוש המתכנן: אין לעשות בהן שימוש ללא אישור בכתב המתכנן.
6. כל ההערות תקפות אלא אם צוין אחרת.

RK
RUTH KOLSKY
תכנון - עיצוב - השראה