נשמרה בב"ש
יבוצע עפ"י ת"י 5100
ונפי ת"י 921 תכן 2

ח.שינה/ממ"ד

שולחן לימודים

ח.רחצה

ח.כביסה

ח.שינה/עבודה

שידת איפור

ח.רחצה

מקפיא B.I

מטבח

ח.ארונות

פינת התארגנות

ח.שינה הורים

שידת איפור

חלון חילוץ

מעקה זכוכית עפ"י התקן

מ.מקורה

מעקה זכוכית עפ"י התקן

MAYA COHEN GOLDMAN
INTERIOR DESIGN

לקוח: סטאחי דורון ושרי	תכנית: העמדת ריהוט				חתימת לקוח לאישור תכנית:	
כתובת: האמהות 7–9 רחובות	גיליון מס': 1	גודל גיליון: A3	תאריך: 12.1.26	קנ"מ: 1:50	○ לעיון ● לאישור	○ למכרז ○ לביצוע

ח.שינה/ממ"ד

ח.שינה/עבודה

ח.רחצה

ח.כביסה

ח.רחצה

ח.ארונות

ח.שינה הורים

מטבח

חלון חילוץ

מעקה זכוכית עפ"י התקן

מקפיא

B.I

תוספת דלת
עץ פנימית

קיר עם
נישה לסבונם
בשיפוע קל
חיבור בגרונג
H=30
H=U.K.=125

דלת קו ס
91
o.k.=214
התקנת משקוף
נסתר
אחרי ריצוף
לפני שלב הטיח

קיר גבס

הגבהת נישת אסלה
עד לתקרה
חיבור בגרונג

נישת אסלה+
קיר נישה
עד לתקרה
חיבור בגרונג

נישה לסבונים
בשיפוע קל
חיבור בגרונג
H=30
H=U.K.=125

נישת אסלה+
קיר נישה
עד לתקרה
חיבור בגרונג

מיכל הדחה+
נישת אסלה
בנישה אחת
H=125
חיבור בגרונג

הגבהת קיר קולטן
עד לתקרה

2 cm

מ.מקורה

105
o.k.=210

80
o.k.=210

210
o.k.=210

MAYA COHEN GOLDMAN
INTERIOR DESIGN

לקוח: סטאחי דורון ושרי	תכנית: העמדת בניה				חתימת לקוח לאישור תכנית:
כתובת: האמהות 7–9 רחובות	גיליון מס': 2	גודל גיליון: A3	תאריך: 12.1.26	קנ"מ: 1:50	○ לעיון ● לאישור ○ למכרז ○ לביצוע

ח.שינה/ממ"ד

ח.שינה/עבודה

ח.כביסה

ח.רחצה

ח.ארונות

ח.שינה הורים

ח.רחצה

מטבח

מקפיא

B.I

חלון חילוץ

מ.מקורה

מעקה זכוכית עפ"י התקן

מעקה זכוכית עפ"י התקן

יבוצע עפ"י ת"י 5100
ולפי ת"י 921 חלק 2

נק' מים
למזלף H=110
ראש טוש
H=220

ברז קיר
H=100
בולכ התקנת
כיור

תעלת ניקוז
מלבנית

אינטרפוץ 4
דרך H=110

הכנה למכונת
כביסה H=60

ברז קיר
H=100
ללא התקנת
ארון רחצה

וונטה
בקיר

ברז גן


נק' גז

הכנה לכיור
נק' מים חם/קר
+ניקוז+הכנה
למדיח H=60

-2 cm


לקוח: סטאחי דורון ושרי	תכנית: אינסטלציה	חתימת לקוח לאישור תכנית:			
כתובת: האמהות 7-9 רחובות	גיליון מס': 3	גודל גיליון: A3	תאריך: 12.1.26	קנ"מ: 1:50	○ לעיון ● לאישור ○ למכרז ○ לביצוע

MAYA COHEN GOLDMAN
INTERIOR DESIGN

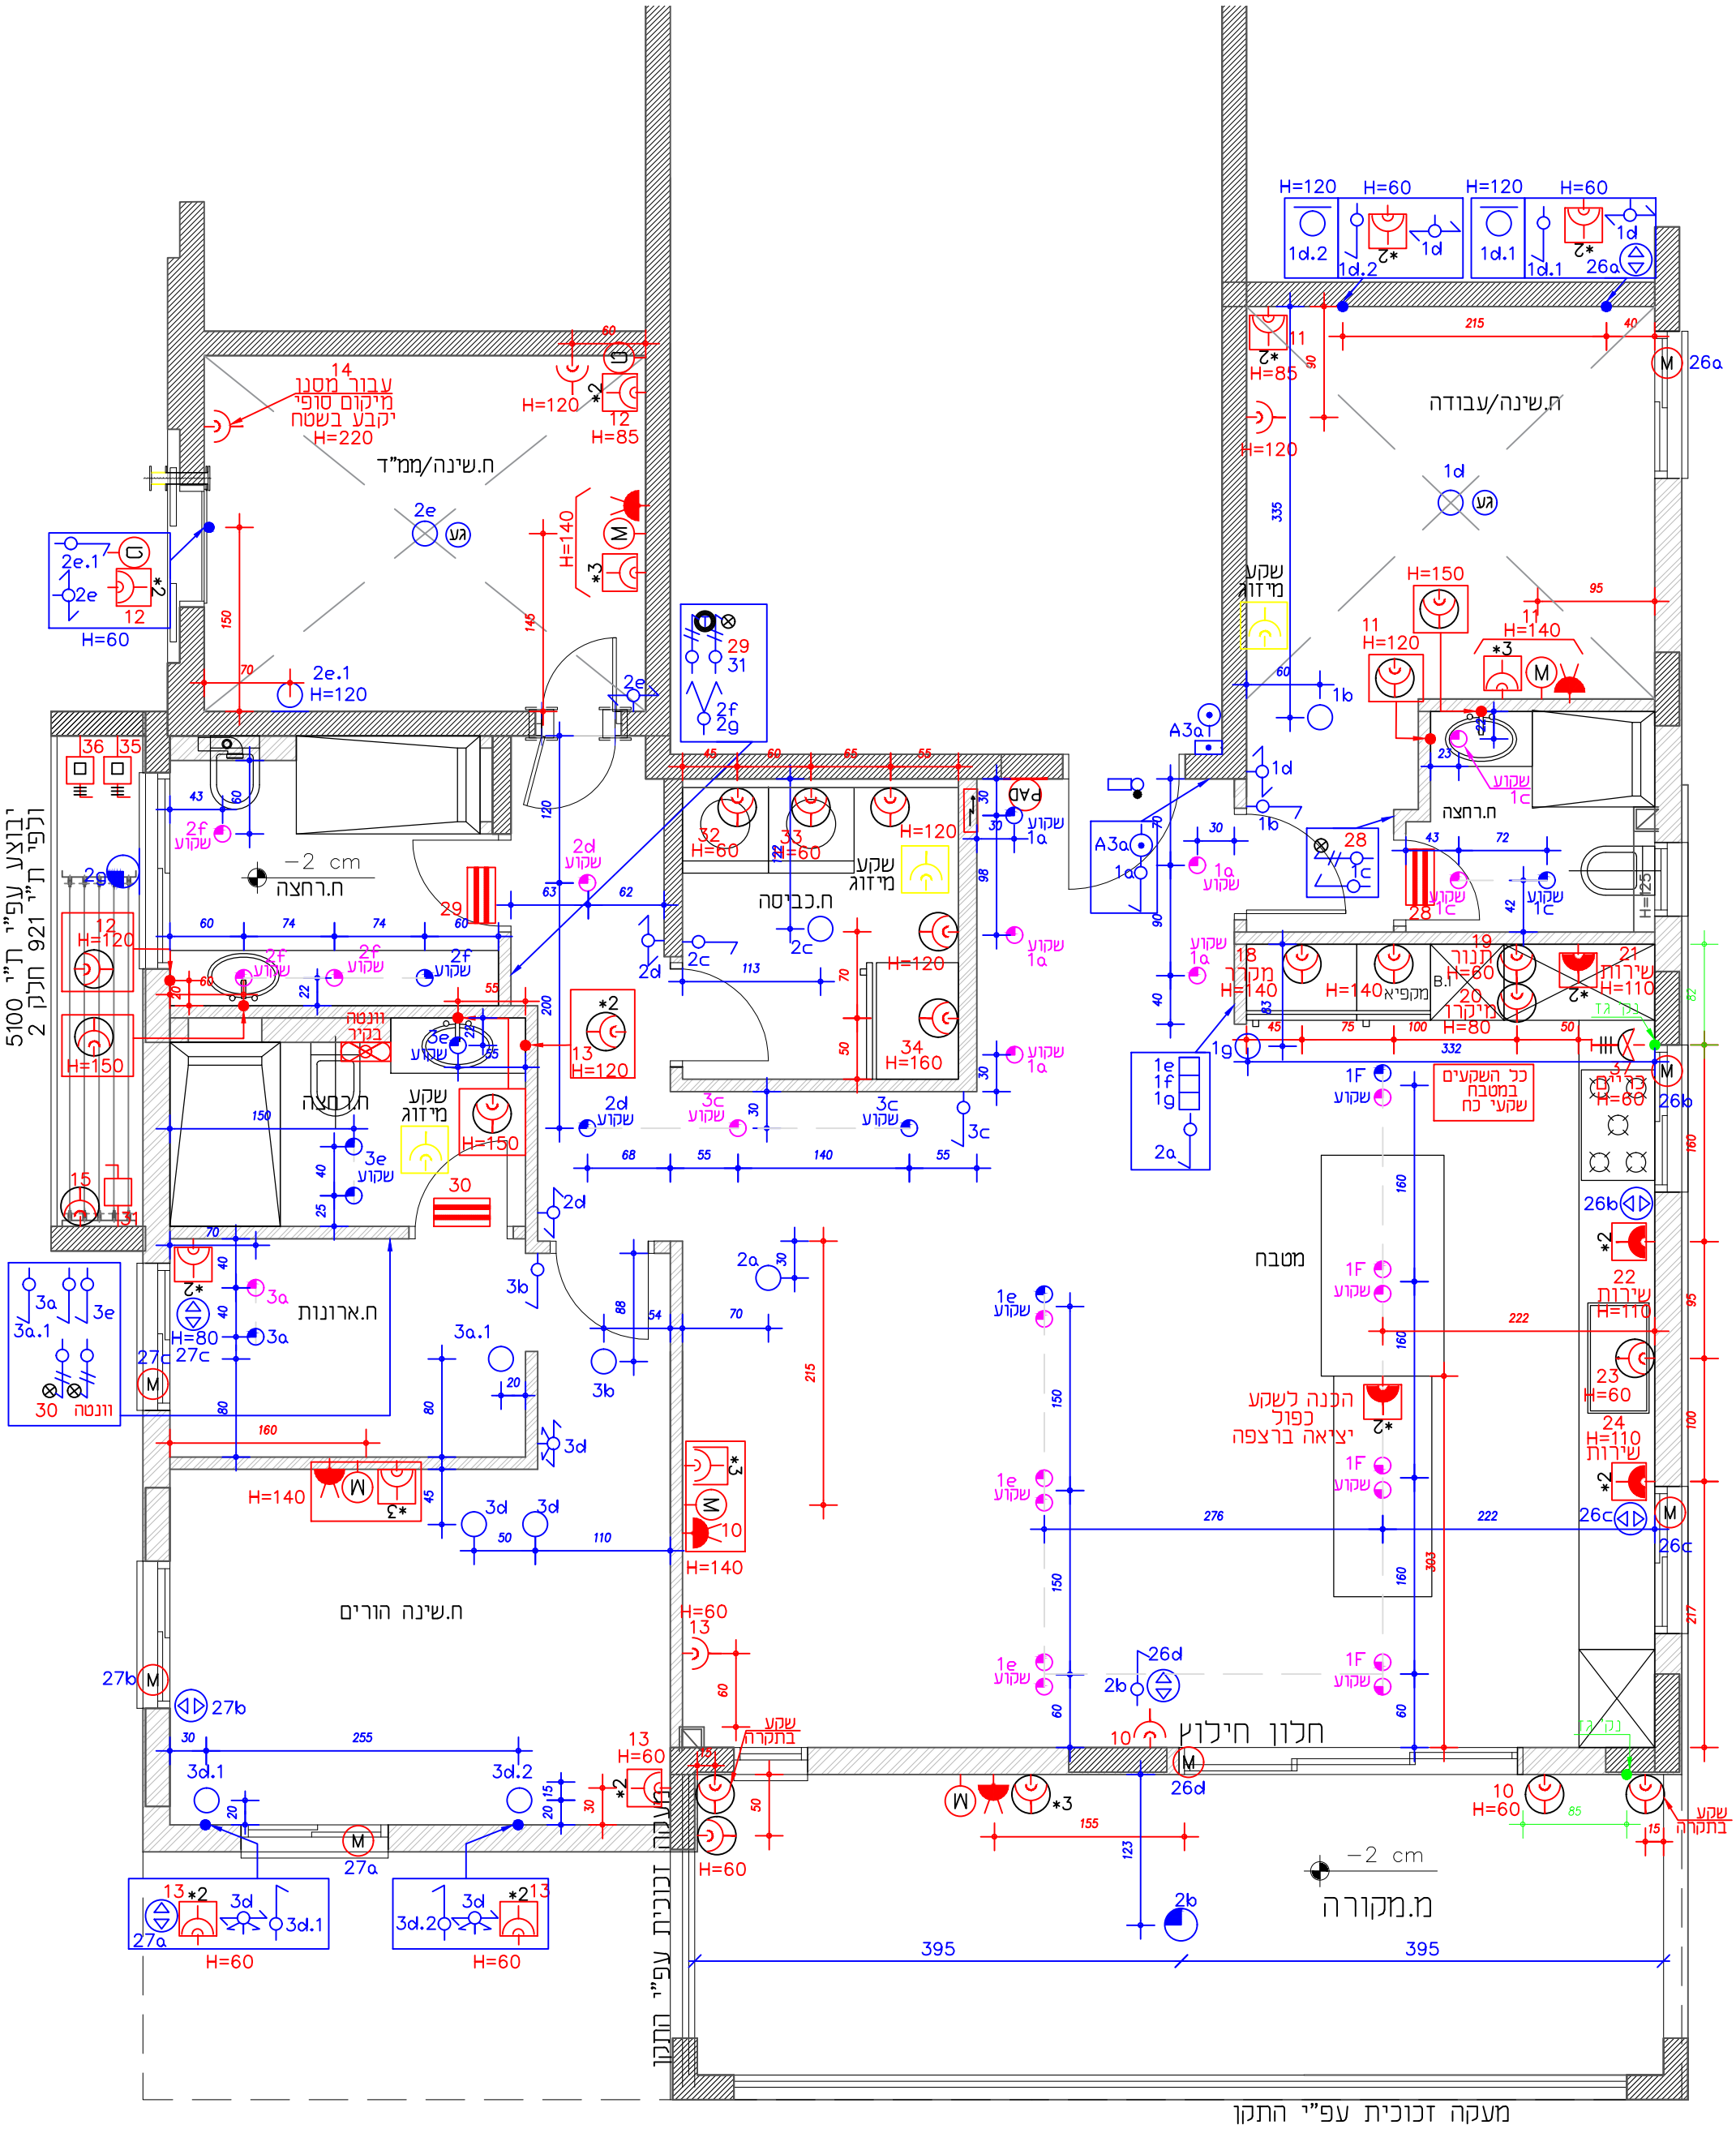


לקוח: סטאחי דורון ושרי	תכנית: חשמל	חתימת לקוח לאישור תכנית:				
כתובת: האמהות 7–9 רחובות	גיליון מס': 4	גודל גיליון: A3	תאריך: 12.1.26	קנ"מ: 1:50	○ לעיון ● לאישור ○ למכרז ○ לביצוע	

MAYA COHEN GOLDMAN
INTERIOR DESIGN

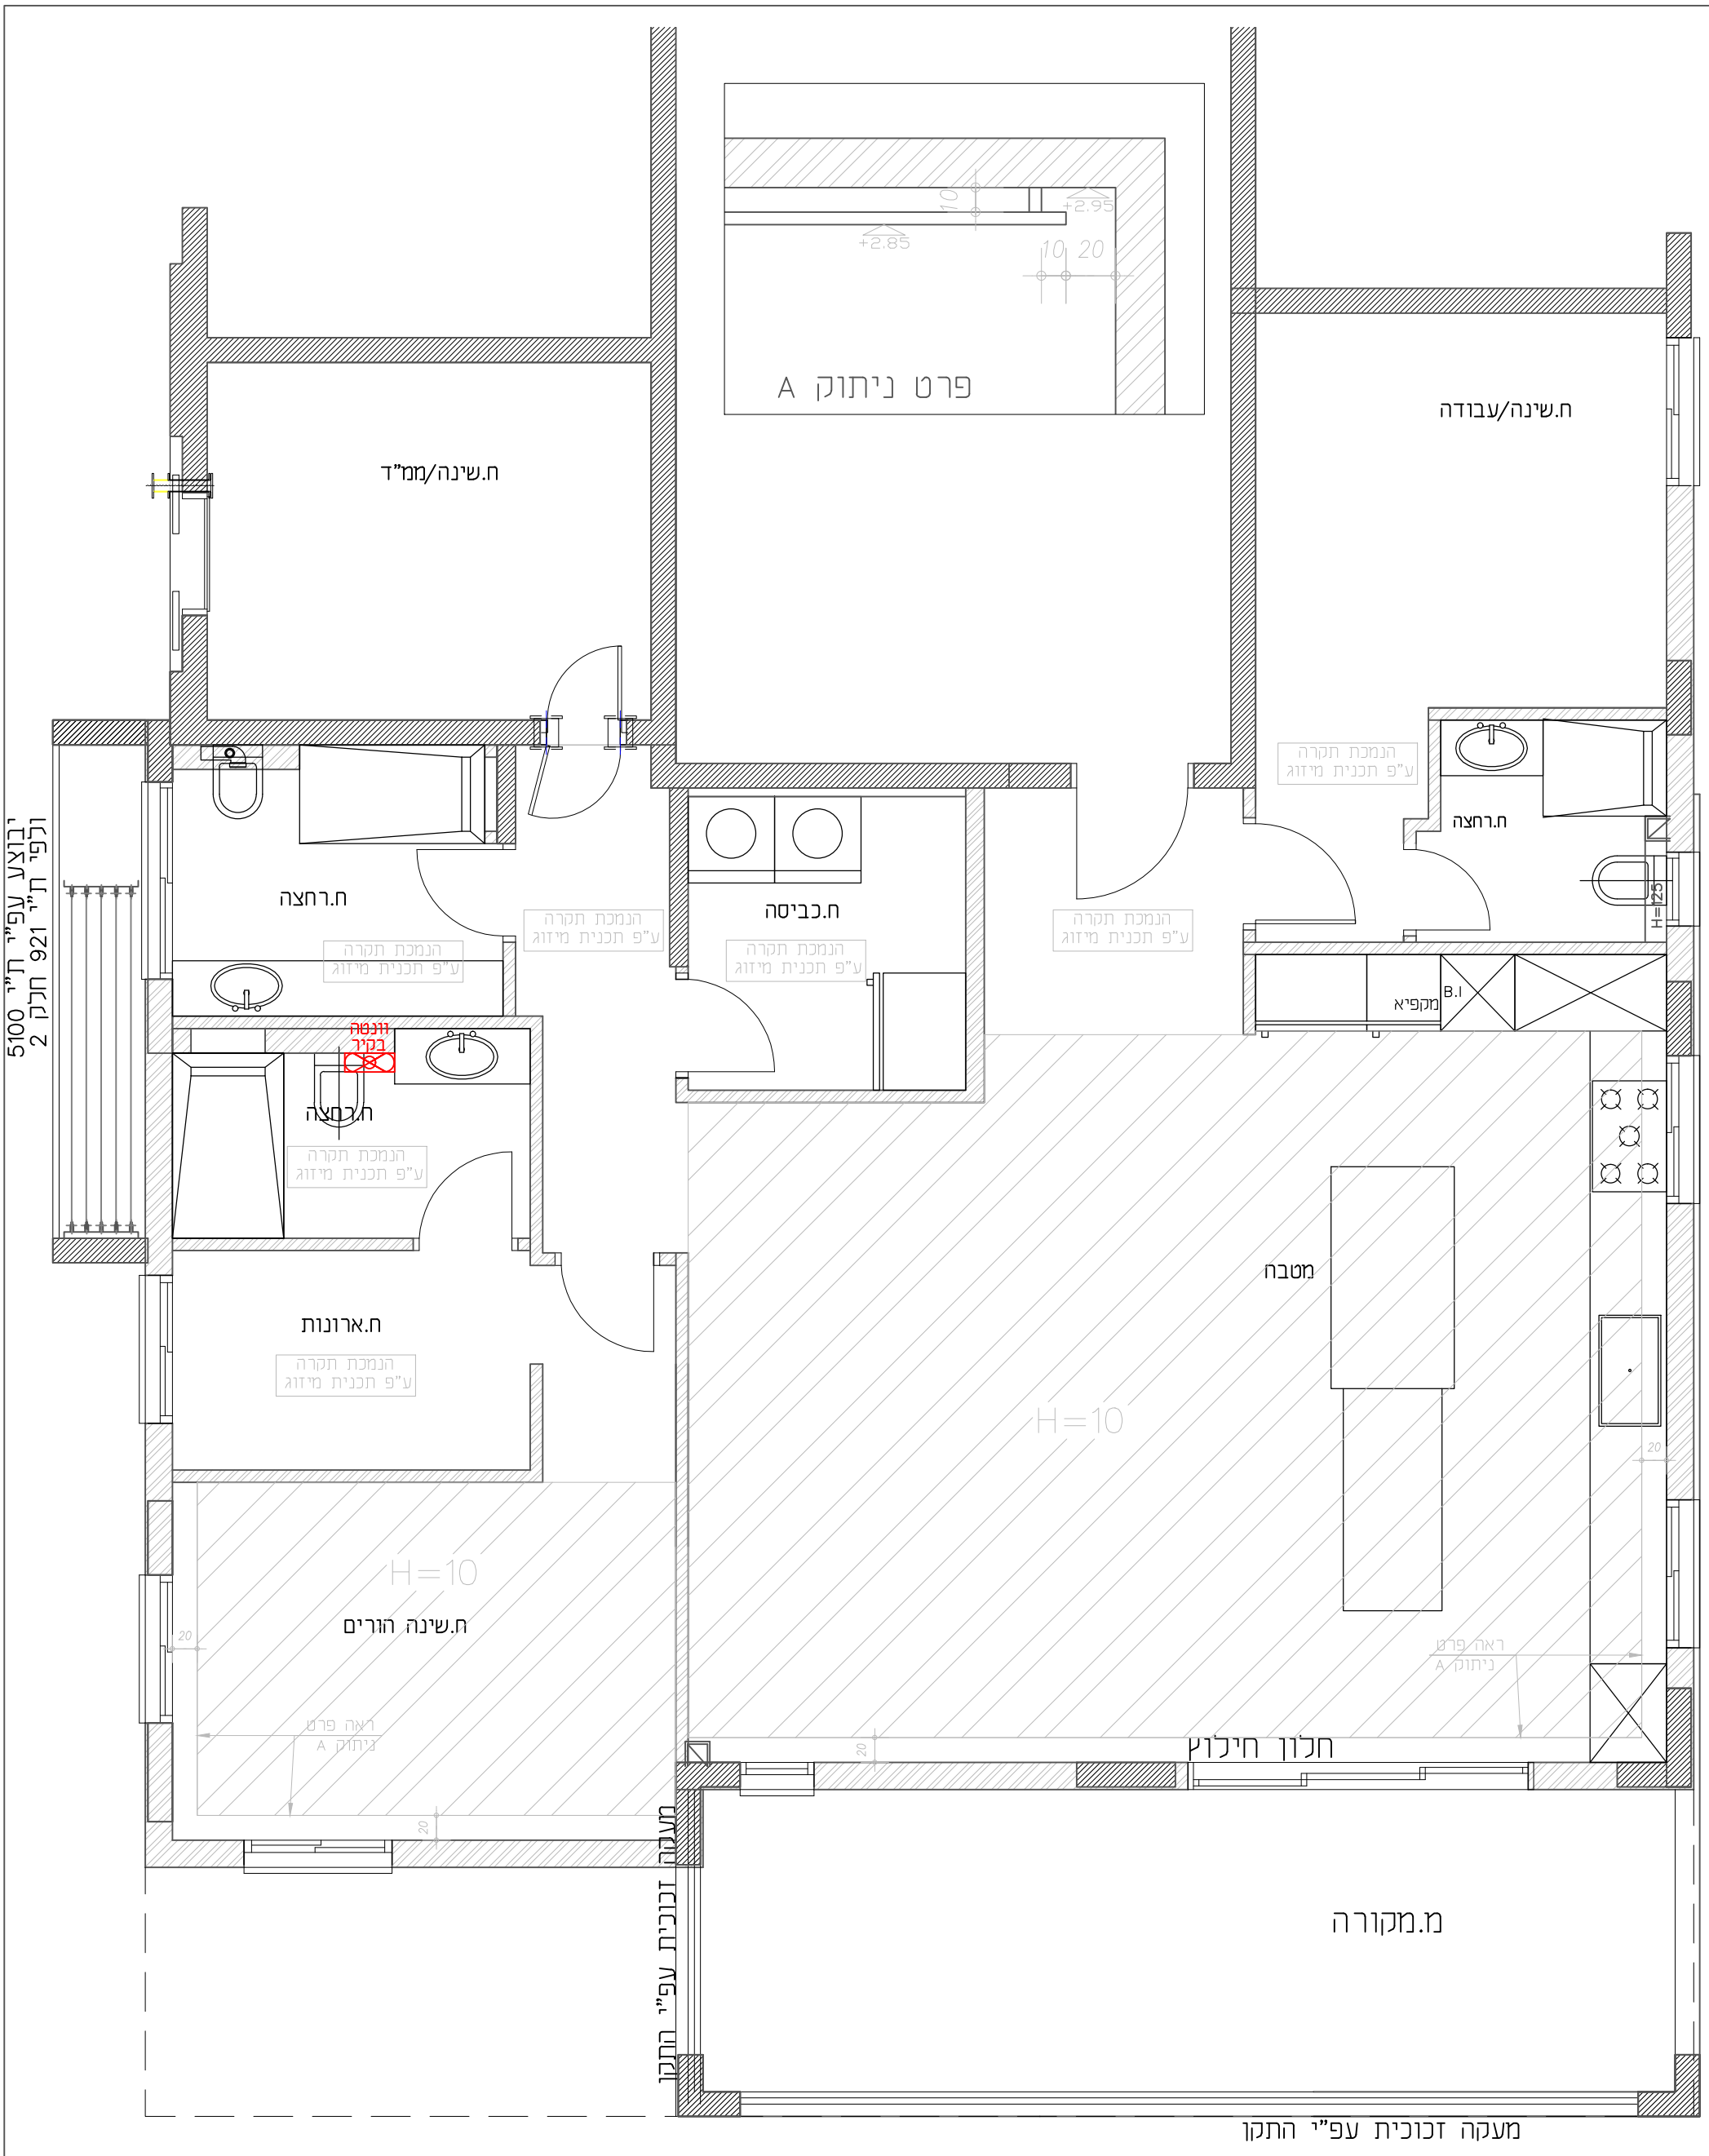

לקוח: סטאחי דורון ושרי	תכנית: הנמכות				חתימת לקוח לאישור תכנית:	
כתובת: האמהות 7–9 רחובות	גיליון מס': 5	גודל גיליון: A3	תאריך: 12.1.26	קנ"מ: 1:50	○ לעיון ● לאישור ○ למכרז ○ לביצוע	MAYA COHEN GOLDMAN INTERIOR DESIGN

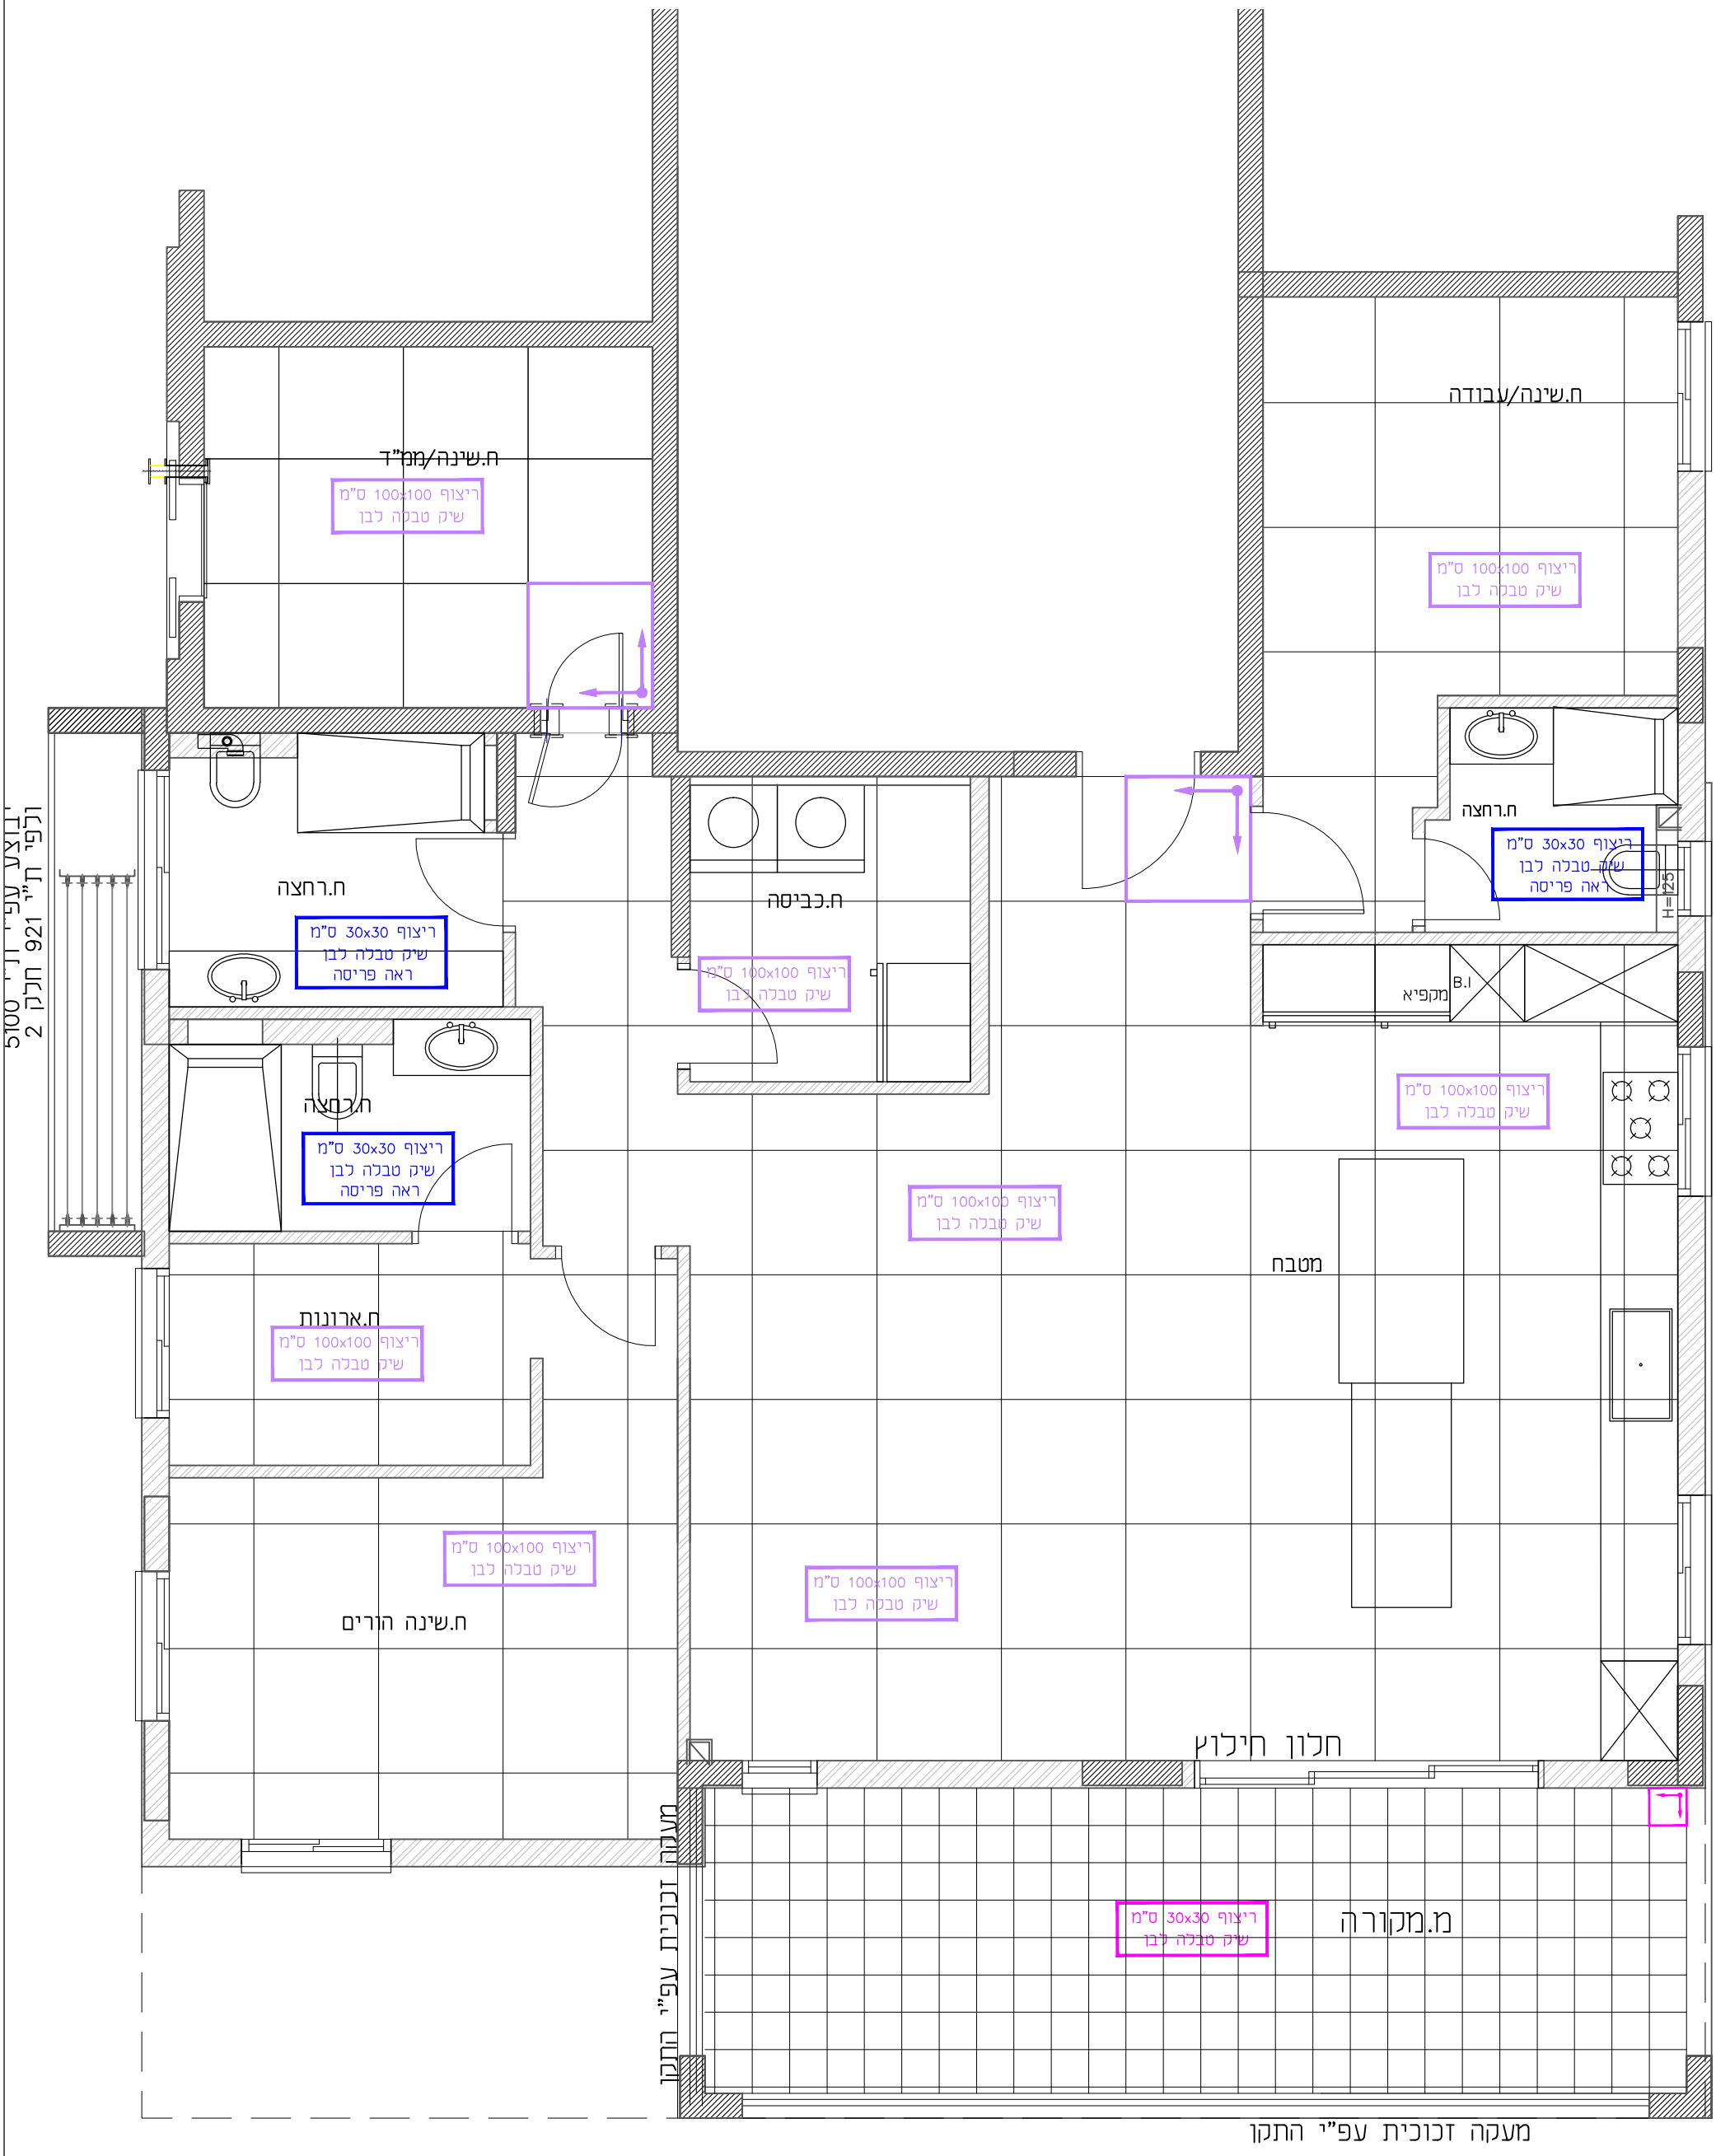


MAYA COHEN GOLDMAN
INTERIOR DESIGN

לקוח: סטאחי דורון ושרי	תכנית: ריצוף	חתימת לקוח לאישור תכנית: _____			
כתובת: האמהות 7–9 רחובות	גיליון מס': 6	גודל גיליון: A3	תאריך: 12.1.26	קנ"מ: 1:50	○ לעיון ● לאישור ○ למכרז ○ לביצוע


חדר רחצה כללי

ריצוף

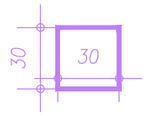


ריצוף R10/11 30*30
שיק טבלה לבן מט


חיפוי

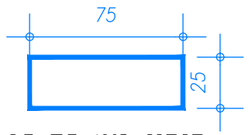


חיפוי מט 25*75
שיק טבלה לבן מט
חיפוי עד לגובה
הנמכה H=275

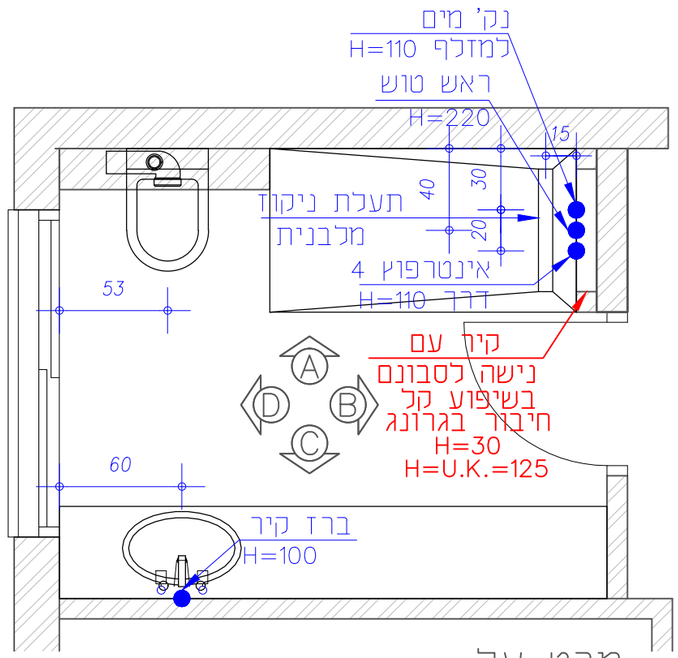


מבט על

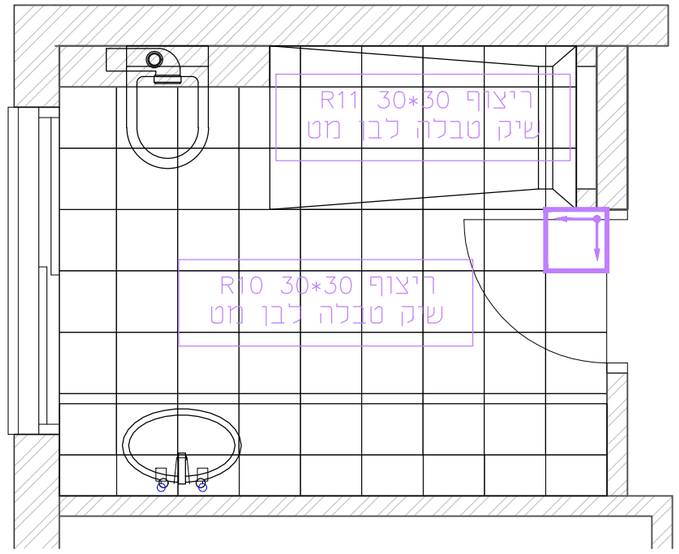


ריצוף

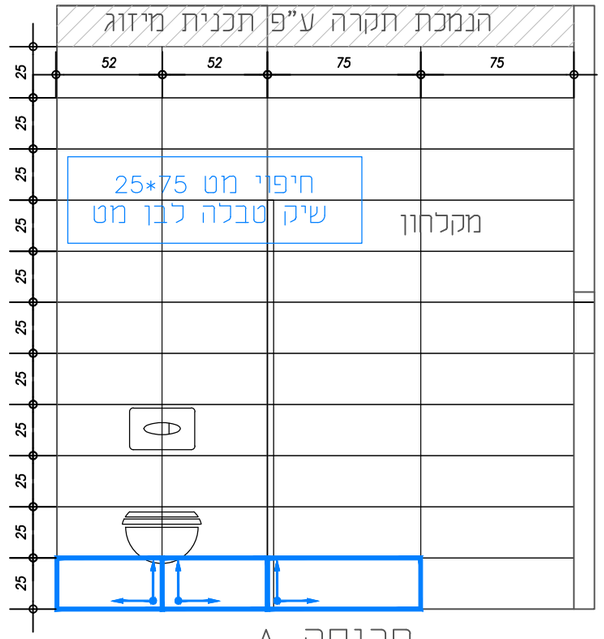


פריסה A

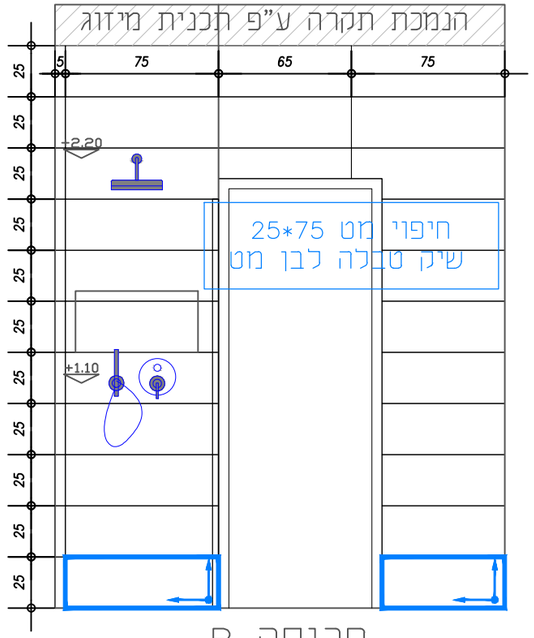

פריסה B

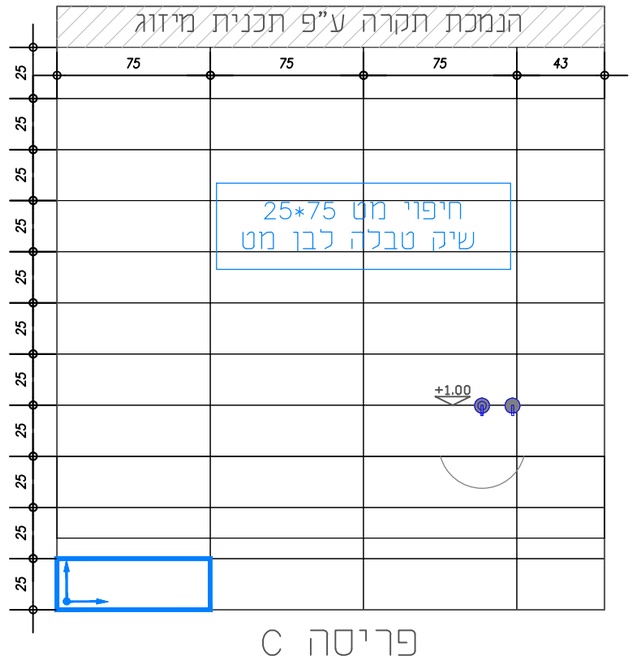


פריסה C

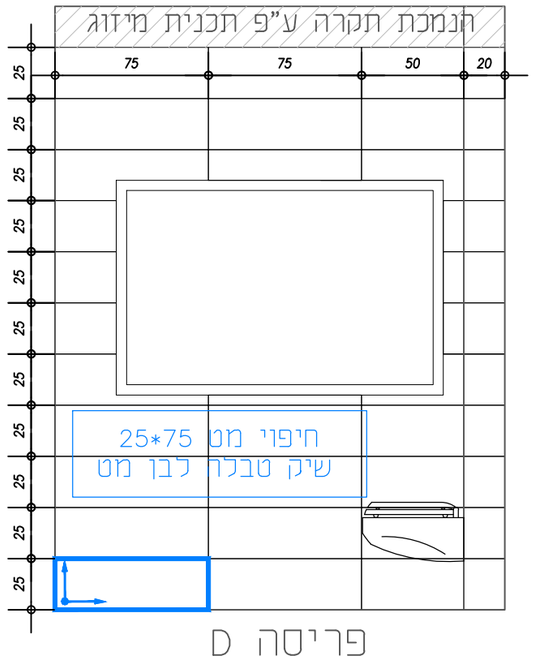


פריסה D


לקוח: סטאחי דורון ושרי	תכנית: פריסת ח.רחצה כללי
כתובת: האמהות 7–9 רחובות	גיליון מס': 9 · גודל גיליון: A3 · תאריך: 12.1.26 · קנ"מ: 1:30
חתימת לקוח לאישור תכנית: _____	○ לעיון ● לאישור ○ למכרז ○ לביצוע
מקרא: ריצוף · חיפוי	MAYA COHEN GOLDMAN INTERIOR DESIGN

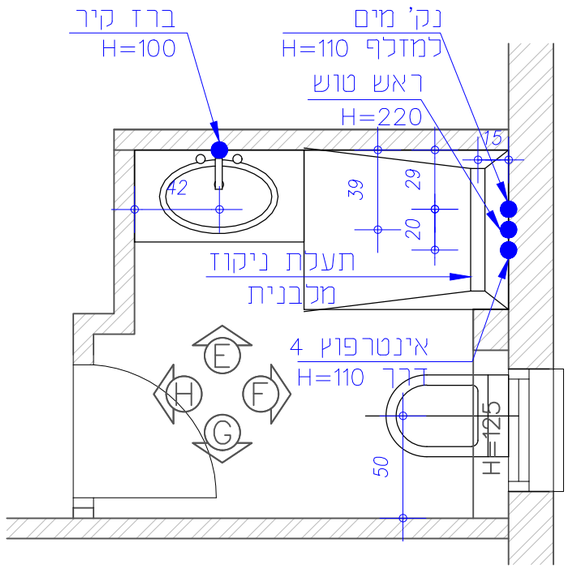


מבט על

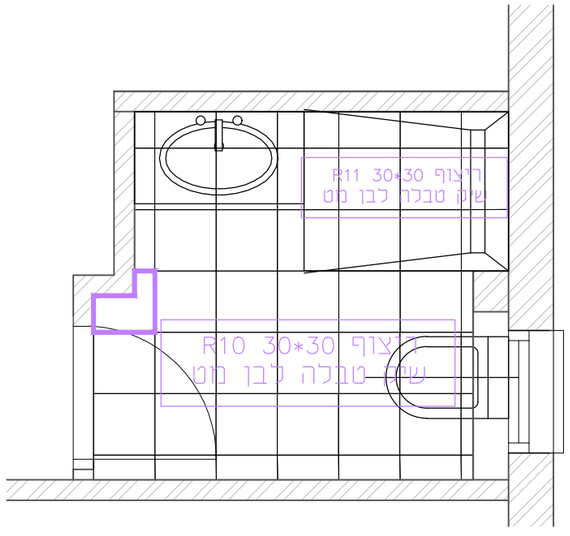


ריצוף

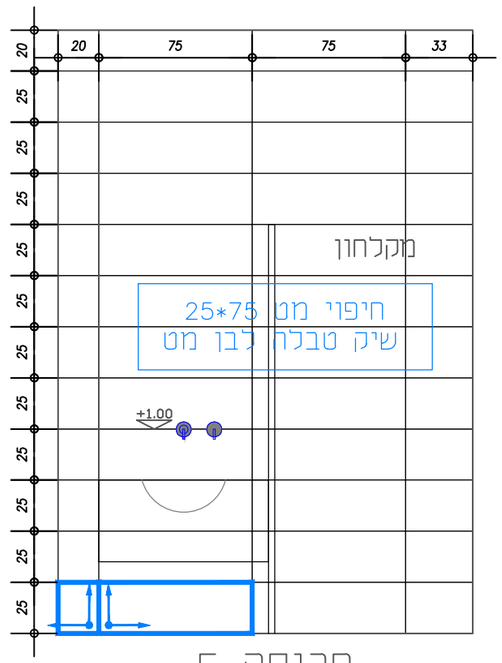


פריסה E

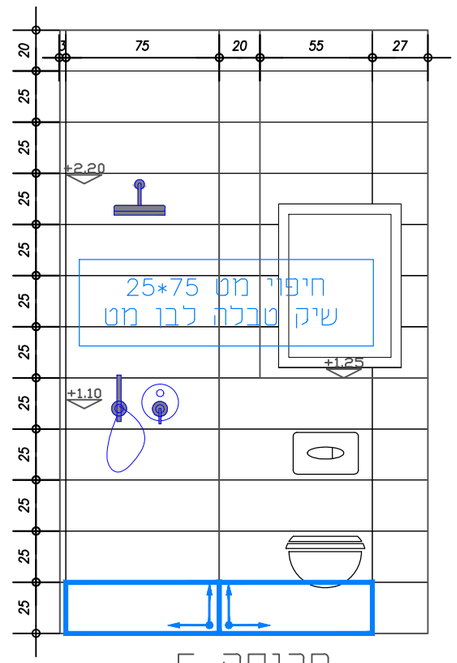

פריסה F

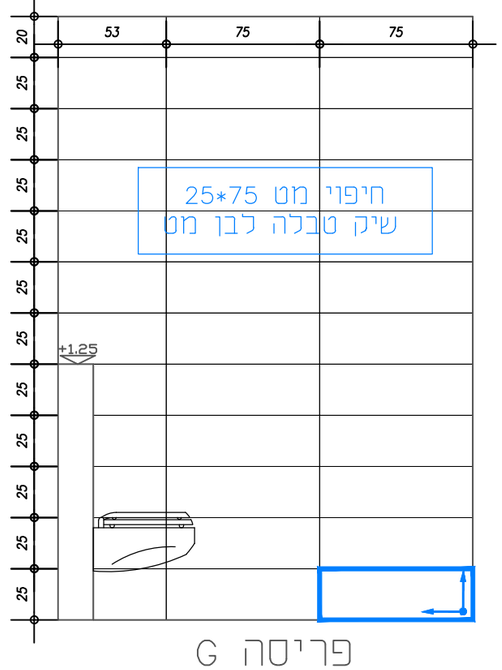

פריסה G

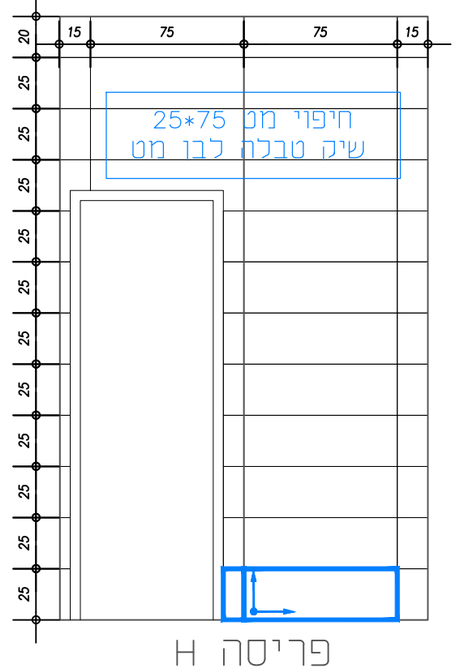


פריסה H

חדר רחצה אורחים
ריצוף
ריצוף R10/11 30*30 שיק טבלה לבן מט
חיפוי
 חיפוי מט 25*75 שיק טבלה לבן מט חיפוי עד לתקרה H=295

לקוח: סטאחי דורון ושרי	תכנית: פריסת ח.רחצה אורחים
כתובת: האמהות 7–9 רחובות	גיליון מס': 9 / גודל גיליון: A3 / תאריך: 12.1.26 / קנ"מ: 1:30
חתימת לקוח לאישור תכנית: _____	○ לעיון ● לאישור ○ למכרז ○ לביצוע
מקרא: ריצוף / חיפוי	MAYA COHEN GOLDMAN INTERIOR DESIGN


חדר רחצה הורים

ריצוף

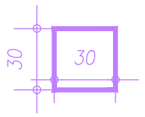


ריצוף R10/11 30*30
שיק טבלה לבן מט


חיפוי

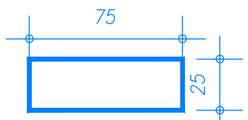


חיפוי מט 25*75
שיק טבלה לבן מט
חיפוי עד לגובה
הנמכה H=245

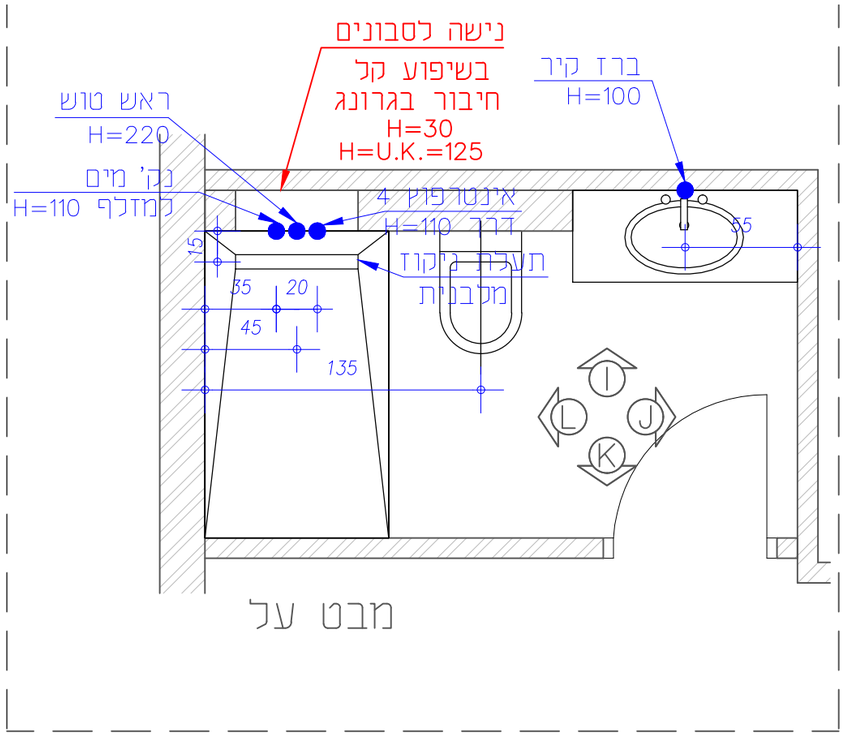


מבט על

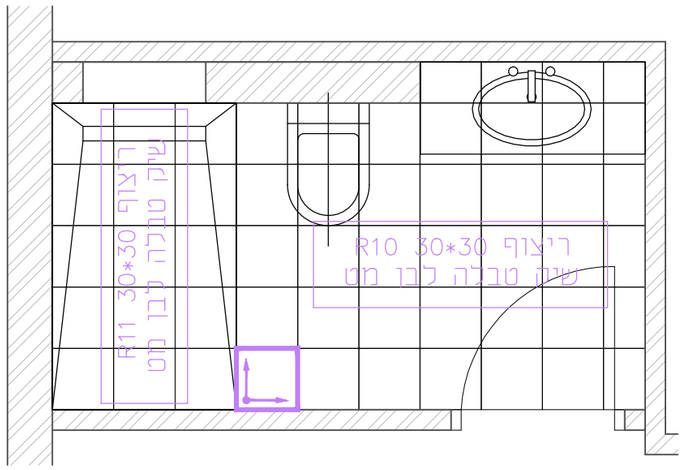


ריצוף

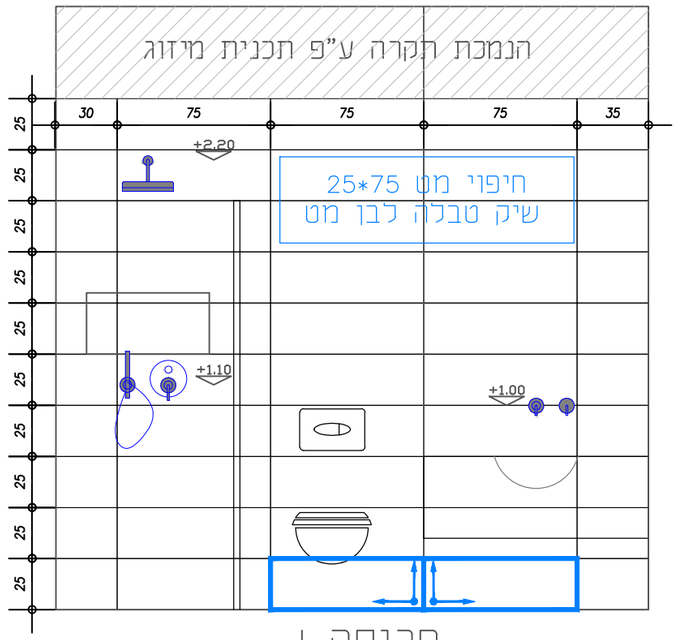

פריסה I

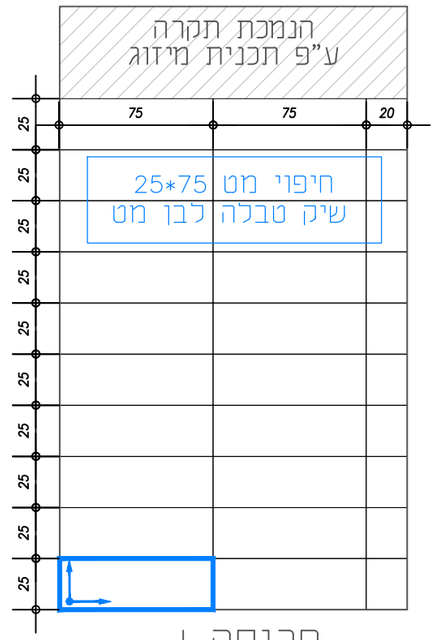

פריסה J

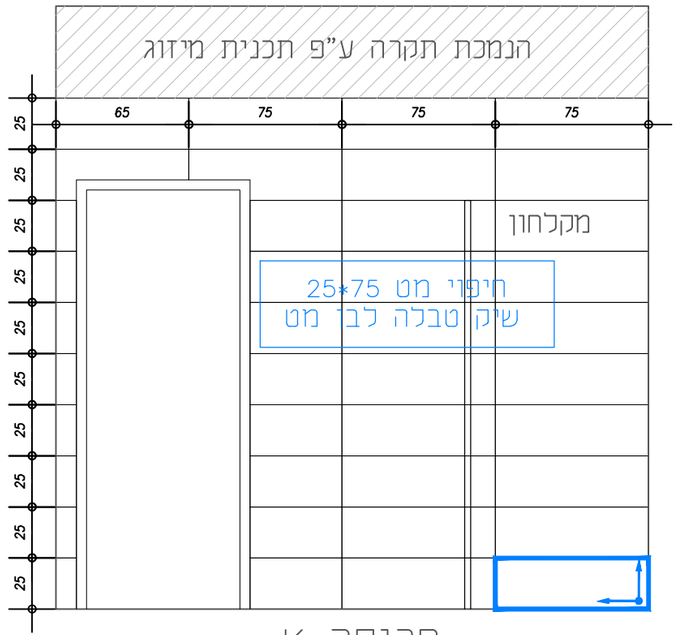


פריסה K




פריסה L

לקוח: סטאחי דורון ושרי	תכנית: פריסת ח.רחצה הורים
כתובת: האמהות 9–7 רחובות	גיליון מס': 9 · גודל גיליון: A3 · תאריך: 12.1.26 · קנ"מ: 1:30
חתימת לקוח לאישור תכנית: _____	○ לעיון ● לאישור ○ למכרז ○ לביצוע
מקרא: ריצוף · חיפוי	


MAYA COHEN GOLDMAN
INTERIOR DESIGN

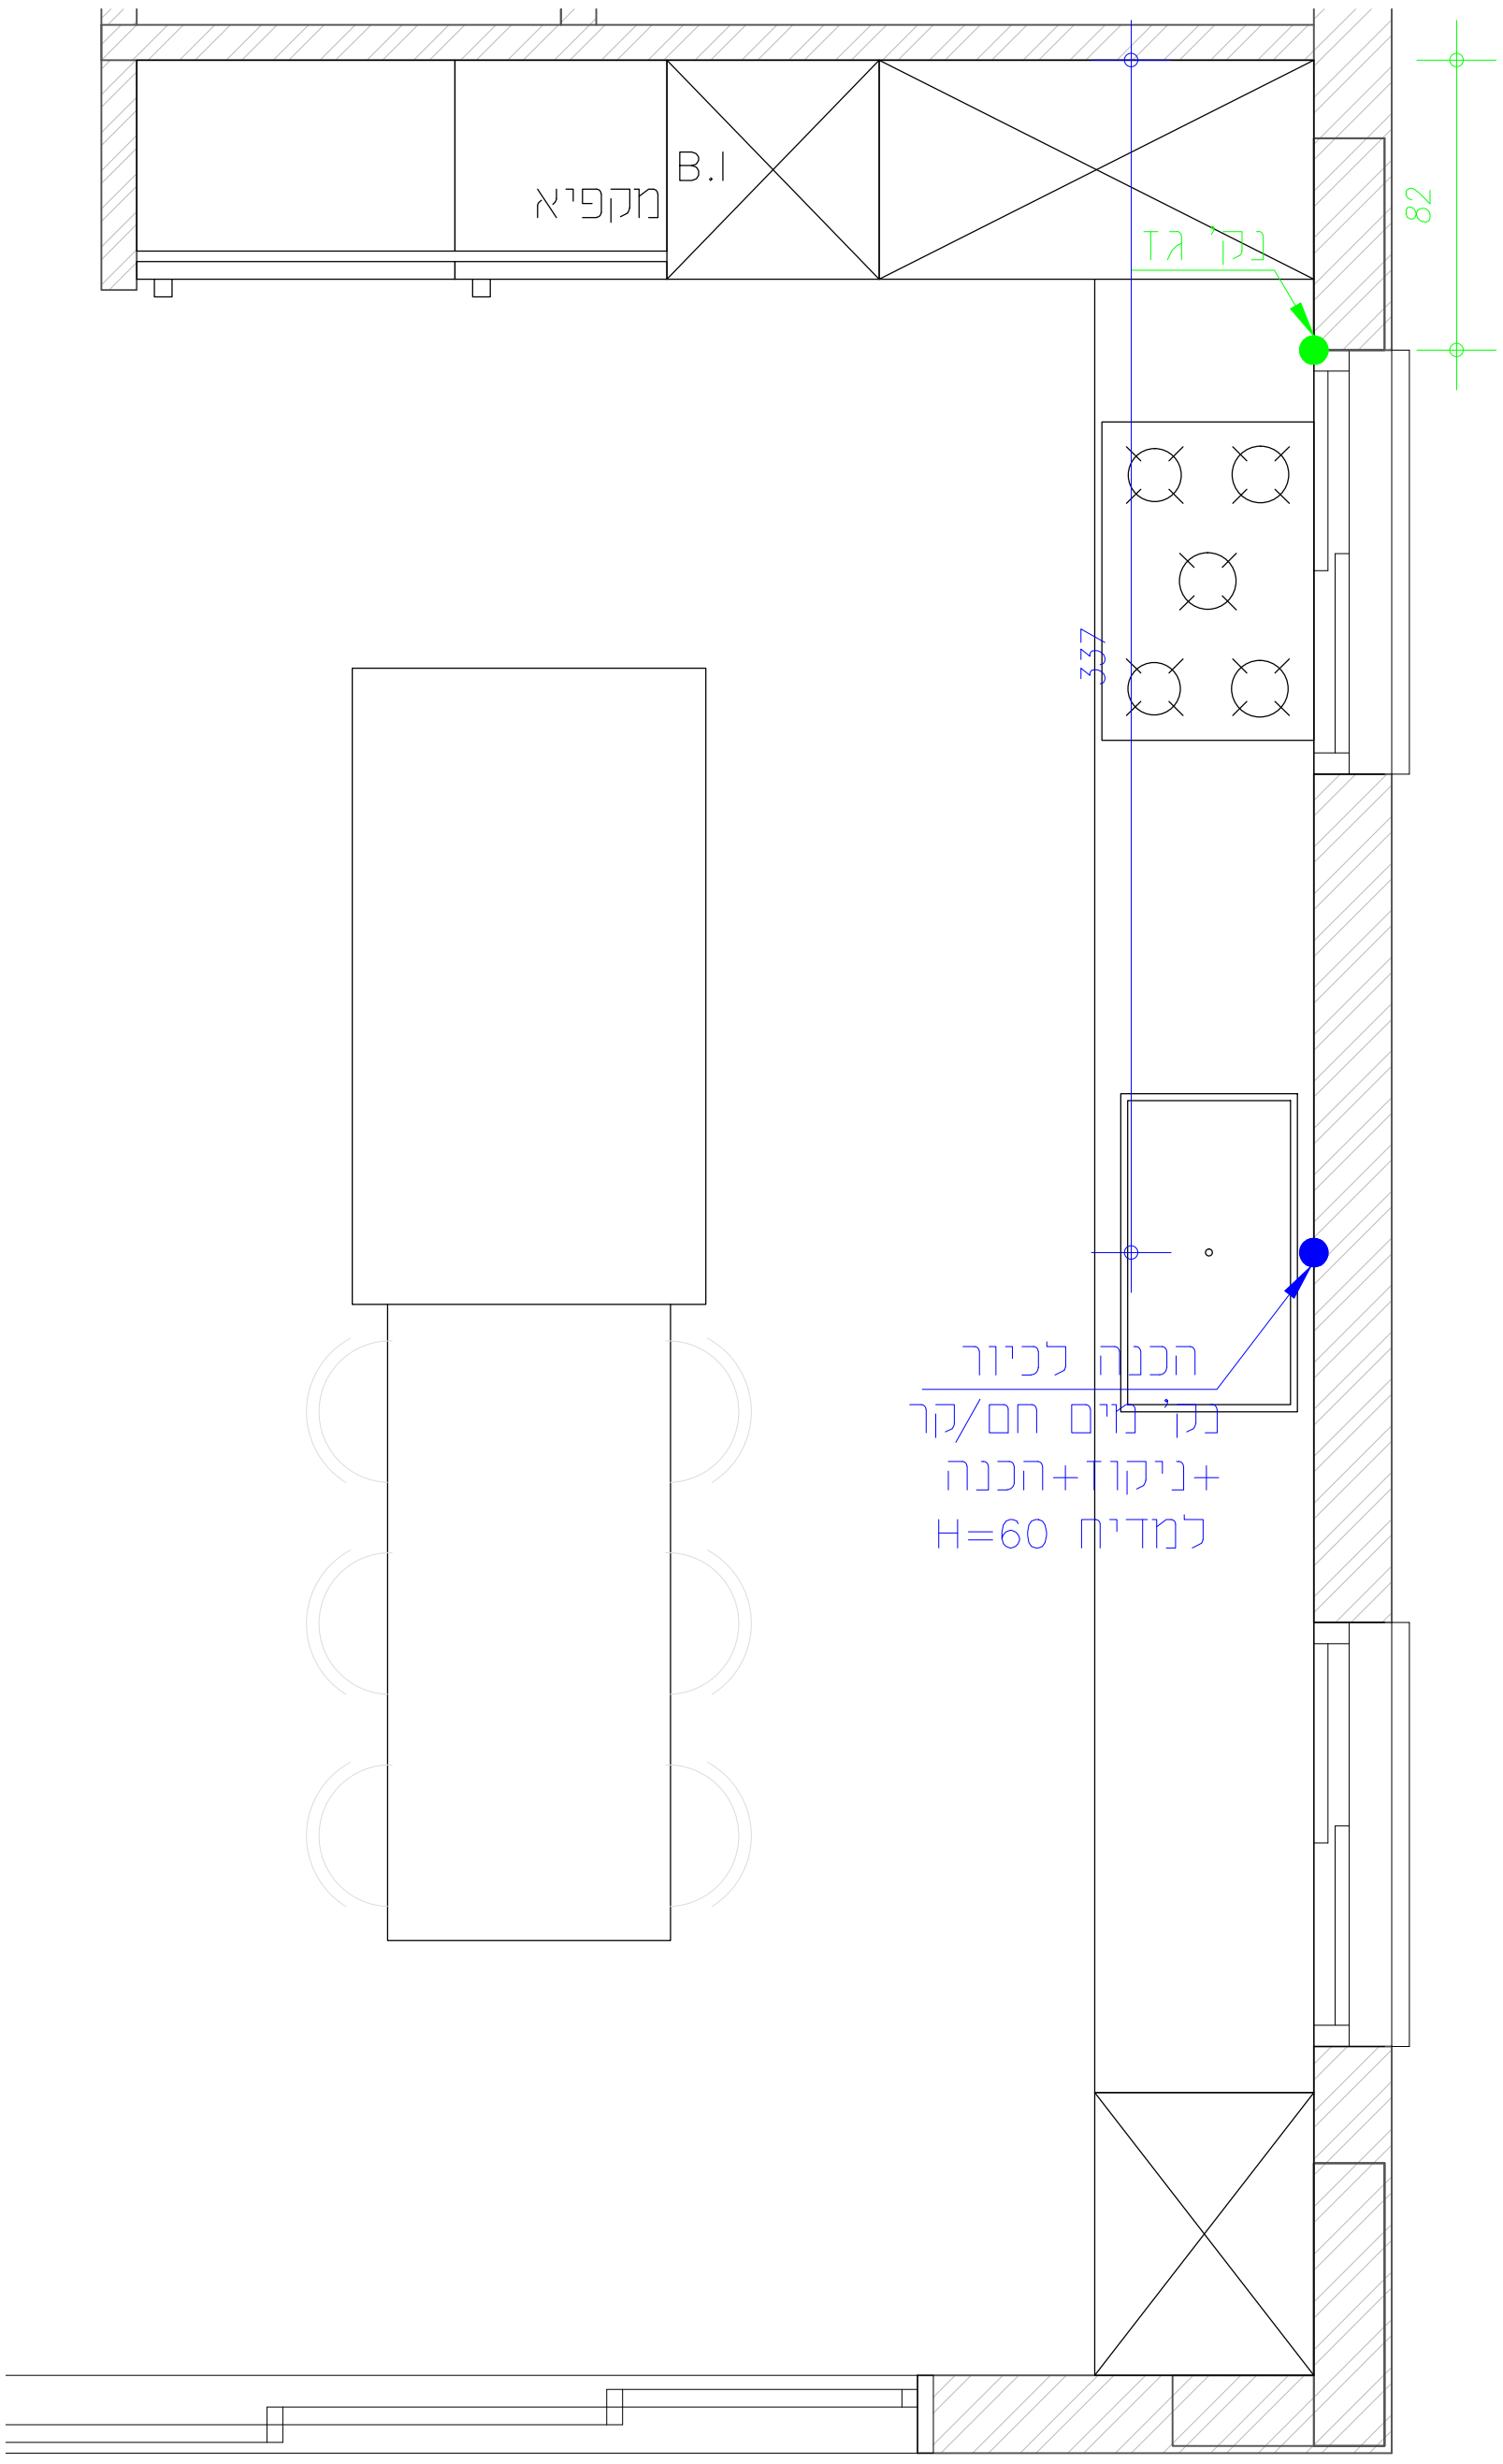

MAYA COHEN GOLDMAN INTERIOR DESIGN	חתימת לקוח לאישור תכנית: _____		תכנית: מטבח–אינסטלציה			לקוח: סטאחי דורון ושרי
	○ לעיון ● לאישור ○ למכרז ○ לביצוע	קנ"מ: 1:50	תאריך: 12.1.26	גודל גיליון: A3	גיליון מס': 6	כתובת: האמהות 7–9 רחובות

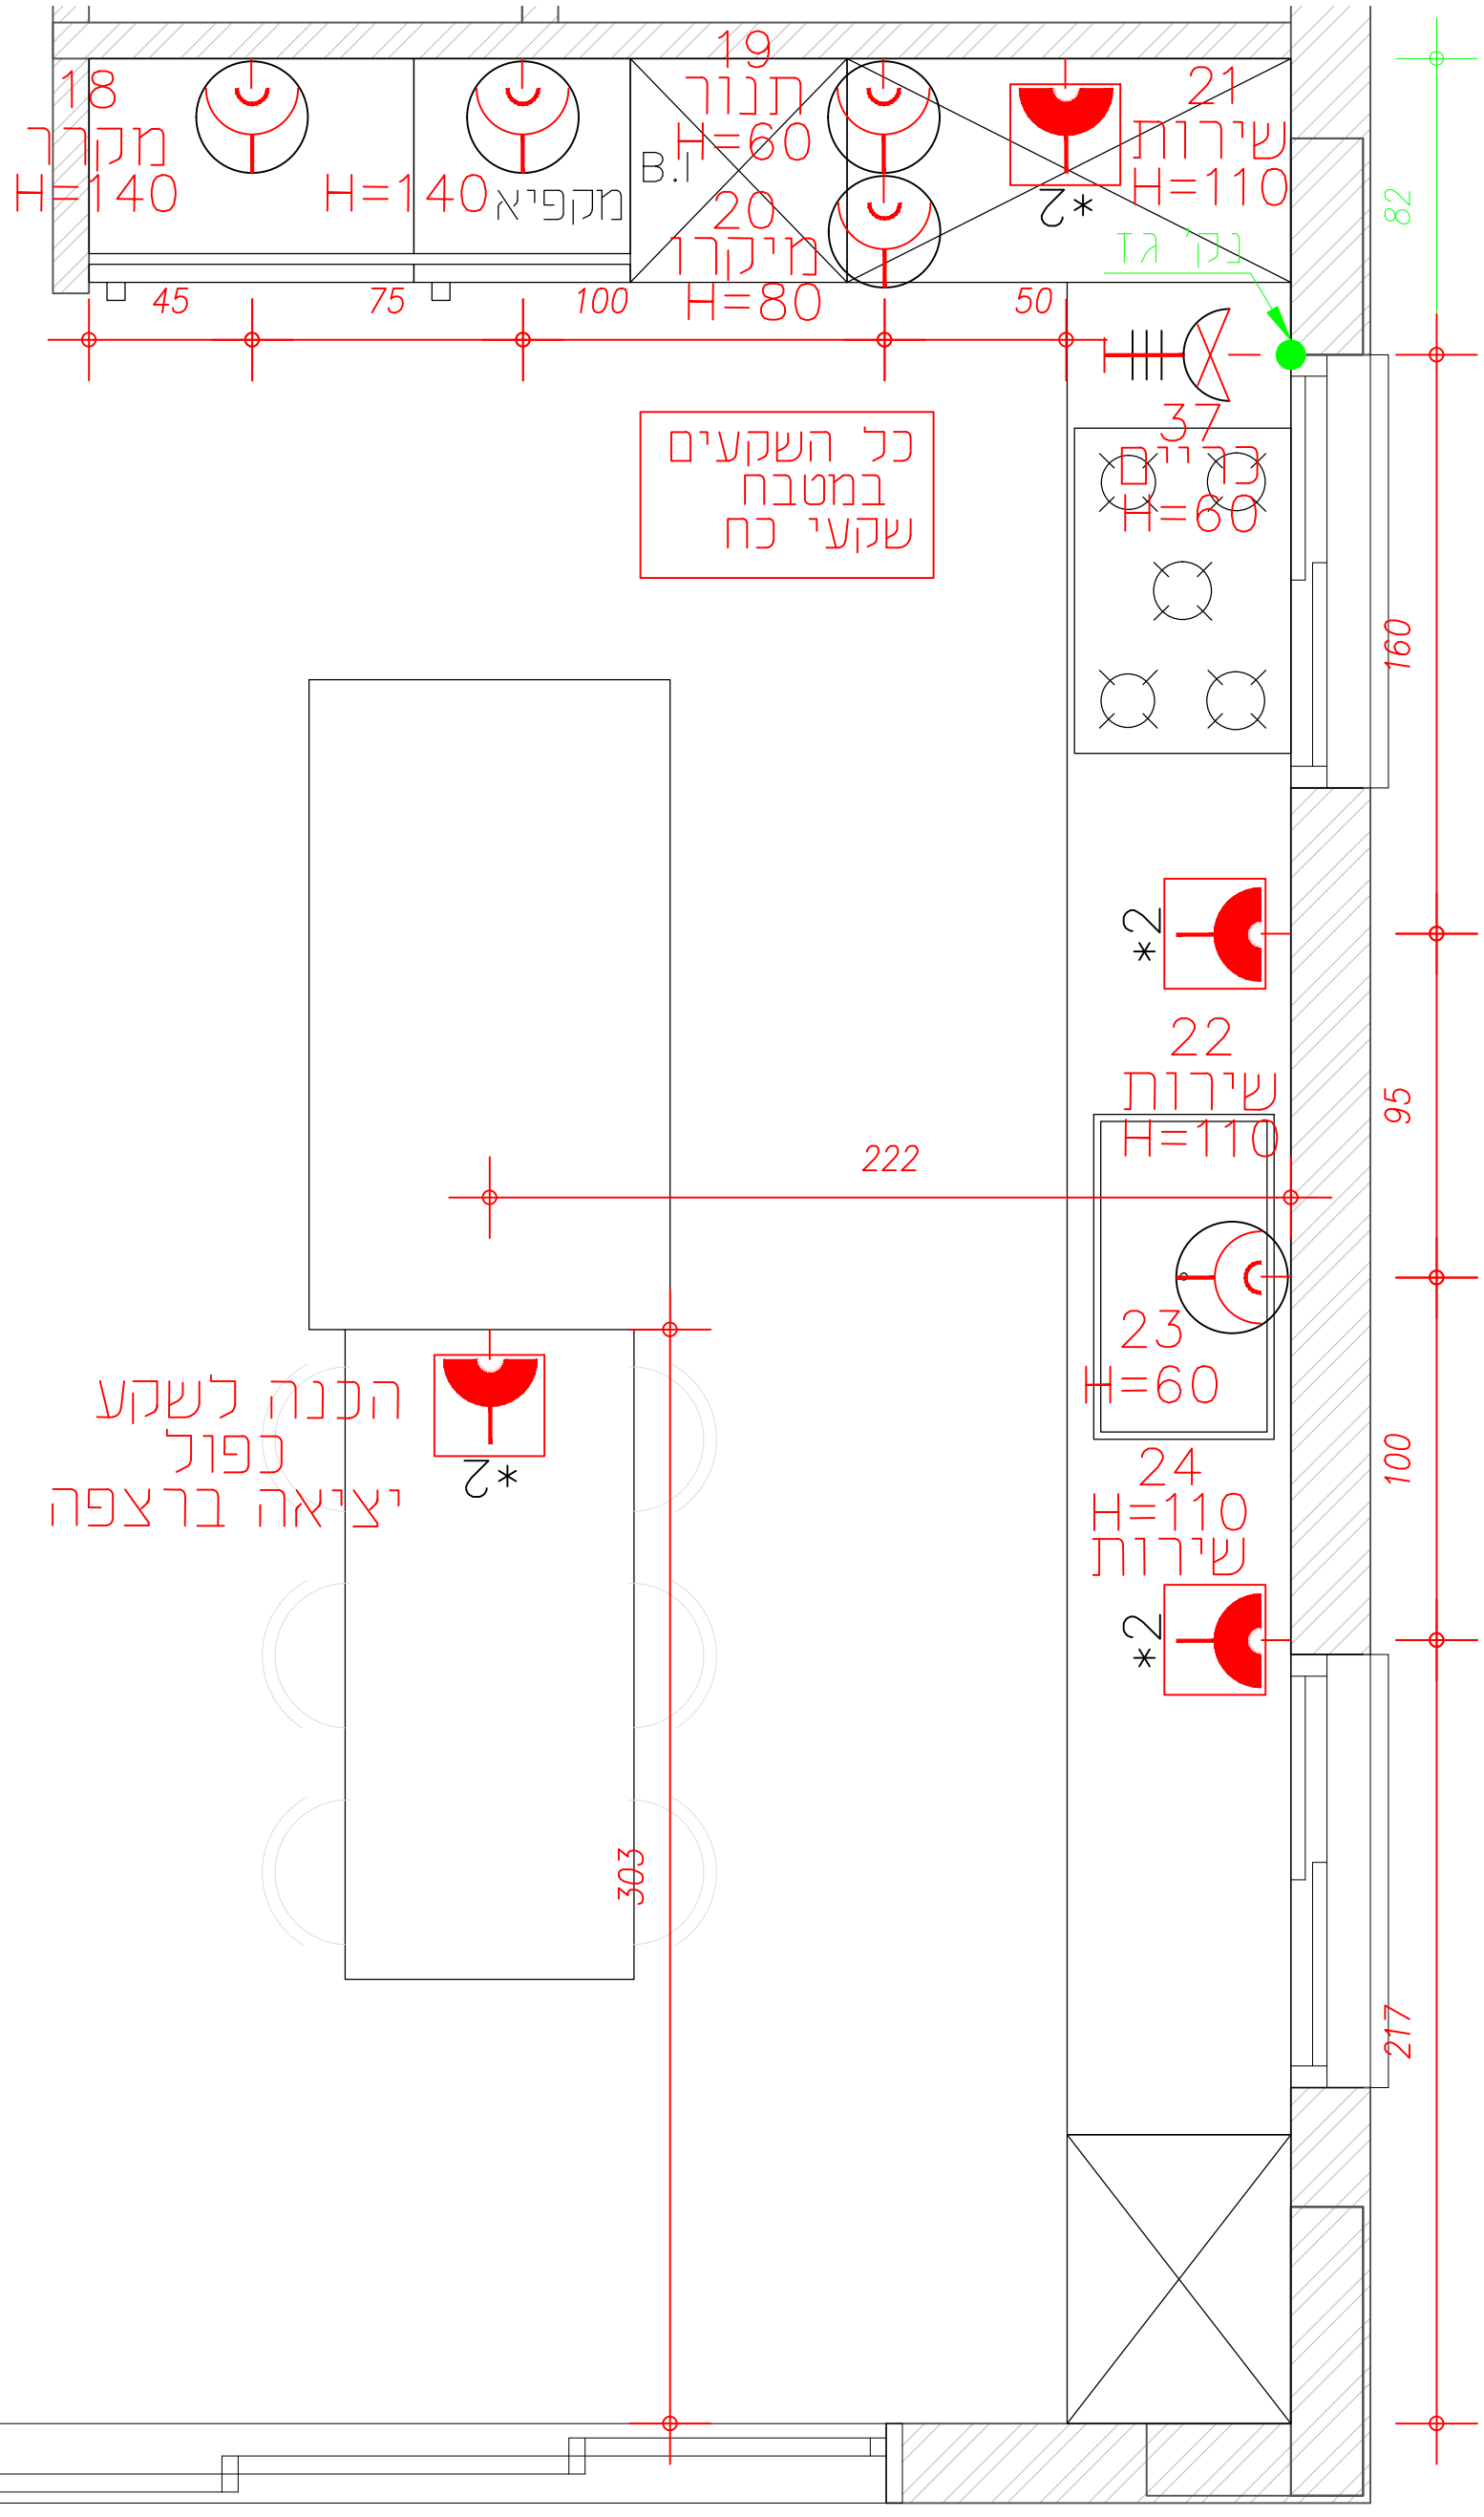

MAYA COHEN GOLDMAN INTERIOR DESIGN	חתימת לקוח לאישור תכנית: _____ ○ לעיון ● לאישור ○ למכרז ○ לביצוע	תכנית: מטבח–חשמל				לקוח: סטאחי דורון ושרי
		קנ"מ: 1:50	תאריך: 12.1.26	גודל גיליון: A3	גיליון מס': 6	כתובת: האמהות 7–9 רחובות

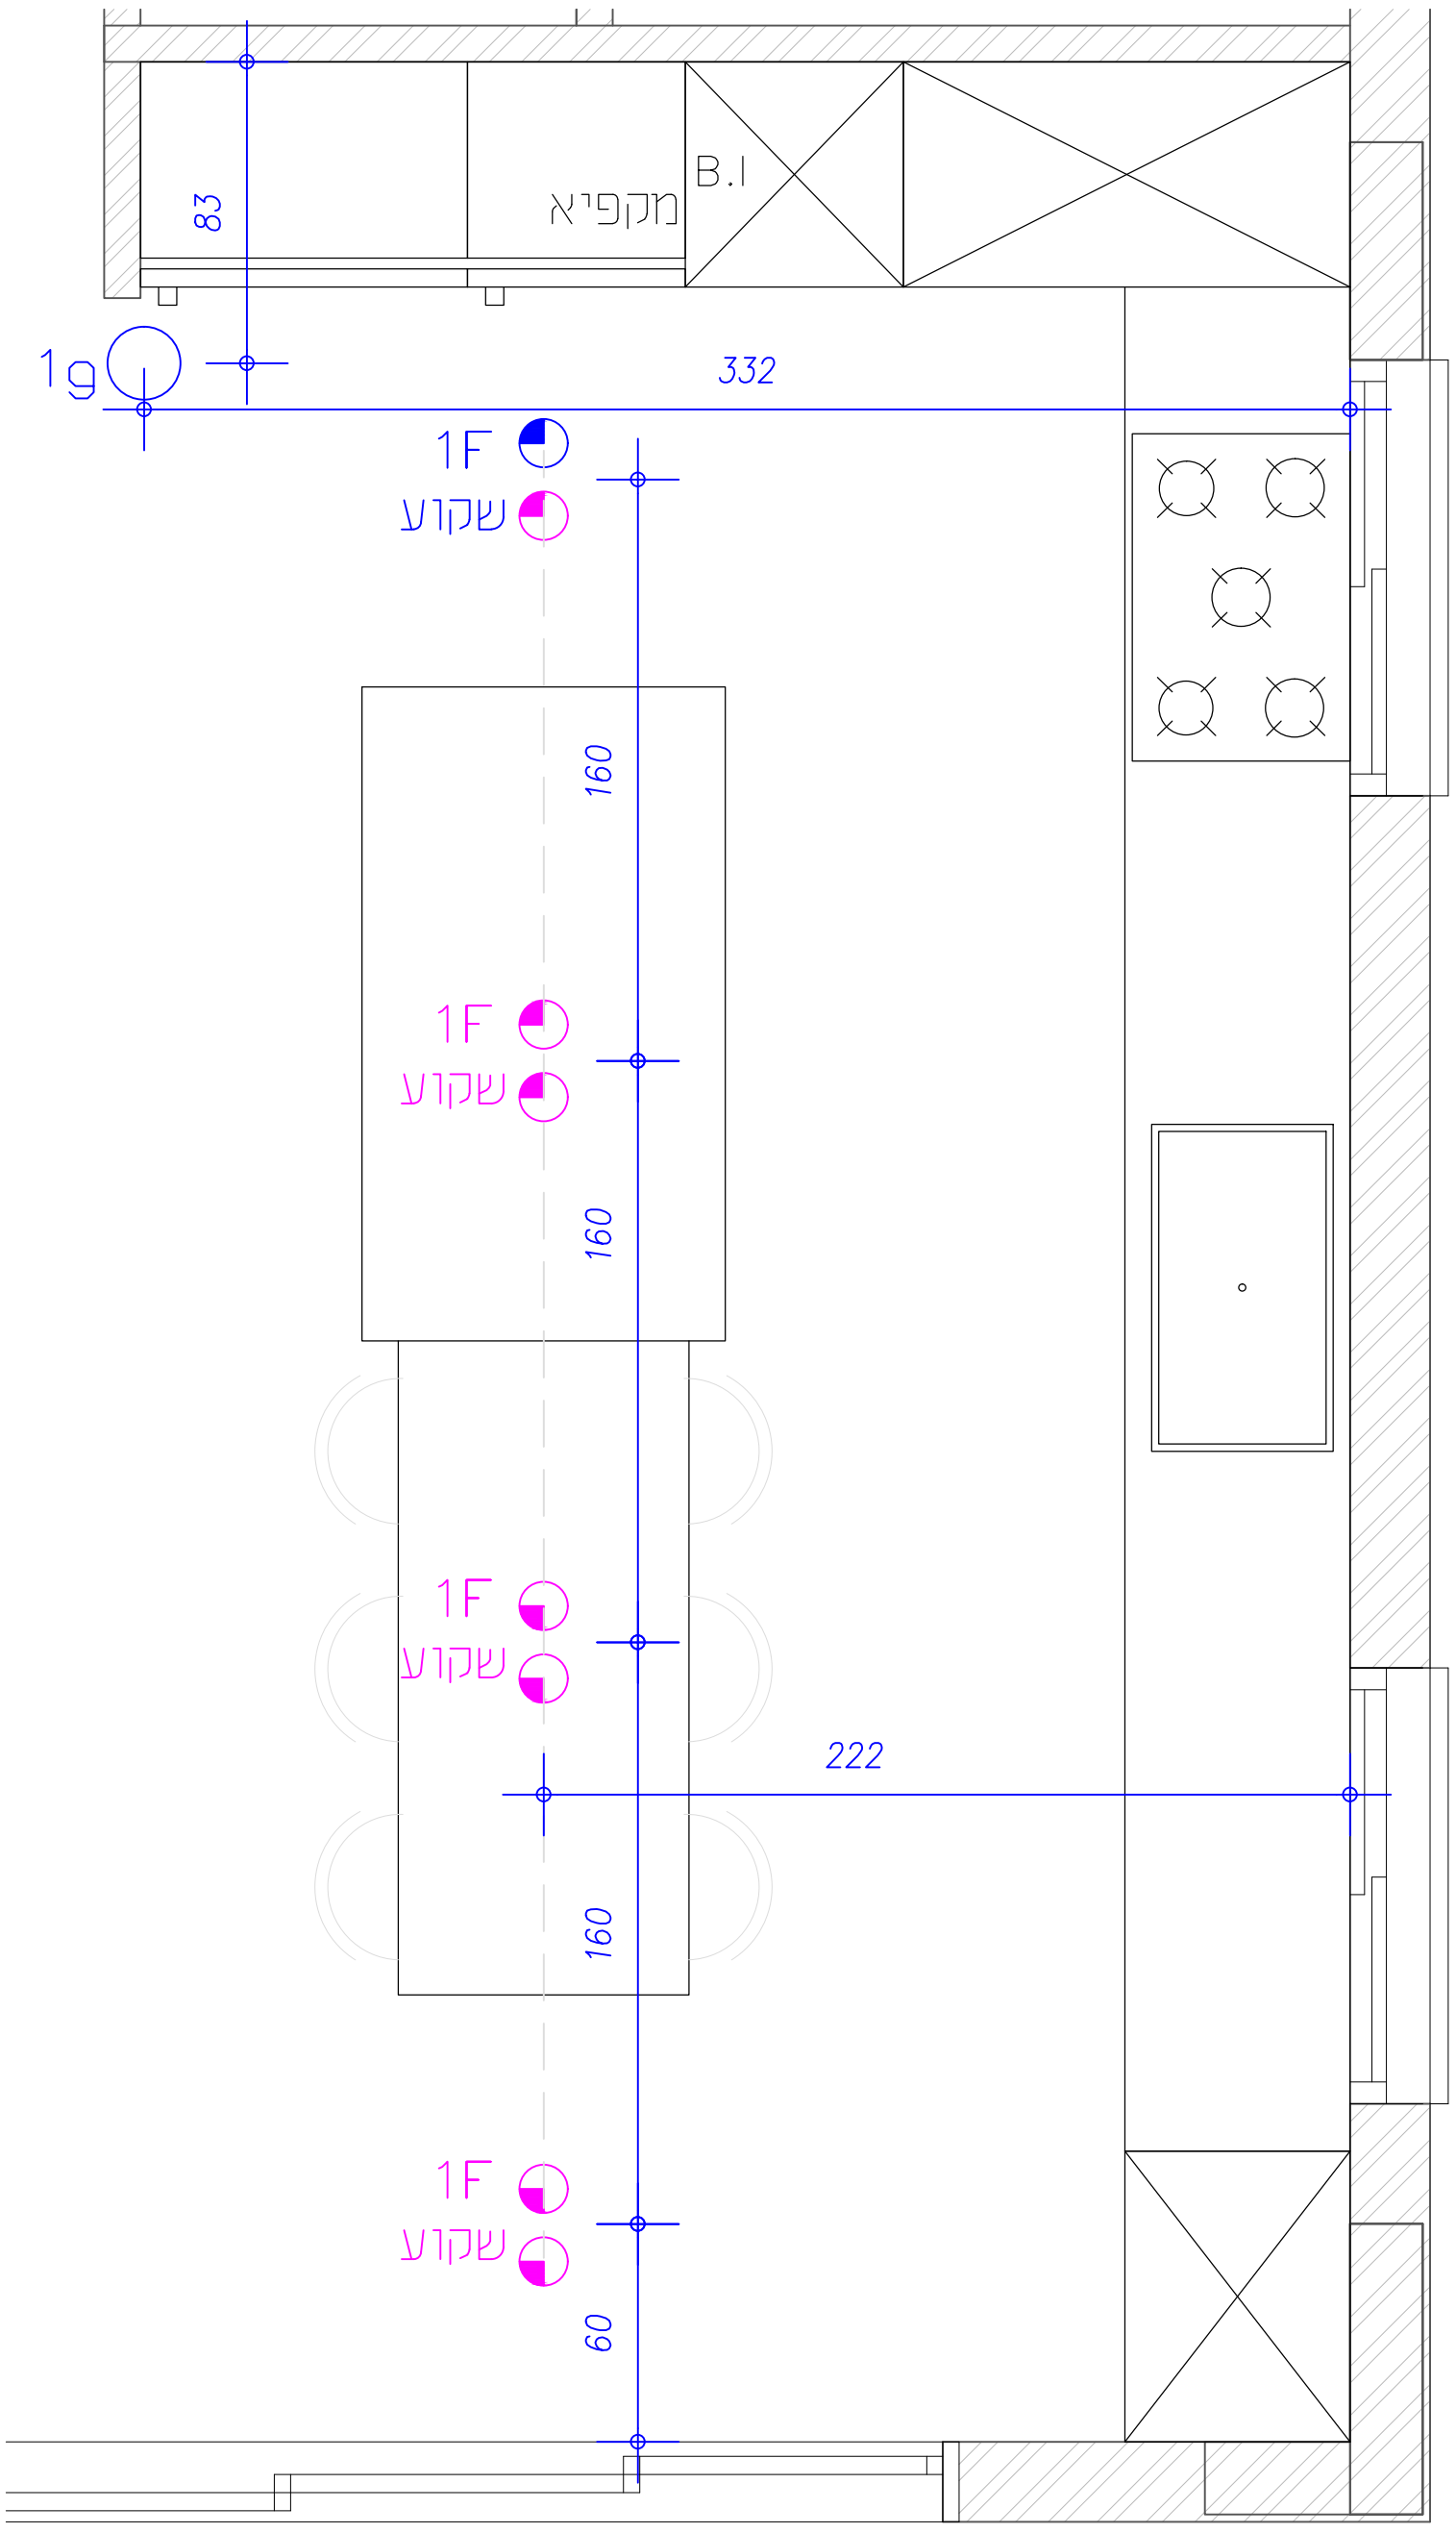

לקוח: סטאחי דורון ושרי	תכנית: מטבח–חשמל				חתימת לקוח לאישור תכנית:	
כתובת: האמהות 7–9 רחובות	גיליון מס': 6	גודל גיליון: A3	תאריך: 12.1.26	קנ"מ: 1:50	○ לעיון ● לאישור	○ למכרז ○ לביצוע

MAYA COHEN GOLDMAN
INTERIOR DESIGN