


רח' יהודה הנשיא

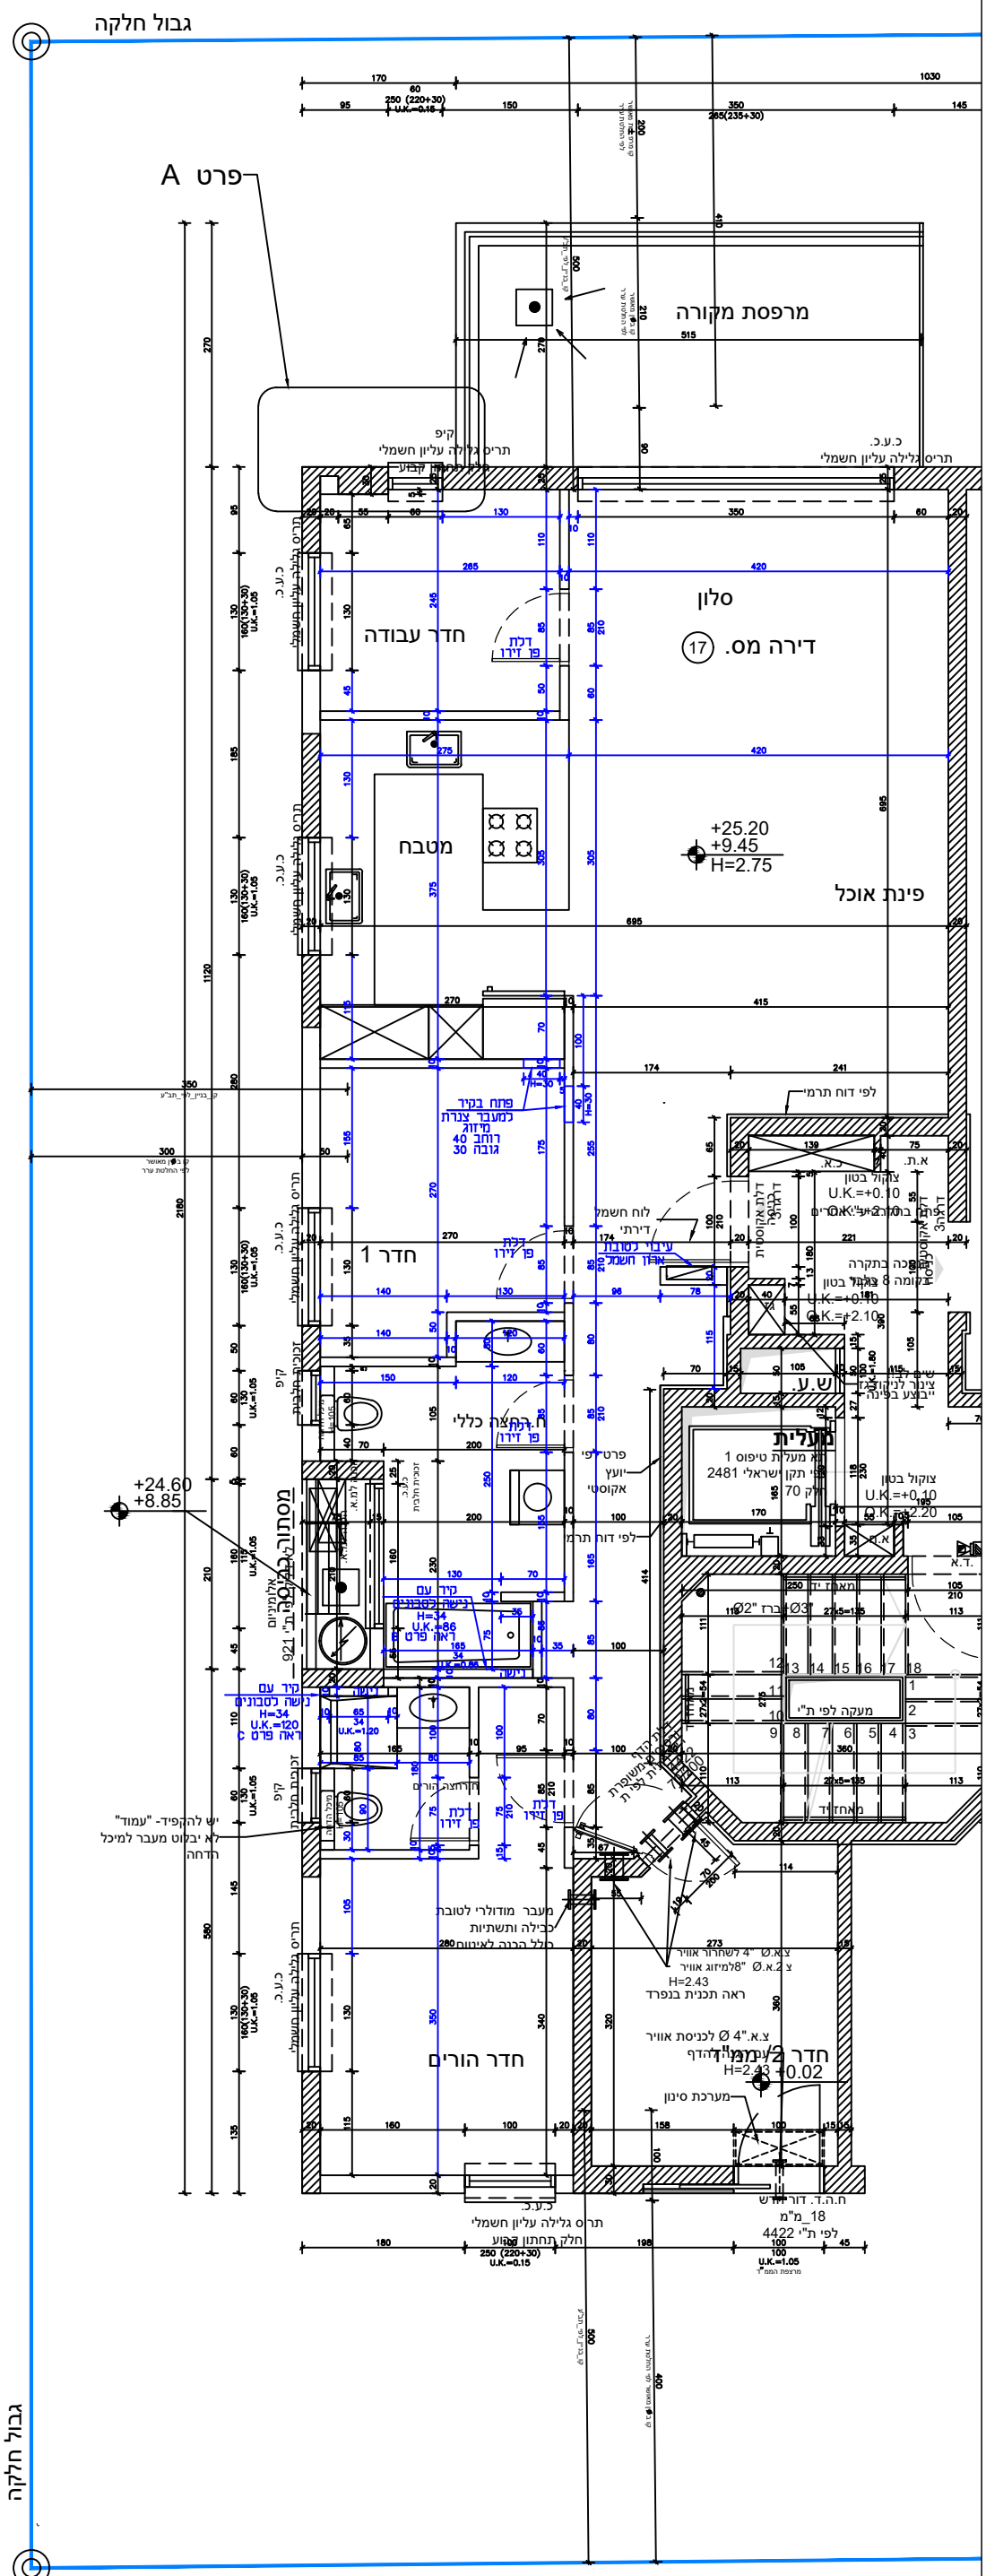

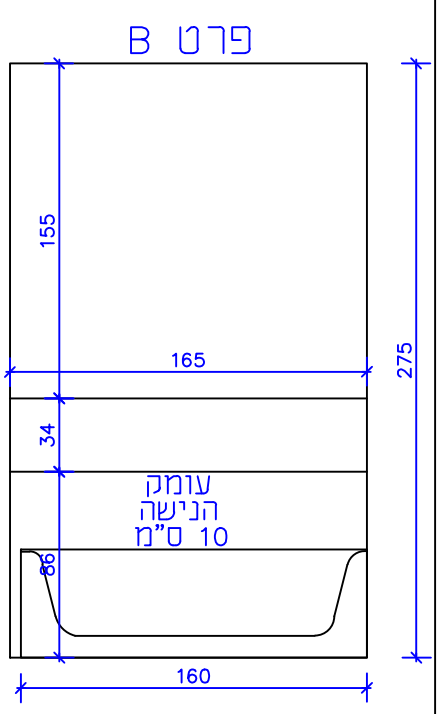

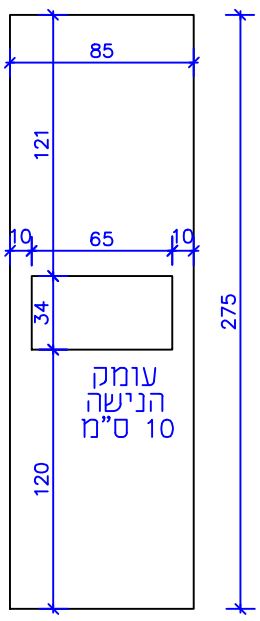

לקוח:
מרדכי וחגית פוגל

תכנית:
בינוי

כתובת:
יהודה הנשיא 12 דירה 17

גיליון מס':	גודל גיליון:	תאריך:	קנ"מ:
1	A3	4.5.26	1:75

חתימת לקוח לאישור תכנית:

_____

● לעיון ○ לאישור
○ למכרז ○ לביצוע

הערות:
1. על המבצע לבדוק את התאמת התכנית בשטח, לפני הבניה, ולבקר את המידות. על כל טעות ו/או אי התאמה יש לעדכן משרד מתכנן.
2. אין לקבוע מידות ע"פ שרטוט. המידות המחייבות הן המידות שנמדדו בשטח לאחר ביצוע.
3. המידות בתכנית הן ברוטו –ללא חיפוי גמר.
4. יתכנו שינויים בהתאם להוראות הביצוע הסופי.
5. כל התכניות נשארות רכוש המתכנן: אין לעשות בהן שימוש ללא אישור בכתב המתכנן.
6. כל ההערות תקפות אלא אם צוין אחרת.

RK
RUTH KOLSKY
תכנון - עיצוב - השראה

לקוח:
מרדכי וחגית פוגל


תכנית:
אינסטלציה

כתובת:
יהודה הנשיא 12 דירה 17

גיליון מס':	גודל גיליון:	תאריך:	קנ"מ:
2	A3	4.5.26	1:75

חתימת לקוח לאישור תכנית:

● לעיון ○ לאישור
○ למכרז ○ לביצוע

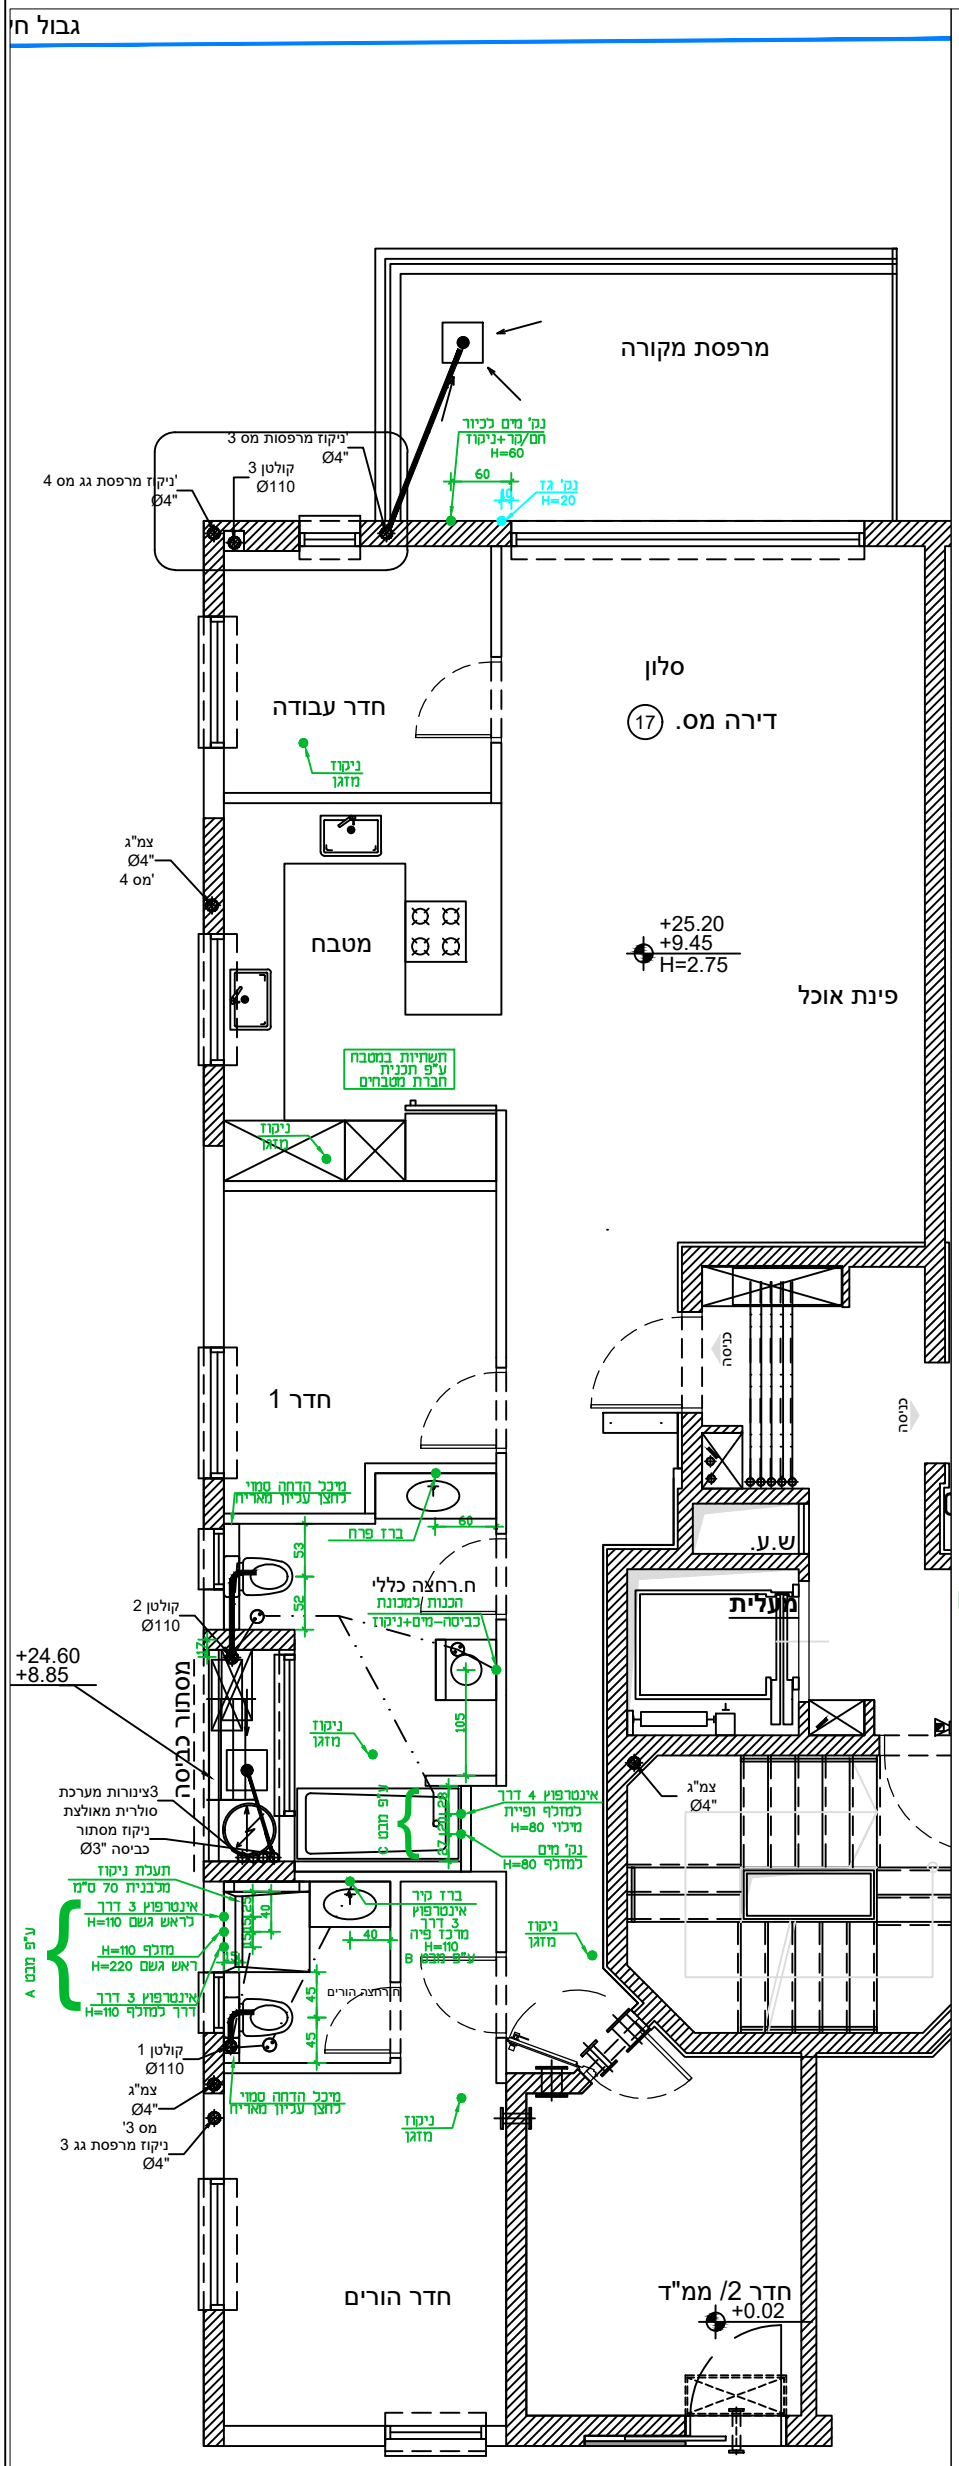

הערות:
1. על המבצע לבדוק את התאמת התכנית בשטח, לפני הבניה, ולבקר את המידות. על כל טעות ו/או אי התאמה יש לעדכן משרד מתכנן.
2. אין לקבוע מידות ע"פ שרטוט. המידות המחייבות הן המידות שנמדדו בשטח לאחר ביצוע.
3. המידות בתכנית הן ברוטו –ללא חיפוי גמר.
4. יתכנו שינויים בהתאם להוראות הביצוע הסופי.
5. כל התכניות נשארות רכוש המתכנן: אין לעשות בהן שימוש ללא אישור בכתב המתכנן.
6. כל ההערות תקפות אלא אם צוין אחרת.

RK
RUTH KOLSKY
תכנון - עיצוב - השראה

לקוח:
מרדכי וחגית פוגל

תכנית:
חשמל

כתובת:
יהודה הנשיא 12 דירה 17

גיליון מס':	גודל גיליון:	תאריך:	קנ"מ:
3	A3	4.5.26	1:75


חתימת לקוח לאישור תכנית:

_____

● לעיון ○ לאישור
○ למכרז ○ לביצוע

רח' יהודה הנשיא

גבול

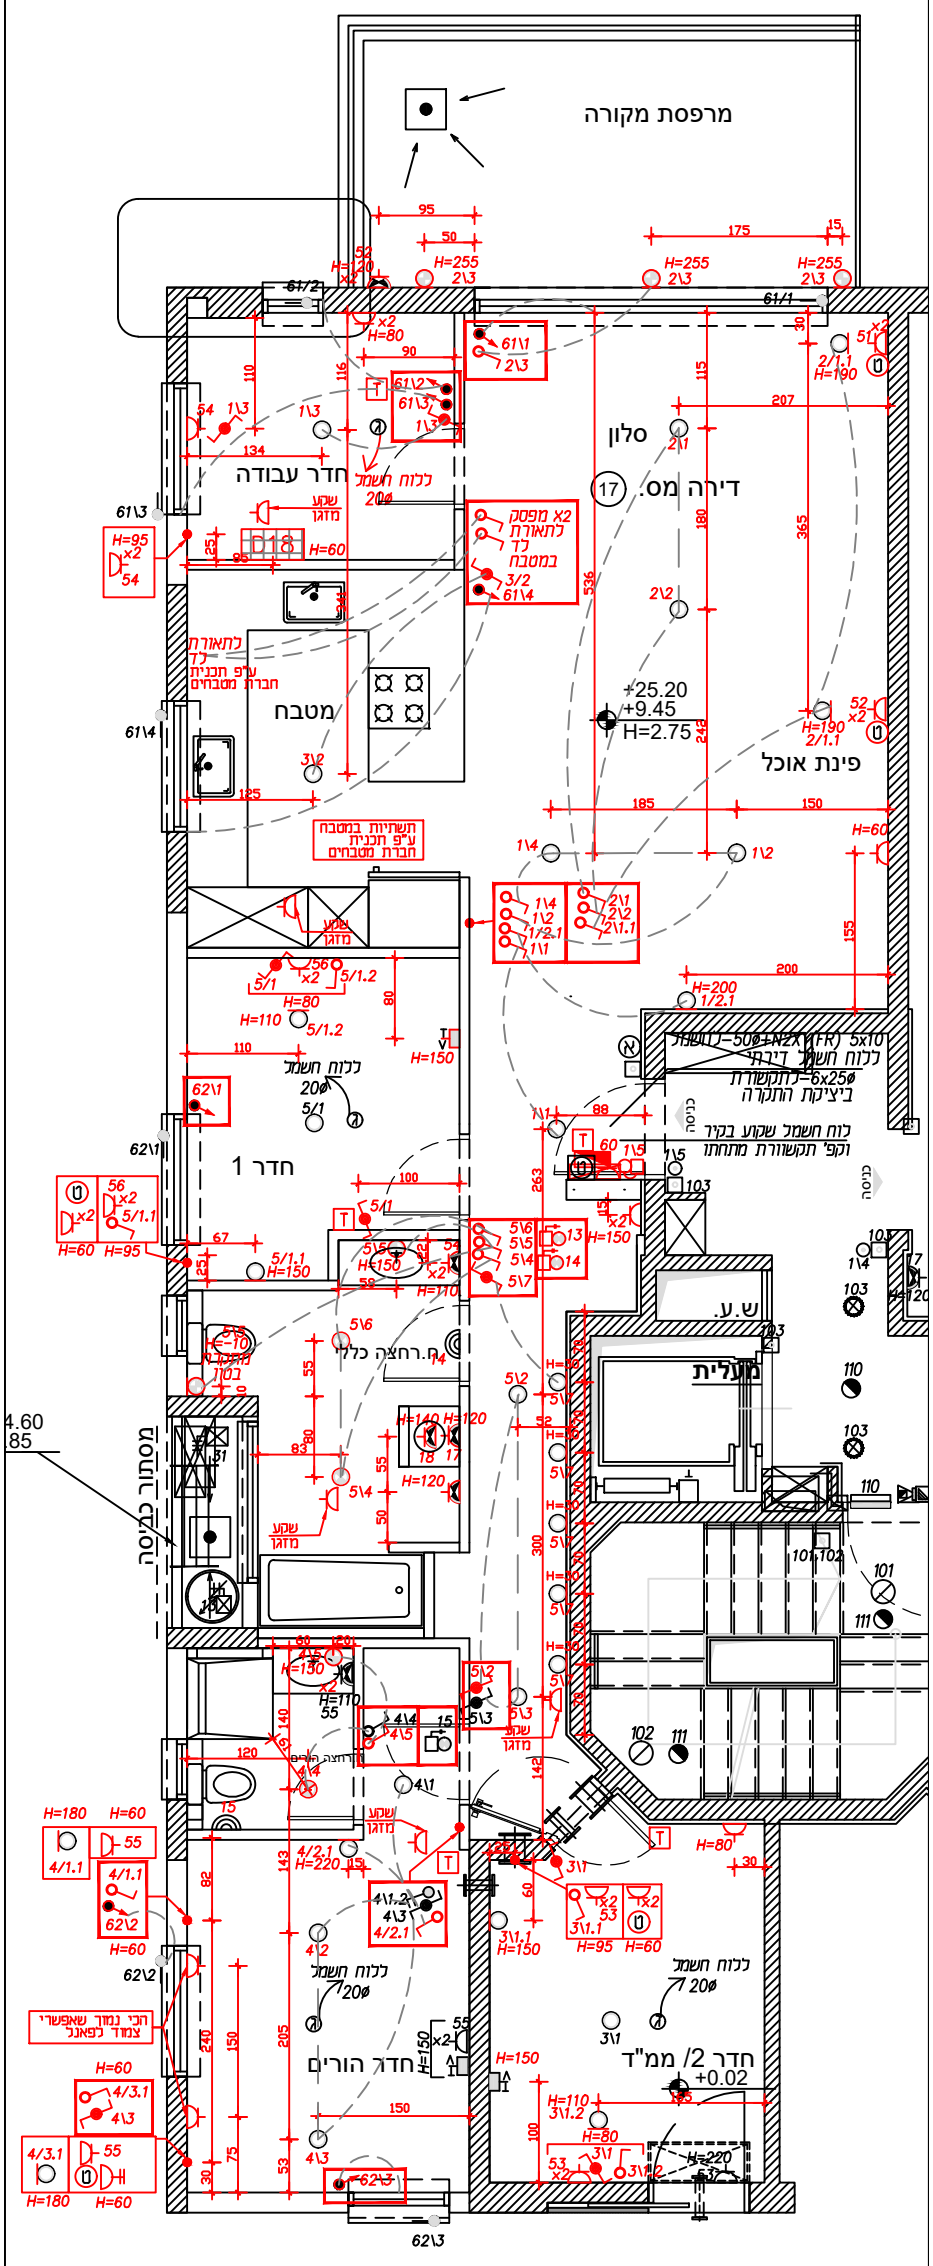


הערות:
1. על המבצע לבדוק את התאמת התכנית בשטח, לפני הבניה, ולבקר את המידות. על כל טעות ו/או אי התאמה יש לעדכן משרד מתכנן.
2. אין לקבוע מידות ע"פ שרטוט. המידות המחייבות הן המידות שנמדדו בשטח לאחר ביצוע.
3. המידות בתכנית הן ברוטו –ללא חיפוי גמר.
4. יתכנו שינויים בהתאם להוראות הביצוע הסופי.
5. כל התכניות נשארות רכוש המתכנן: אין לעשות בהן שימוש ללא אישור בכתב המתכנן.
6. כל ההערות תקפות אלא אם צוין אחרת.

RK
RUTH KOLSKY
תכנון - עיצוב - השראה

רח' יהודה הנשיא

גבול חלקה

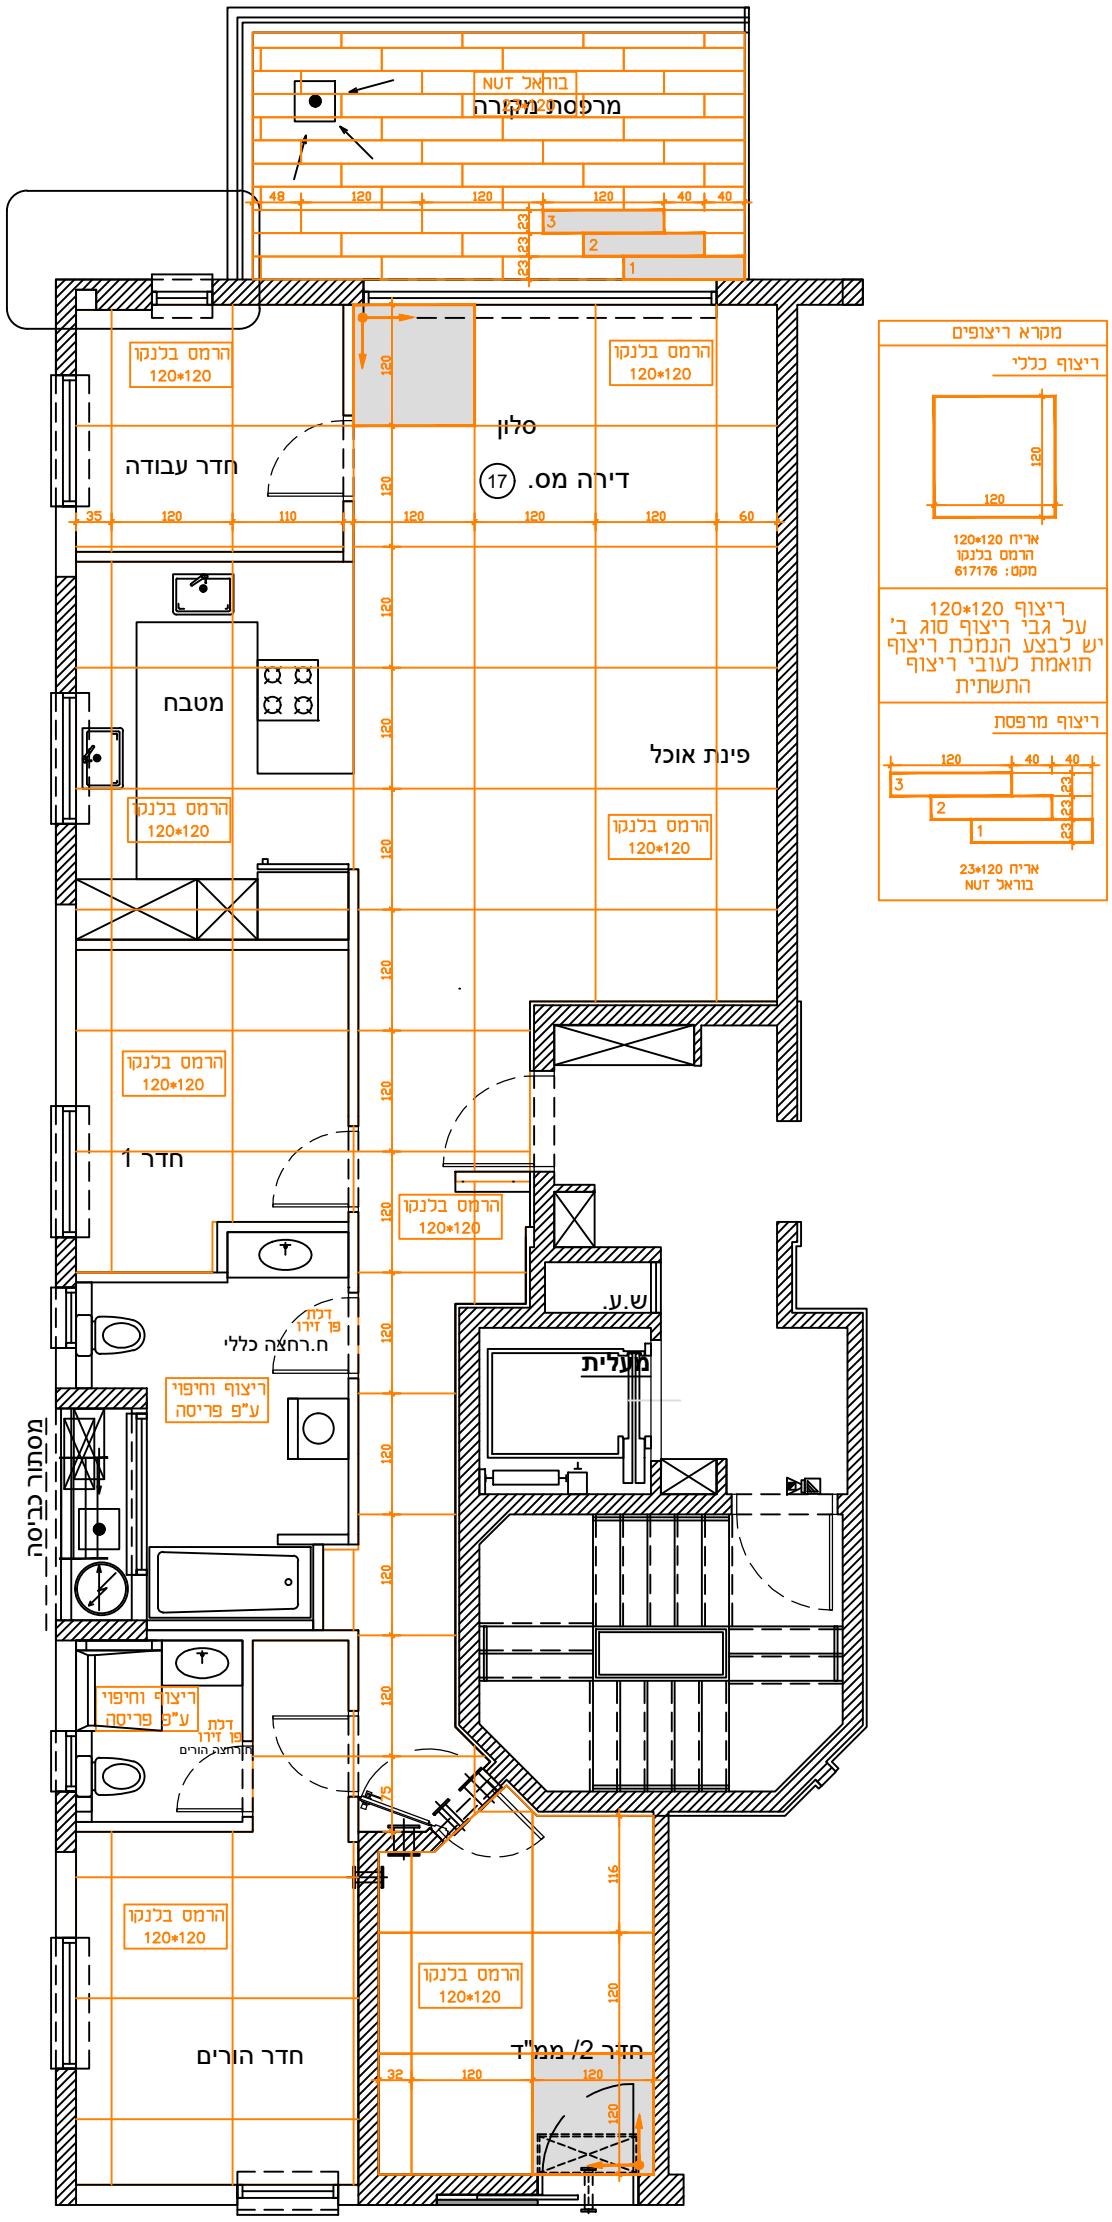

לקוח:
מרדכי וחגית פוגל

תכנית:
פריסת ריצוף כללי

כתובת:
יהודה הנשיא 12 דירה 17

גיליון מס':	גודל גיליון:	תאריך:	קנ"מ:
4	A3	4.5.26	1:75

חתימת לקוח לאישור תכנית:

_____

● לעיון ○ לאישור
○ למכרז ○ לביצוע

הערות:

1. על המבצע לבדוק את התאמת התכנית בשטח, לפני הבניה, ולבקר את המידות. על כל טעות ו/או אי התאמה יש לעדכן משרד מתכנן.
2. אין לקבוע מידות ע"פ שרטוט. המידות המחייבות הן המידות שנמדדו בשטח לאחר ביצוע.
3. המידות בתכנית הן ברוטו –ללא חיפוי גמר.
4. יתכנו שינויים בהתאם להוראות הביצוע הסופי.
5. כל התכניות נשארות רכוש המתכנן: אין לעשות בהן שימוש ללא אישור בכתב המתכנן.
6. כל ההערות תקפות אלא אם צוין אחרת.

RK
RUTH KOLSKY
תכנון - עיצוב - השראה

לקוח:
מרדכי וחגית פוגל

תכנית:
פריסות ח.רחצה הורים

כתובת:
יהודה הנשיא 12 דירה 17

גיליון מס:	גודל גיליון:	תאריך:	קנ"מ:
5	A3	4.5.26	1:30

חתימת לקוח לאישור תכנית:

_____


● לעיון ○ לאישור
○ למכרז ○ לביצוע

הערות:
1. על המבצע לבדוק את התאמת התכנית בשטח, לפני הבניה, ולבקר את המידות. על כל טעות ו/או אי התאמה יש לעדכן משרד מתכנן.
2. אין לקבוע מידות ע"פ שרטוט. המידות המחייבות הן המידות שנמדדו בשטח לאחר ביצוע.
3. המידות בתכנית הן ברוטו –ללא חיפוי גמר.
4. יתכנו שינויים בהתאם להוראות הביצוע הסופי.
5. כל התכניות נשארות רכוש המתכנן: אין לעשות בהן שימוש ללא אישור בכתב המתכנן.
6. כל ההערות תקפות אלא אם צוין אחרת.

RK
RUTH KOLSKY
תכנון - עיצוב - השראה

חדר רחצה הורים


ריצוף וחיפוי

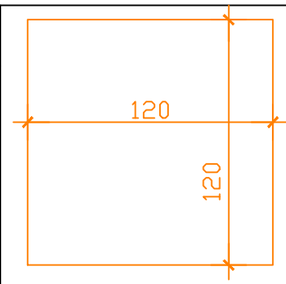

אריח R10/11 120*120
דורסט טאופה
מקט: 690155

הערות:
* פוגות בחיפוי המשכיות לפוגות בריצוף
* יש להתקין פרופילי פינות שיובאו לשטח ע"י הלקוח
* לחצן עליון מאריח: ההתקנה תתבצע ע"י בעל מקצוע מטעם הדייר במועד שיקבע מראש

יש לשים לב לכיוון הנחת האריחים. בריצוף הפסים יהיו לרוחב החדר בחיפוי לאורך הקירות

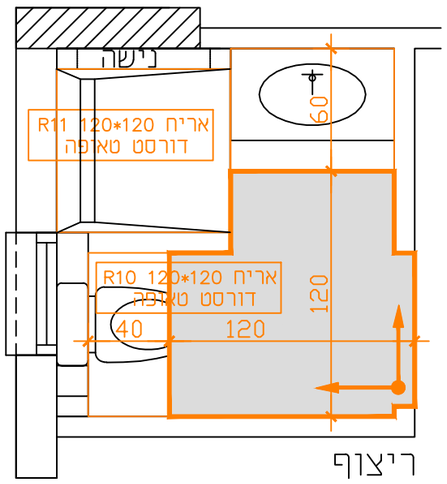


ריצוף



כיוון הנחת האריחים




כיוון הנחת האריחים

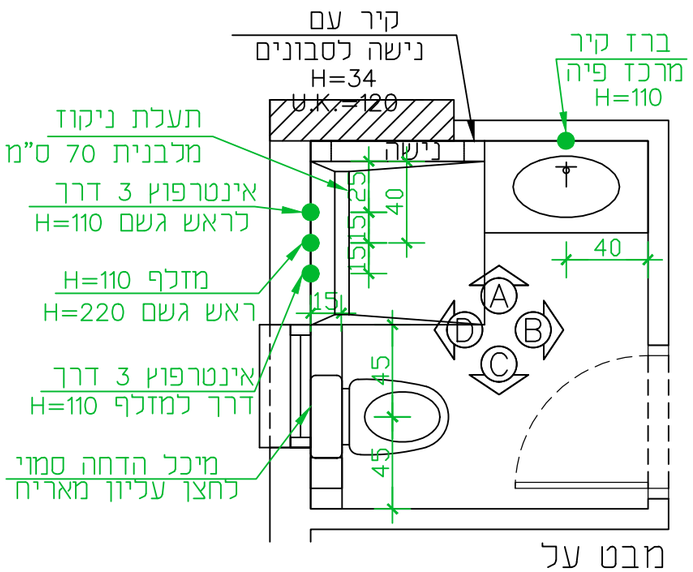


מבט על


פריסה A

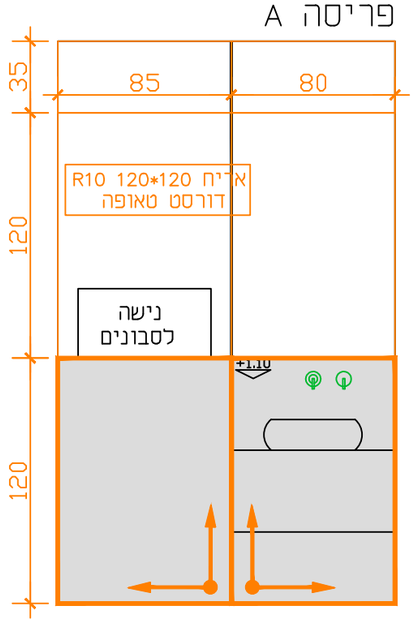


פריסה B

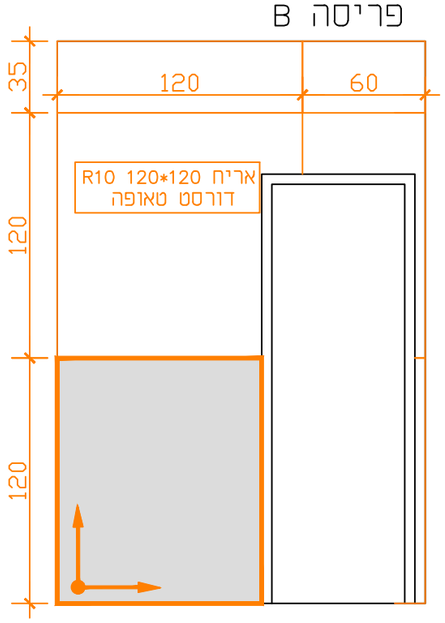

פריסה C

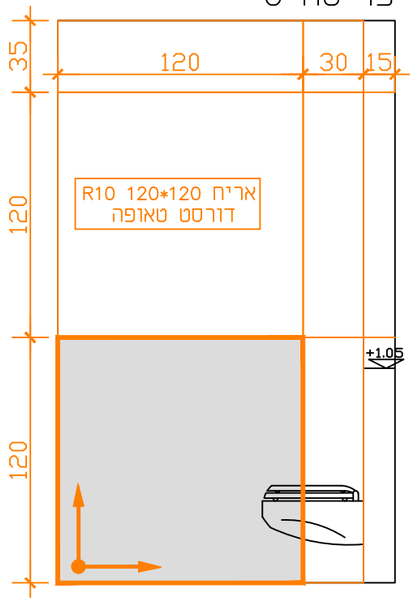


פריסה D

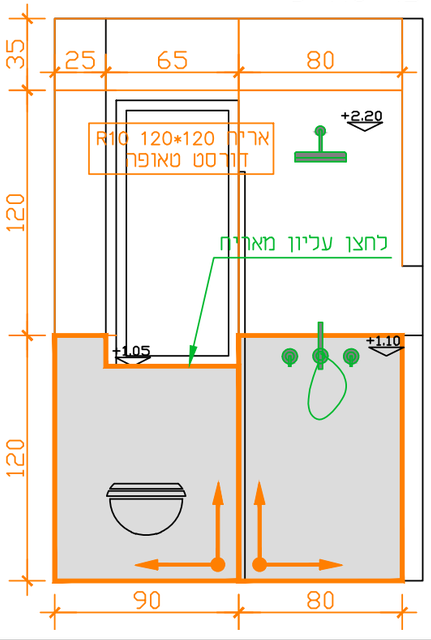

חדר רחצה כללי


ריצוף וחיפוי

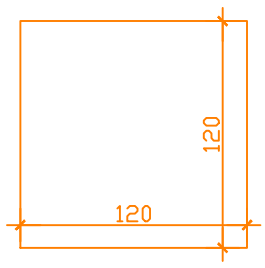


אריח R10 120*120
פורטלנד סטון טאופה
מקט: 690189

הערות:

* פוגות בחיפוי המשכיות לפוגות בריצוף
* יש להתקין פרופילי פינות שיובאו לשטח ע"י הלקוח
* לחצן עליון מאריח: ההתקנה תתבצע ע"י בעל מקצוע מטעם הדייר במועד שיקבע מראש

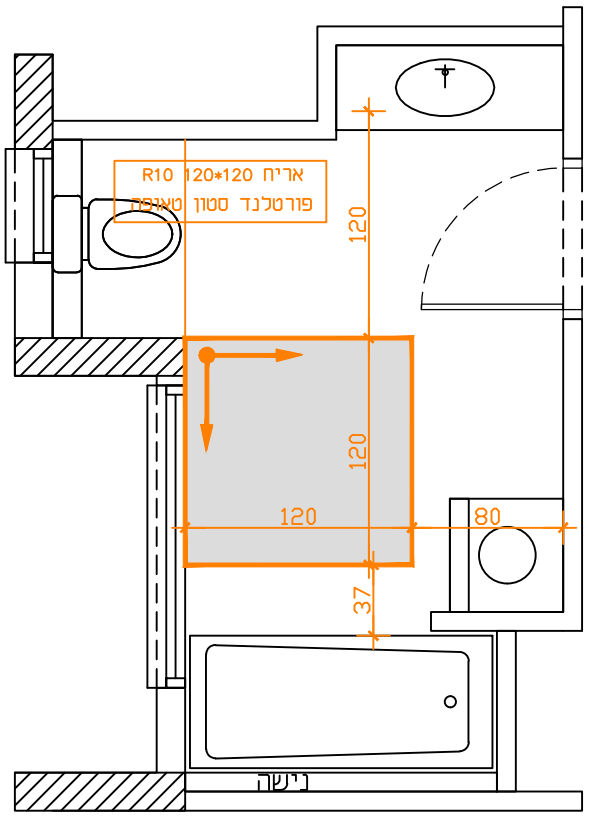


ריצוף

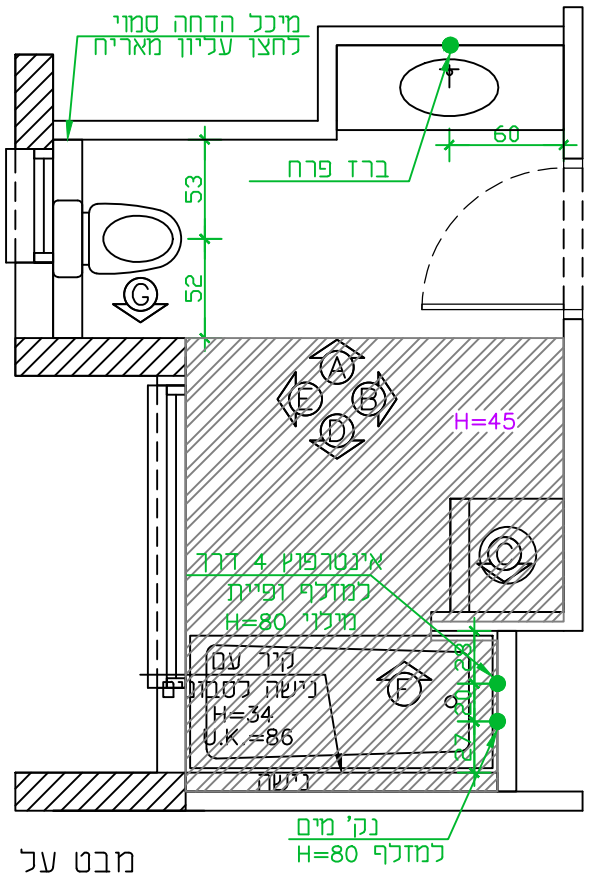


מבט על


פריסה A

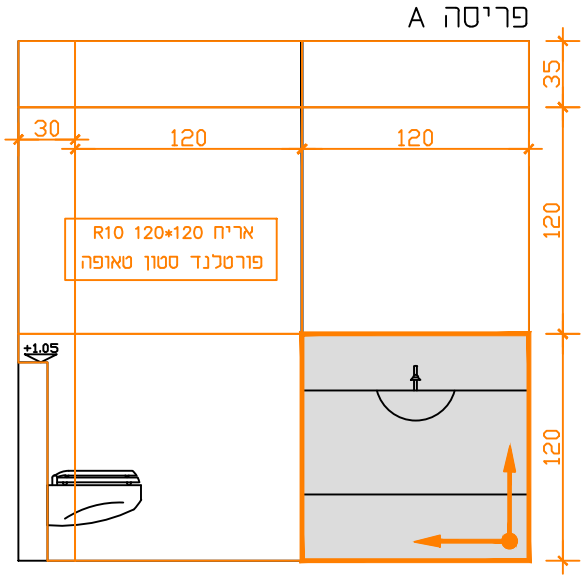


פריסה B

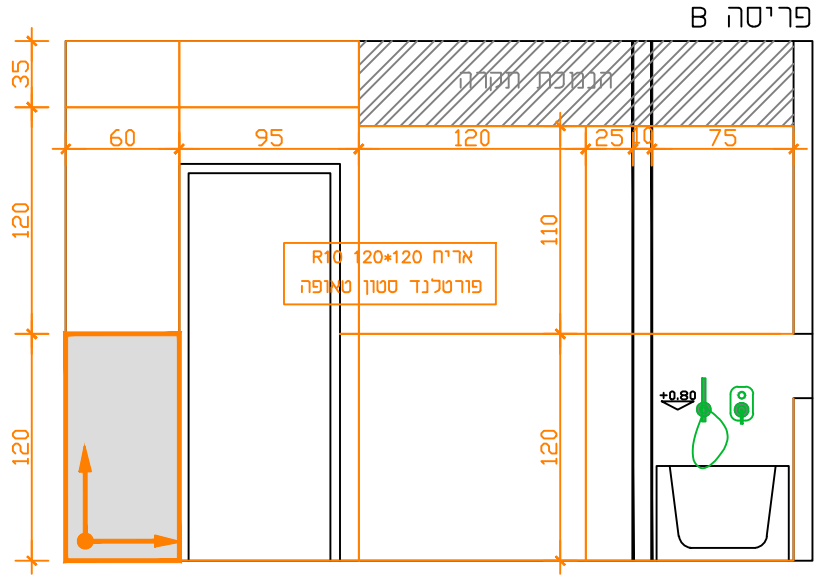


פריסה C

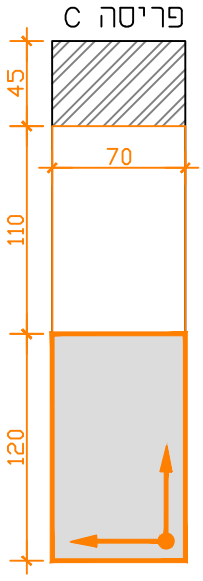


פריסה D

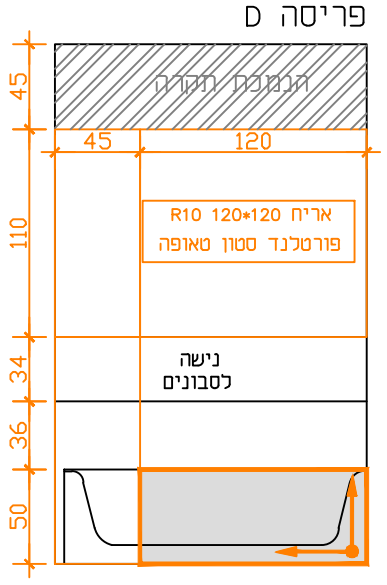


פריסה E

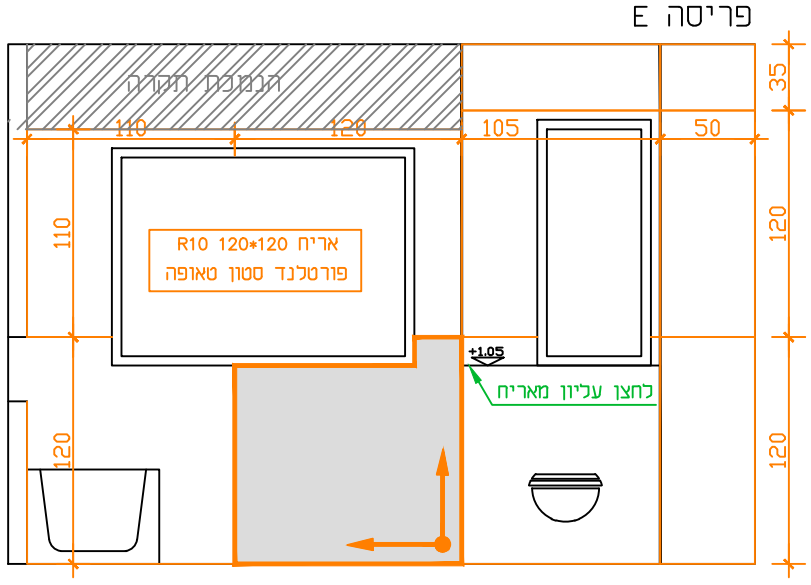

פריסה F

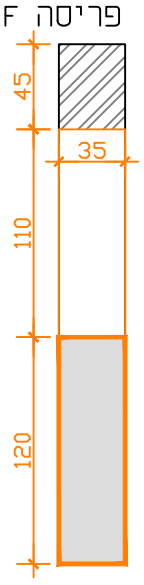

פריסה G

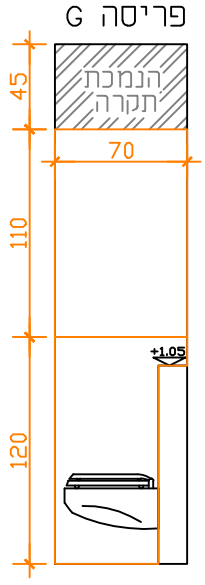

לקוח: מרדכי וחגית פוגל	כתובת: יהודה הנשיא 12 דירה 17	תכנית: פריסות ח.רחצה כללי
חתימת לקוח לאישור תכנית: _____	● לעיון ○ לאישור ○ למכרז ○ לביצוע	גיליון מס': 6 / גודל גיליון: A3 / תאריך: 4.5.26 / קנ"מ: 1:40

הערות:

1. על המבצע לבדוק את התאמת התכנית בשטח, לפני הבנייה, ולבקר את המידות. על כל טעות ו/או אי התאמה יש לעדכן משרד מתכנן.
2. אין לקבוע מידות ע"פ שרטוט. המידות המחייבות הן המידות שנמדדו בשטח לאחר ביצוע.
3. המידות בתכנית הן ברוטו–ללא חיפוי גמר.
4. יתכנו שינויים בהתאם להוראות הביצוע הסופי.
5. כל התכניות נשארות רכוש המתכנן: אין לעשות בהן שימוש ללא אישור בכתב המתכנן.
6. כל ההערות תקפות אלא אם צוין אחרת.

RK
RUTH KOLSKY
תכנון - עיצוב - השראה